




3D DRAWINGS FOR VISUALISATION PURPOSES

SHEET LIST

SHEET NO.	SHEET NAME
A-00-01	COVER SHEET
A-00-02	PERSPECTIVES
A-00-03	INTERNAL PERSPECTIVES
A-00-04	BACKYARD PERSPECTIVES
A-00-05	3D SITE VIEW
A-00-06	3D SLAB VIEW
A-00-07	GENERAL NOTES
A-01-01	SITE PLAN
A-01-02	EARTHWORKS PLAN
A-01-03	SLAB SETOUT
A-01-04	DRAINAGE PLAN
A-02-01	GROUND FLOOR PLAN
A-02-02	LEVEL 1 FLOOR PLAN
A-02-03	ROOF PLAN
A-02-04	GROUND CEILING PLAN
A-02-05	LEVEL 1 CEILING PLAN
A-03-01	PROPOSED ELEVATIONS
A-03-02	PROPOSED ELEVATIONS
A-03-03	POOL PLAN
A-03-04	FENCE ELEVATIONS
A-04-01	SECTIONS
A-04-02	SECTIONS
A-04-03	STAIR DETAIL
A-04-05	SECTION DETAILS
A-04-06	FACADE CALLOUT
A-04-07	LAUNDRY CHUTE
A-05-00	FIXED JOINERY NOTES
A-05-01	INTERNALS - KITCHEN
A-05-02	INTERNALS - LAUNDRY
A-05-03	INTERNALS - LOWER BATHROOM
A-05-04	INTERNALS - UPPER BATHROOM
A-05-05	INTERNALS - UPPER TOILET
A-05-06	INTERNALS - ENSUITE
A-05-07	INTERNALS - WIR
A-05-08	INTERNALS - WARDROBES
A-05-09	INTERNALS - BBQ AREA
A-05-10	INTERNALS - TV CABINET
A-06-01	GROUND FLOOR FINISHES PLAN
A-06-02	LEVEL 1 FINISHES PLAN
A-06-03	GROUND FLOOR CLADDING DIAGRAM
A-06-04	LEVEL 1 CLADDING DIAGRAM
A-06-05	GROUND ELECTRICAL PLAN
A-06-06	LEVEL 1 ELECTRICAL PLAN
A-07-01	DOOR SCHEDULE
A-07-02	WINDOW SCHEDULE
A-07-09	SIZING SCHEDULE

GRAND TOTAL: 46

DATE	DESCRIPTION	REV. NO.	DRAWING TITLE :		SCALE :	
03-02-2026	TECHNICAL UPDATES	H				
10-02-2026	TECHNICAL UPDATES	I				
18-02-2026	CONSTRUCTION REVIEW	J				
PILGRIM retains copyright in all documents and drawings and in any works executed from those documents and drawings. The PILGRIM reserves all present and future moral rights in all intellectual property in the designs, the documents, drawings and any works executed or to be executed from them. PILGRIM by agreement grants the client a license to use the documents and drawings to produce the project, for which they were intended, conditional upon the following: - the license applies only to the site or that part of the site to which the design relates. - PILGRIM has completed the particular stage or stages of design service for which PILGRIM has been commissioned. - fees properly due to the designer have been paid in full. Do not scale from drawings, verify all dimensions prior to commencement of construction or fabrication, notify the designer of any discrepancies.			COVER SHEET		MADELEINE & NICHOLAS CHILDS	
			106 HAROLD STREET, HOLLAND PARK		PILGRIM[®]	
					ABN: 89 639 943 187 QBCC: 1523 8743	
					DRAWN : TH CHECK BY : CA	
					DRAWING NO: A-00-01	
					DATE 18-02-2026	REV J

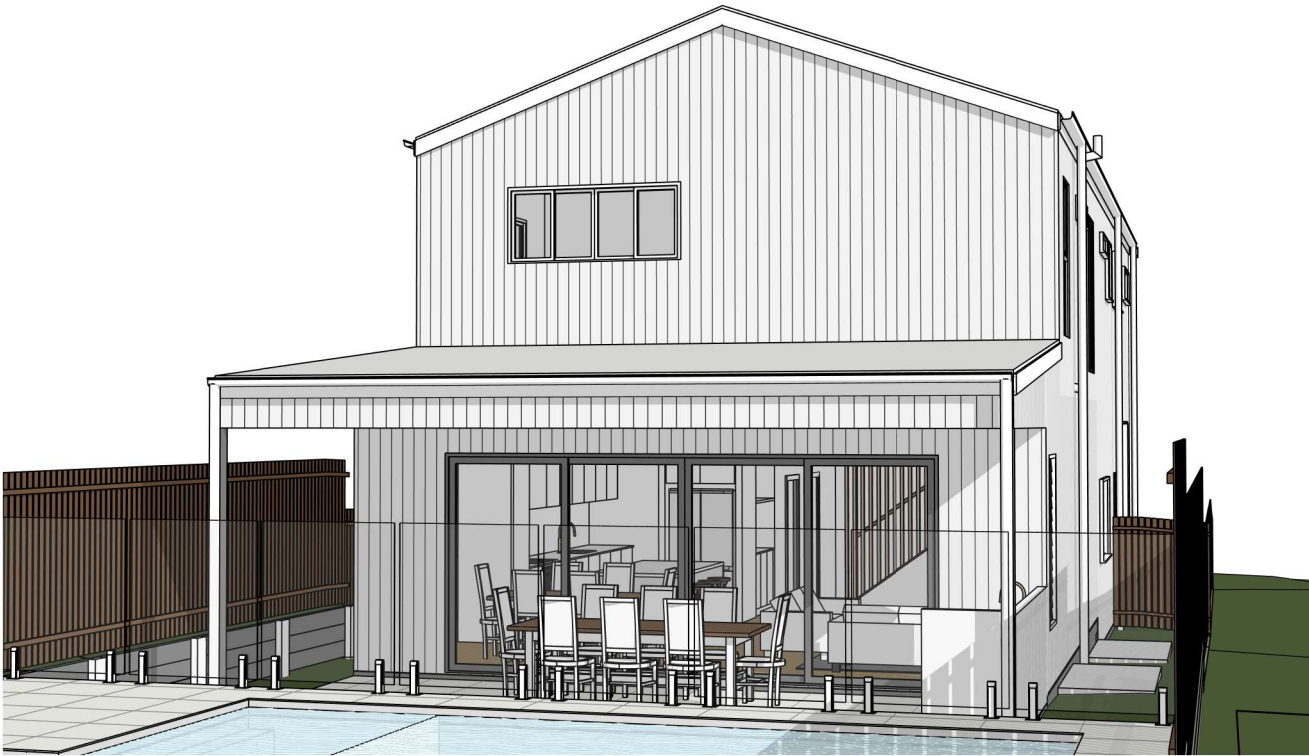

3D DRAWINGS FOR VISUALISATION PURPOSES

DATE	DESCRIPTION	REV. NO.	DRAWING TITLE :		SCALE :	
03-02-2026	TECHNICAL UPDATES	H	PERSPECTIVES	MADELEINE & NICHOLAS CHILDS	ABN: 89 639 943 187 QBCC: 1523 8743	
10-02-2026	TECHNICAL UPDATES	I				
18-02-2026	CONSTRUCTION REVIEW	J				
PILGRIM retains copyright in all documents and drawings and in any works executed from those documents and drawings. The PILGRIM reserves all present and future moral rights in all intellectual property in the designs, the documents, drawings and any works executed or to be executed from them. PILGRIM by agreement grants the client a license to use the documents and drawings to produce the project, for which they were intended, conditional upon the following: - the license applies only to the site or that part of the site to which the design relates. - PILGRIM has completed the particular stage or stages of design service for which PILGRIM has been commissioned. - fees properly due to the designer have been paid in full. Do not scale from drawings, verify all dimensions prior to commencement of construction or fabrication, notify the designer of any discrepancies.			106 HAROLD STREET, HOLLAND PARK		PILGRIM [®]	
					DRAWING NO: A-00-02	
					DATE 18-02-2026	REV J



3D DRAWINGS FOR VISUALISATION PURPOSES

DATE	DESCRIPTION	REV. NO.
03-02-2026	TECHNICAL UPDATES	H
10-02-2026	TECHNICAL UPDATES	I
18-02-2026	CONSTRUCTION REVIEW	J

PILGRIM retains copyright in all documents and drawings and in any works executed from those documents and drawings. The PILGRIM reserves all present and future moral rights in all intellectual property in the designs, the documents, drawings and any works executed or to be executed from them.



PILGRIM by agreement grants the client a license to use the documents and drawings to produce the project, for which they were intended, conditional upon the following:

- the license applies only to the site or that part of the site to which the design relates,
- PILGRIM has completed the particular stage or stages of design service for which PILGRIM has been commissioned,
- fees properly due to the designer have been paid in full.

Do not scale from drawings, verify all dimensions prior to commencement of construction or fabrication, notify the designer of any discrepancies.



DRAWING TITLE :	INTERNAL PERSPECTIVES	MADELEINE & NICHOLAS CHILDS
106 HAROLD STREET, HOLLAND PARK		

SCALE :	
ABN: 89 639 943 187	
QBCC: 1523 8743	
DRAWN : TH	CHECK BY : CA
DRAWING NO: A-00-03	
DATE 18-02-2026	REV J

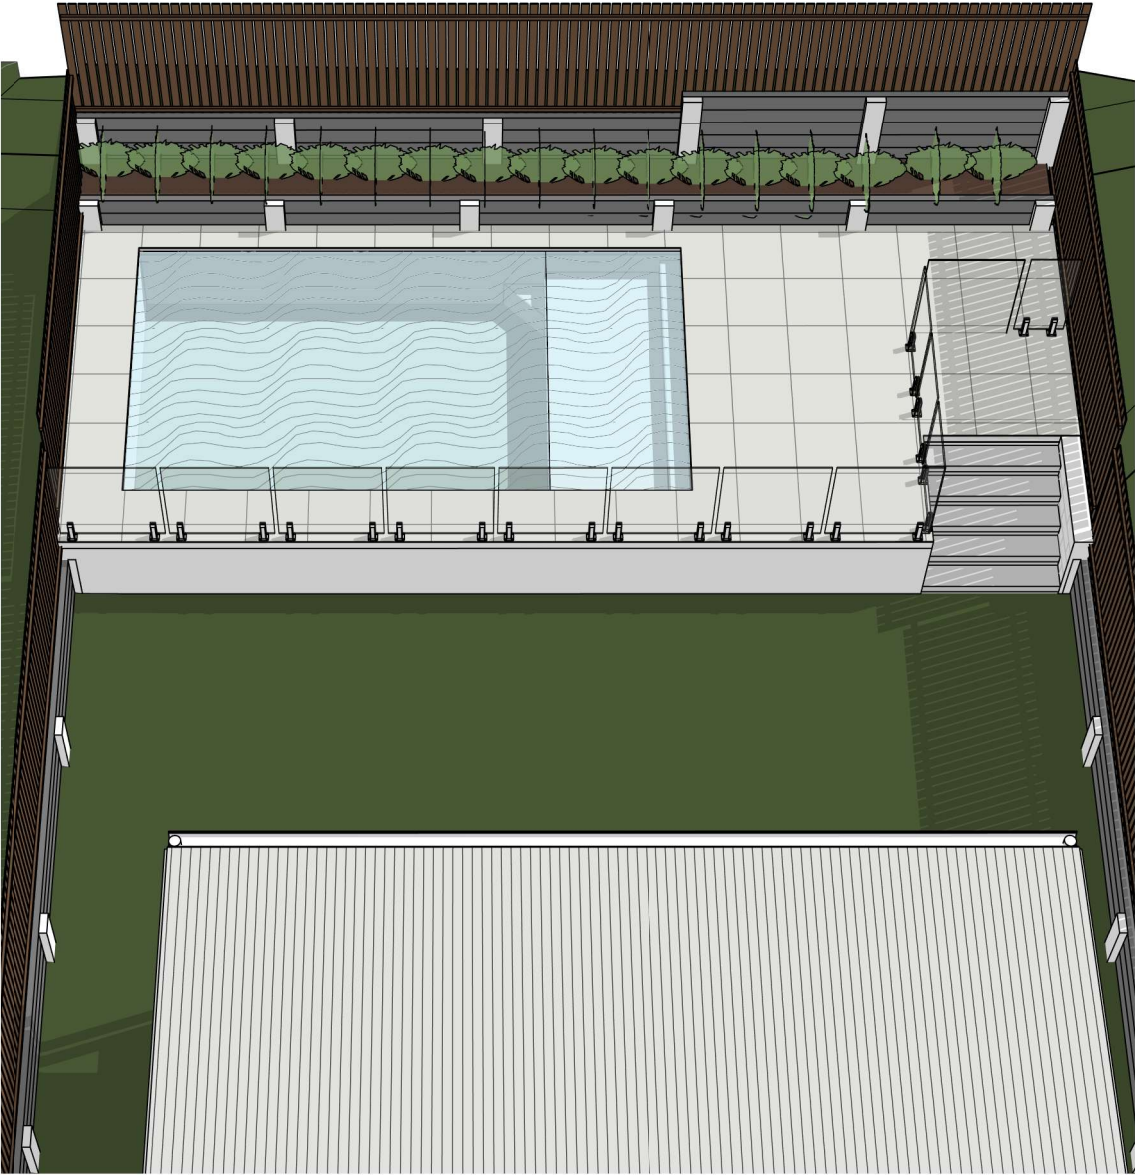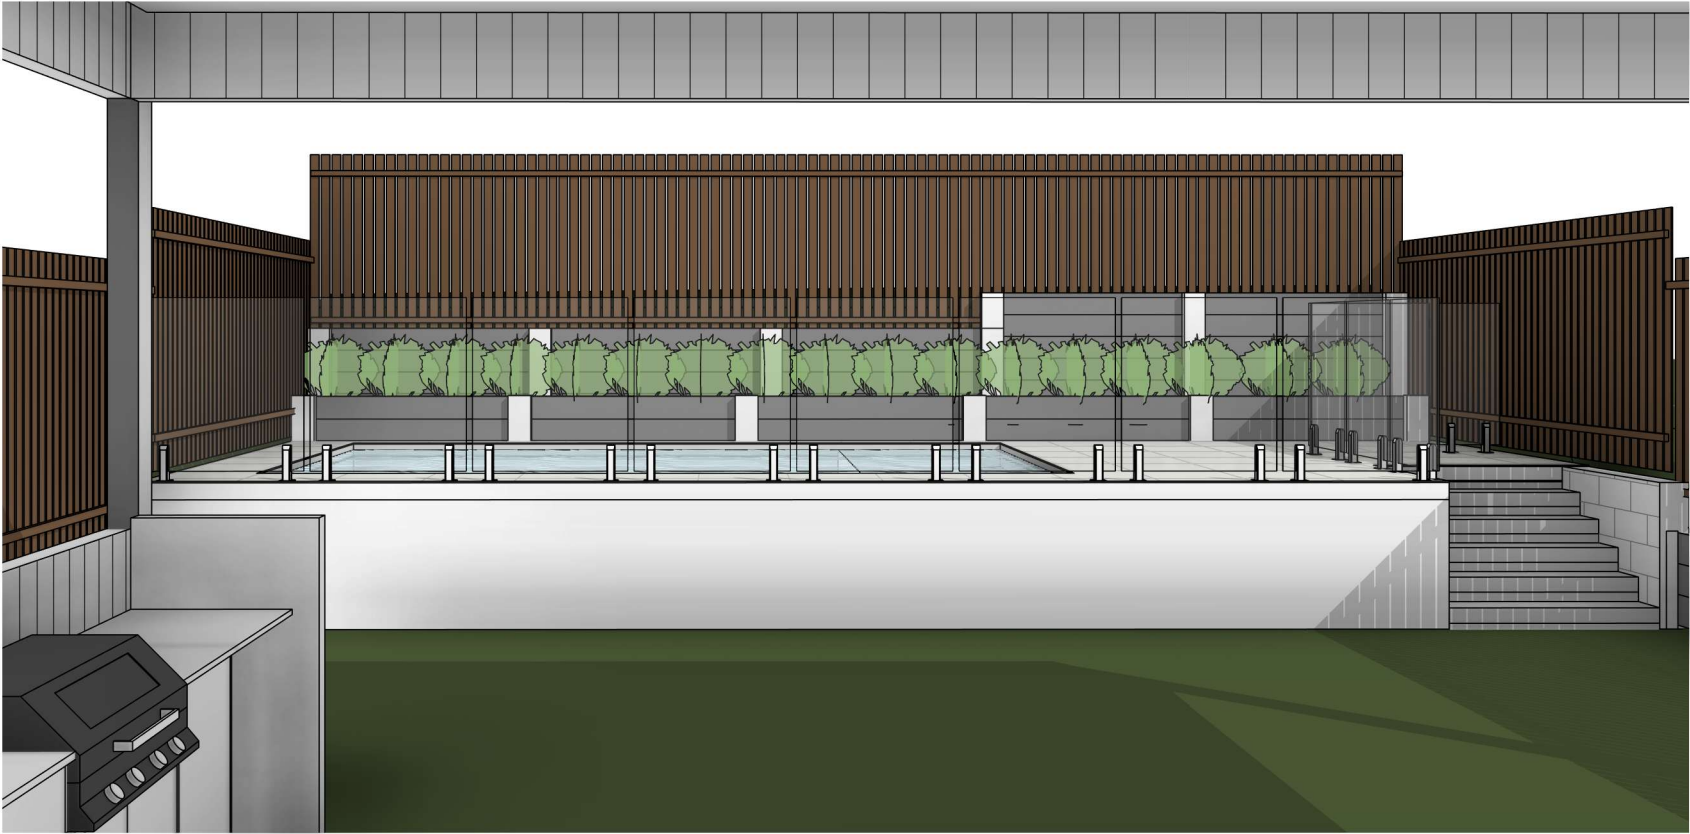

3D DRAWINGS FOR VISUALISATION PURPOSES

DATE	DESCRIPTION	REV. NO.	DRAWING TITLE :		SCALE :	
03-02-2026	TECHNICAL UPDATES	H				
10-02-2026	TECHNICAL UPDATES	I				
18-02-2026	CONSTRUCTION REVIEW	J				
PILGRIM retains copyright in all documents and drawings and in any works executed from those documents and drawings. The PILGRIM reserves all present and future moral rights in all intellectual property in the designs, the documents, drawings and any works executed or to be executed from them. PILGRIM by agreement grants the client a license to use the documents and drawings to produce the project, for which they were intended, conditional upon the following: - the license applies only to the site or that part of the site to which the design relates, - PILGRIM has completed the particular stage or stages of design service for which PILGRIM has been commissioned, - fees properly due to the designer have been paid in full. Do not scale from drawings, verify all dimensions prior to commencement of construction or fabrication, notify the designer of any discrepancies.			BACKYARD PERSPECTIVES		MADELEINE & NICHOLAS CHILDS	
			106 HAROLD STREET, HOLLAND PARK		PILGRIM[®]	
					DRAWN : TH CHECK BY : CA	
					DRAWING NO: A-00-04	
					DATE 18-02-2026	REV J

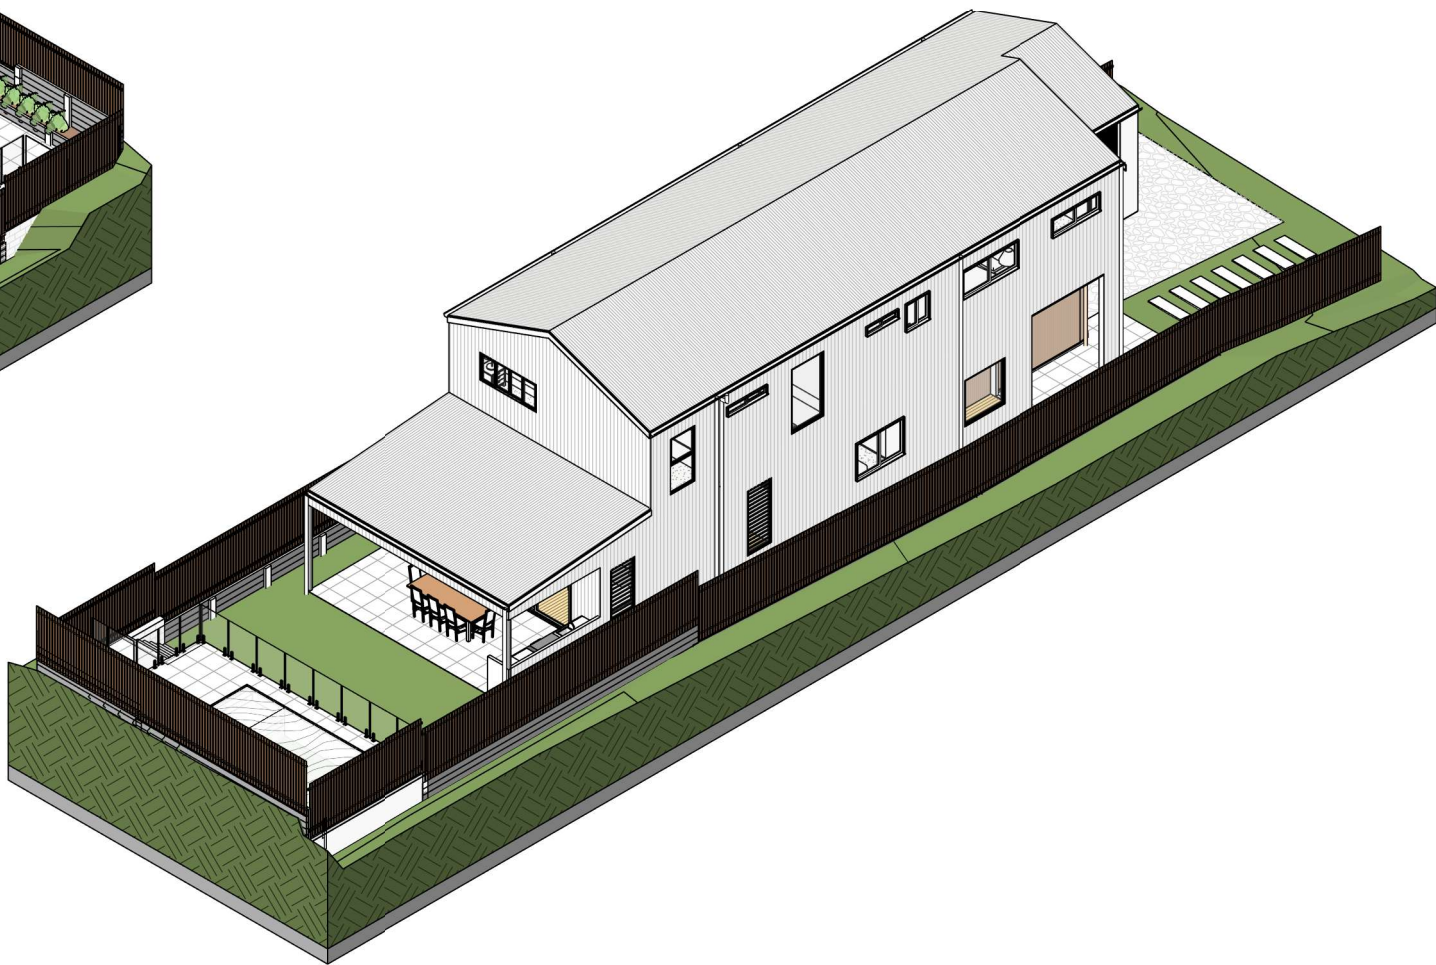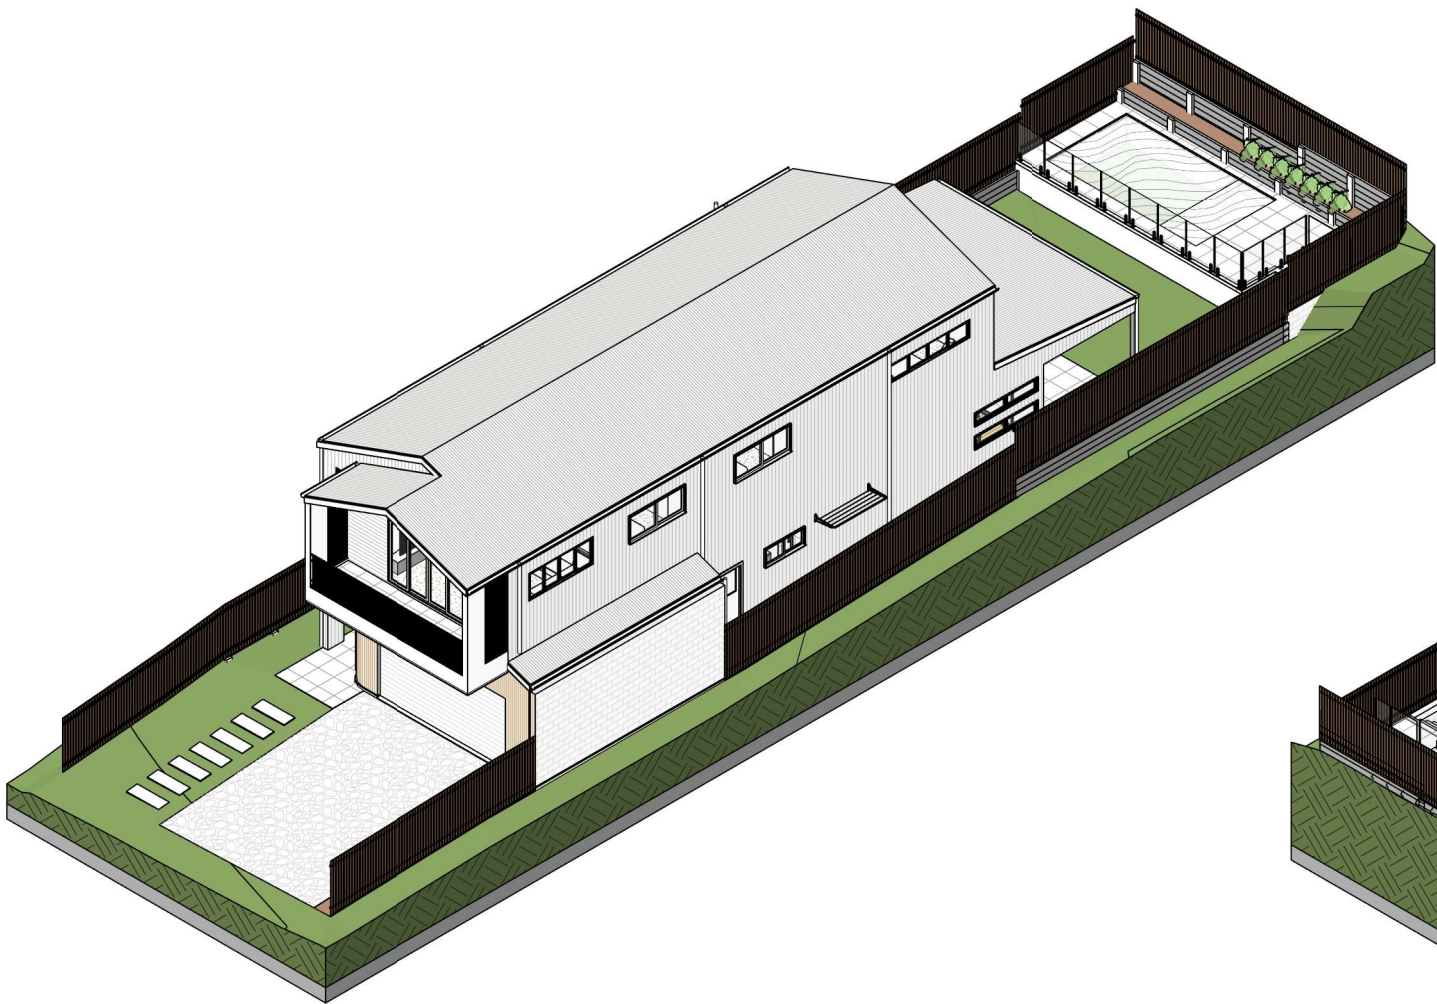

DATE	DESCRIPTION	REV. NO.
03-02-2026	TECHNICAL UPDATES	H
10-02-2026	TECHNICAL UPDATES	I
18-02-2026	CONSTRUCTION REVIEW	J

PILGRIM retains copyright in all documents and drawings and in any works executed from those documents and drawings. The PILGRIM reserves all present and future moral rights in all intellectual property in the designs, the documents, drawings and any works executed or to be executed from them.


PILGRIM by agreement grants the client a license to use the documents and drawings to produce the project, for which they were intended, conditional upon the following:

- the license applies only to the site or that part of the site to which the design relates,
- PILGRIM has completed the particular stage or stages of design service for which PILGRIM has been commissioned,
- fees properly due to the designer have been paid in full.

Do not scale from drawings, verify all dimensions prior to commencement of construction or fabrication, notify the designer of any discrepancies.

DRAWING TITLE :	MADELEINE & NICHOLAS CHILDS
3D SITE VIEW	
106 HAROLD STREET, HOLLAND PARK	

SCALE :	
ABN: 89 639 943 187	
QBCC: 1523 8743	
DRAWN : TH	CHECK BY : CA
DRAWING NO: A-00-05	
DATE 18-02-2026	REV J

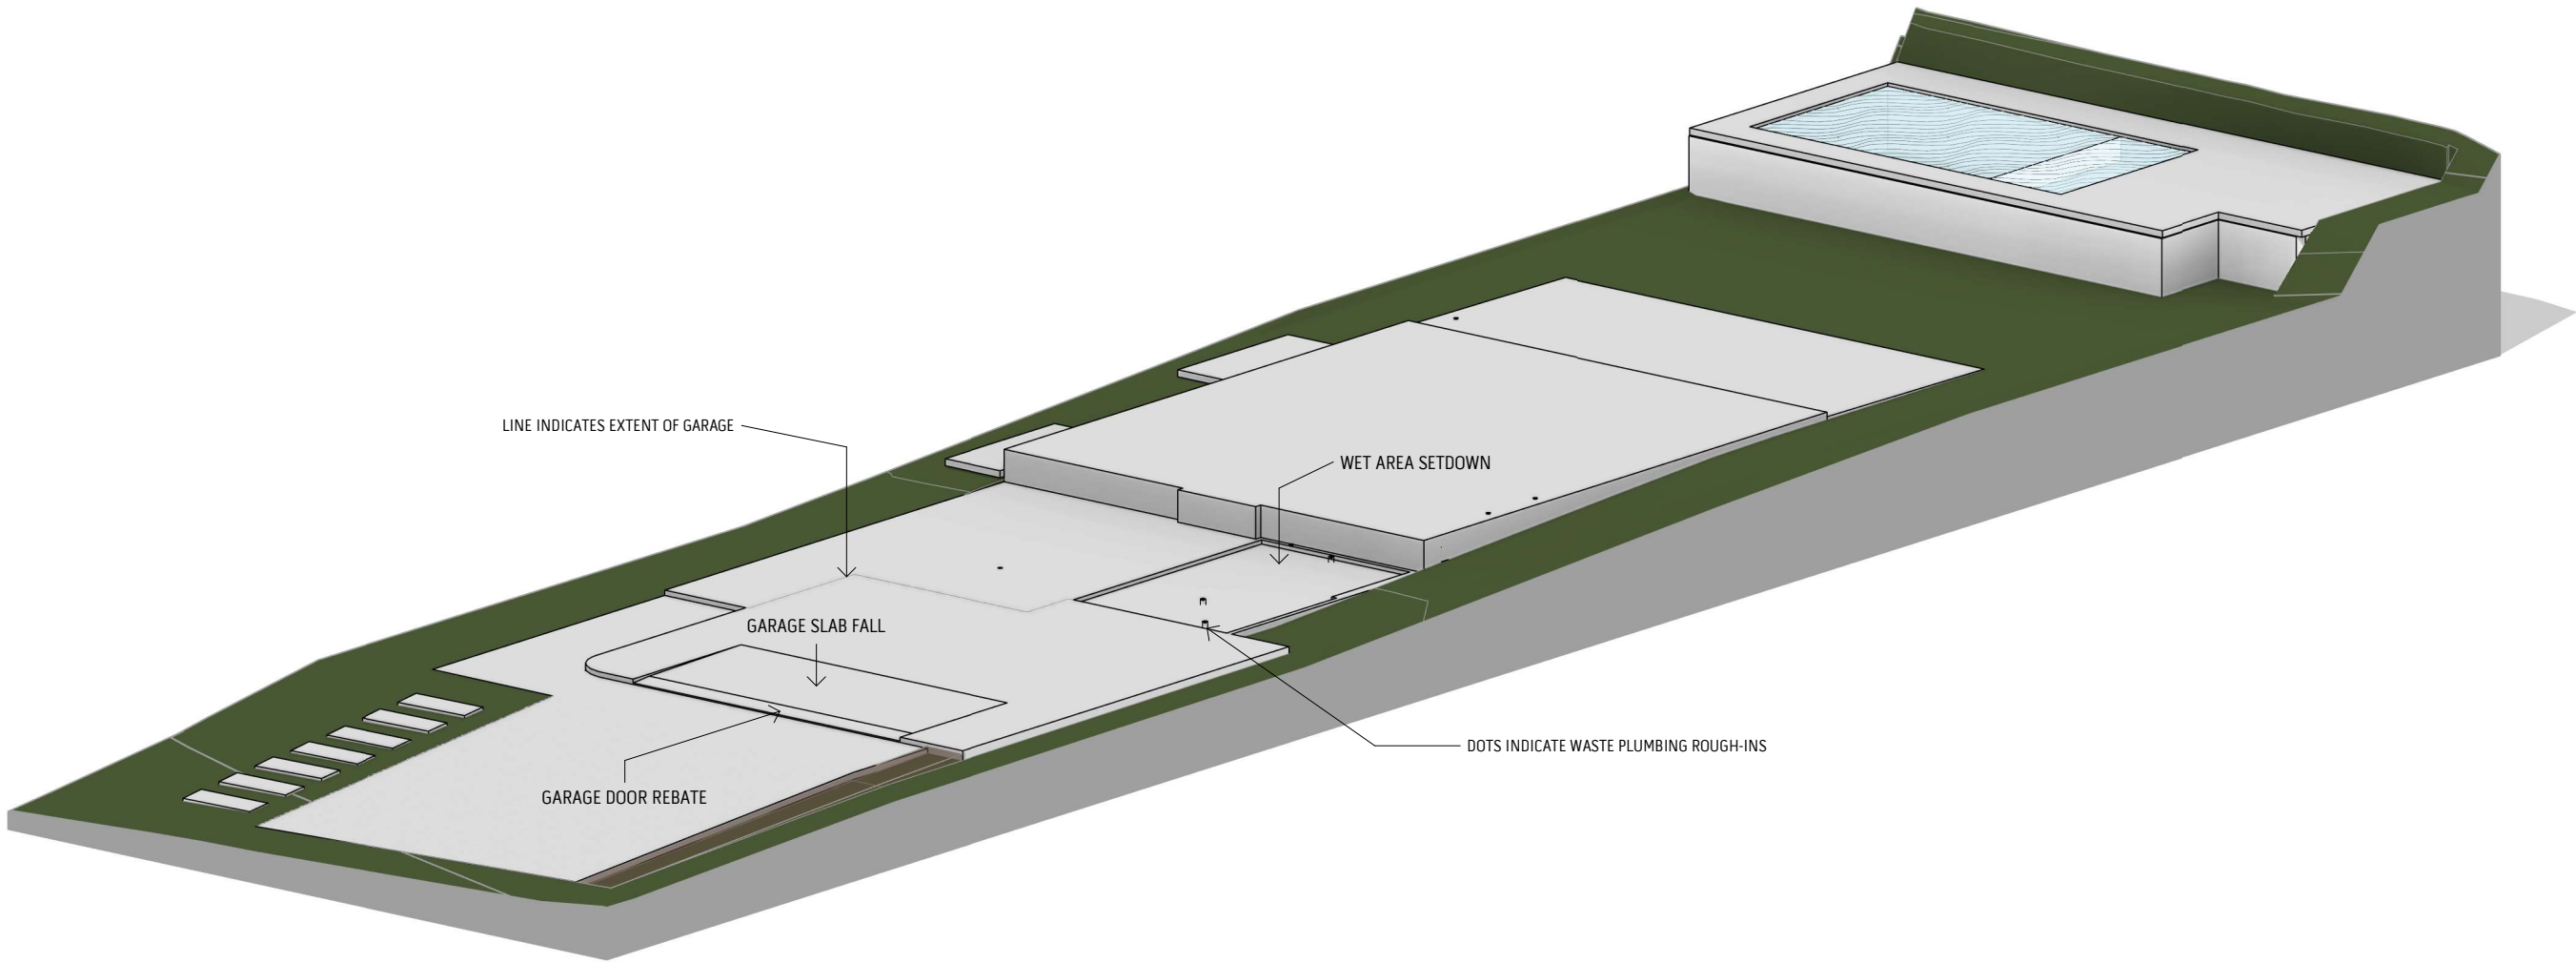

DATE	DESCRIPTION	REV. NO.
03-02-2026	TECHNICAL UPDATES	H
10-02-2026	TECHNICAL UPDATES	I
18-02-2026	CONSTRUCTION REVIEW	J

PILGRIM retains copyright in all documents and drawings and in any works executed from those documents and drawings.

The PILGRIM reserves all present and future moral rights in all intellectual property in the designs, the documents, drawings and any works executed or to be executed from them.

PILGRIM by agreement grants the client a license to use the documents and drawings to produce the project, for which they were intended, conditional upon the following:

- the license applies only to the site or that part of the site to which the design relates.

- PILGRIM has completed the particular stage or stages of architectural service for which PILGRIM has been commissioned.

- fees properly due to the designer have been paid in full.

Do not scale from drawings, verify all dimensions prior to commencement of construction or fabrication, notify the designer of any discrepancies.

DRAWING TITLE :

3D SLAB VIEW

MADELEINE & NICHOLAS CHILDS

106 HAROLD STREET, HOLLAND PARK

SCALE :		
DRAWN :	TH	CHECK BY : CA
DRAWING NO: A-00-06		
DATE	18-02-2026	REV J

1. GENERAL

- THESE DRAWINGS ARE TO BE READ IN CONJUNCTION WITH ALL CONSULTANT DOCUMENTATION INCLUDING STRUCTURAL, HYDRAULIC, ELECTRICAL, ENERGY EFFICIENCY, POOL AND LANDSCAPE DRAWINGS
- DO NOT SCALE FROM DRAWINGS. VERIFY ALL DIMENSIONS, LEVELS AND SITE CONDITIONS ON SITE PRIOR TO COMMENCEMENT OF CONSTRUCTION
- ANY DISCREPANCIES BETWEEN DRAWINGS, SPECIFICATIONS OR CONSULTANT DOCUMENTS ARE TO BE REPORTED TO THE DESIGNER PRIOR TO PROCEEDING
- ALL WORKS TO BE CARRIED OUT BY SUITABLY LICENSED CONTRACTORS IN ACCORDANCE WITH CURRENT LEGISLATION AND CODES
- THE BUILDER IS RESPONSIBLE FOR COORDINATION OF ALL TRADES AND COMPLIANCE WITH STATUTORY REQUIREMENTS

2. NCC COMPLIANCE BASIS

- BUILDING CLASSIFICATION: CLASS 1A DWELLING (PRIMARY DWELLING) WITH ASSOCIATED CLASS 10A STRUCTURES (GARAGE, POOL, FENCING)
- CONSTRUCTION TO COMPLY WITH NCC 2022, ABCB HOUSING PROVISIONS, AND RELEVANT AUSTRALIAN STANDARDS
- DEEMED-TO-SATISFY PROVISIONS ADOPTED UNLESS NOTED OTHERWISE
- PERFORMANCE SOLUTIONS, IF REQUIRED, TO BE DEVELOPED AND CERTIFIED BY OTHERS

3. STRUCTURAL COORDINATION

- ALL FOOTINGS, SLABS, FRAMING, BRACING AND TIE-DOWNS TO COMPLY WITH NCC 2022 HP PART 10.3 AND RELEVANT AUSTRALIAN STANDARDS
- STRUCTURAL ELEMENTS ARE SHOWN DIAGRAMMATICALLY ONLY. REFER TO STRUCTURAL ENGINEER'S DRAWINGS FOR SIZES, REINFORCEMENT, MEMBER SPACING AND CONNECTIONS
- TIMBER FRAMING TO COMPLY WITH AS 1684 SERIES
- ROOF TRUSSES TO BE DESIGNED, CERTIFIED AND INSTALLED IN ACCORDANCE WITH MANUFACTURE'S DOCUMENTATION AND ENGINEER'S DETAILS

4. SITE, EARTHWORKS & LEVELS

- FINISHED FLOOR LEVELS (FFLs) AND SETBACKS TO COMPLY WITH APPROVED PLANNING CONDITIONS AND SURVEY INFORMATION
- CUT, FILL AND RETAINING WALLS TO BE CONSTRUCTED IN ACCORDANCE WITH ENGINEER'S DOCUMENTATION
- SURFACE WATER TO BE DIRECTED AWAY FROM THE BUILDING IN ACCORDANCE WITH NCC 2022 HP 10.1.2

5. FIRE SEPARATION & BOUNDARY CONDITIONS

- FIRE-RESISTING CONSTRUCTION TO COMPLY WITH NCC 2022 HP PART 9.2 WHERE APPLICABLE
- BOUNDARY WALLS AND ELEMENTS NOMINATED AS FIRE-RATED TO ACHIEVE THE REQUIRED FRL AS INDICATED ON DRAWINGS
- OPENINGS, PENETRATIONS AND SERVICES THROUGH FIRE-RESISTING ELEMENTS TO BE PROTECTED IN ACCORDANCE WITH NCC REQUIREMENTS

6. WET AREAS & WATERPROOFING

- WET AREAS TO COMPLY WITH NCC 2022 HP PART 10.2
- WATERPROOFING TO BE INSTALLED IN ACCORDANCE WITH AS 3740
- FALLS TO FLOOR WASTES TO BE PROVIDE AS NOTED ON DRAWINGS (MINIMUM 1:80 TO SHOWERS, 1:100 TO OTHER WET AREAS UNLESS NOTED OTHERWISE)
- WATERSTOPS TO BE INSTALLED AT DOORWAYS AND JUNCTIONS AS REQUIRED

7. STAIRWAYS, BALUSTRADES & FALL PREVENTION

- STAIRWAYS TO COMPLY WITH NCC 2022 HP PART 11.2
- BALUSTRADES, HANDRAILS AND FALL PREVENTION TO COMPLY WITH NCC HP PART 11.3
- MAXIMUM RISER HEIGHTS, MINIMUM GOINGS, HANDRAIL HEIGHTS AND BALUSTRADE OPENING TO MEET NCC REQUIREMENTS

8. GLAZING, DOORS & WINDOWS

- GLAZING TO COMPLY WITH AS 1288 AND NCC 2022 HP PART 10.4
- SAFETY GLAZING TO BE PROVIDED WHERE REQUIRED
- WINDOW AND DOOR PERFORMANCE TO ALIGN WITH THE APPROVED ENERGY EFFICIENCY REPORT

9. ROOFING & RAINWATER DISPOSAL

- ROOF CONSTRUCTION TO COMPLY WITH NCC 2022 HP PART 10.3
- ROOFING, FLASHINGS, GUTTER AND DOWNPIPES TO COMPLY WITH MANUFACTURER REQUIREMENTS AND AS 3500.3
- ROOFWATER TO BE DISCHARGED TO A LAWFUL POINT OF DISCHARGE

10. PLUMBING & DRAINAGE

- PLUMBING AND DRAINAGE TO COMPLY WITH AS 3500 SERIES AND LOCAL AUTHORITY REQUIREMENTS
- STORMWATER AND SEWER SYSTEMS TO REMAIN SEPARATE
- ALL FLOOR WASTES, TUNDISHES AND OVERFLOW RELIEF GULLIES TO BE INSTALLED AS DOCUMENTED

11. ENERGY EFFICIENCY

- DWELLING TO COMPLY WITH NCC 2022 HP PART 13
- INSULATION, GLAZING AND SEALING TO BE INSTALLED IN ACCORDANCE WITH THE APPROVED ENERGY EFFICIENCY REPORT
- ANY CHANGES TO MATERIALS OR GLAZING MUST BE CHECKED AGAINST THE ENERGY ASSESSMENT

12. TERMITE MANAGEMENT

- TERMITE MANAGEMENT SYSTEM TO COMPLY WITH NCC 2022 HP PART 10.8
- SYSTEM SELECTION AND INSTALLATION TO FOLLOW MANUFACTURER REQUIREMENTS AND AUSTRALIAN STANDARDS

13. EXTERNAL WORKS, POOL & FENCING

- POOL CONSTRUCTION AND BARRIERS TO COMPLY WITH NCC 2022 HP PART 10.6 AND AS 1926.1
- POOL FENCING AND GATES TO BE SELF-CLOSING AND SELF-LATCHING
- FENCES AND RETAINING WALLS TO COMPLY WITH COUNCIL REQUIREMENTS AND ENGINEER CERTIFICATION WHERE REQUIRED


14. TOLERANCES & RESPONSIBILITY

- BUILDING TOLERANCES TO COMPLY WITH "GUIDE TO STANDARDS AND TOLERANCES"
- BUILDER TO VERIFY ALL SERVICE LOCATIONS PRIOR TO CONSTRUCTION
- THE DESIGNER ACCEPTS NO RESPONSIBILITY FOR WORK CARRIED OUT CONTRARY TO THESE DRAWINGS OR WITHOUT WRITTEN APPROVAL

DATE	DESCRIPTION	REV. NO.	DRAWING TITLE :		SCALE :	
03-02-2026	TECHNICAL UPDATES	H				
10-02-2026	TECHNICAL UPDATES	I				
18-02-2026	CONSTRUCTION REVIEW	J				
PILGRIM retains copyright in all documents and drawings and in any works executed from those documents and drawings. The PILGRIM reserves all present and future moral rights in all intellectual property in the designs, the documents, drawings and any works executed or to be executed from them. PILGRIM by agreement grants the client a license to use the documents and drawings to produce the project, for which they were intended, conditional upon the following: - the license applies only to the site or that part of the site to which the design relates. - PILGRIM has completed the particular stage or stages of design service for which PILGRIM has been commissioned. - fees properly due to the designer have been paid in full. Do not scale from drawings, verify all dimensions prior to commencement of construction or fabrication, notify the designer of any discrepancies.			GENERAL NOTES		MADELEINE & NICHOLAS CHILDS	
			106 HAROLD STREET, HOLLAND PARK		PILGRIM[®]	
					ABN: 89 639 943 187 QBCC: 1523 8743	
					DRAWN : TH	CHECK BY : CA
					DRAWING NO: A-00-07	
			DATE 18-02-2026		REV	J

SITE INFO

LOT NUMBER:	LOT 332
RP NUMBER:	RP 13252
SITE AREA:	404m ²
SITE COVER:	189m ²
TOTAL:	46.8%

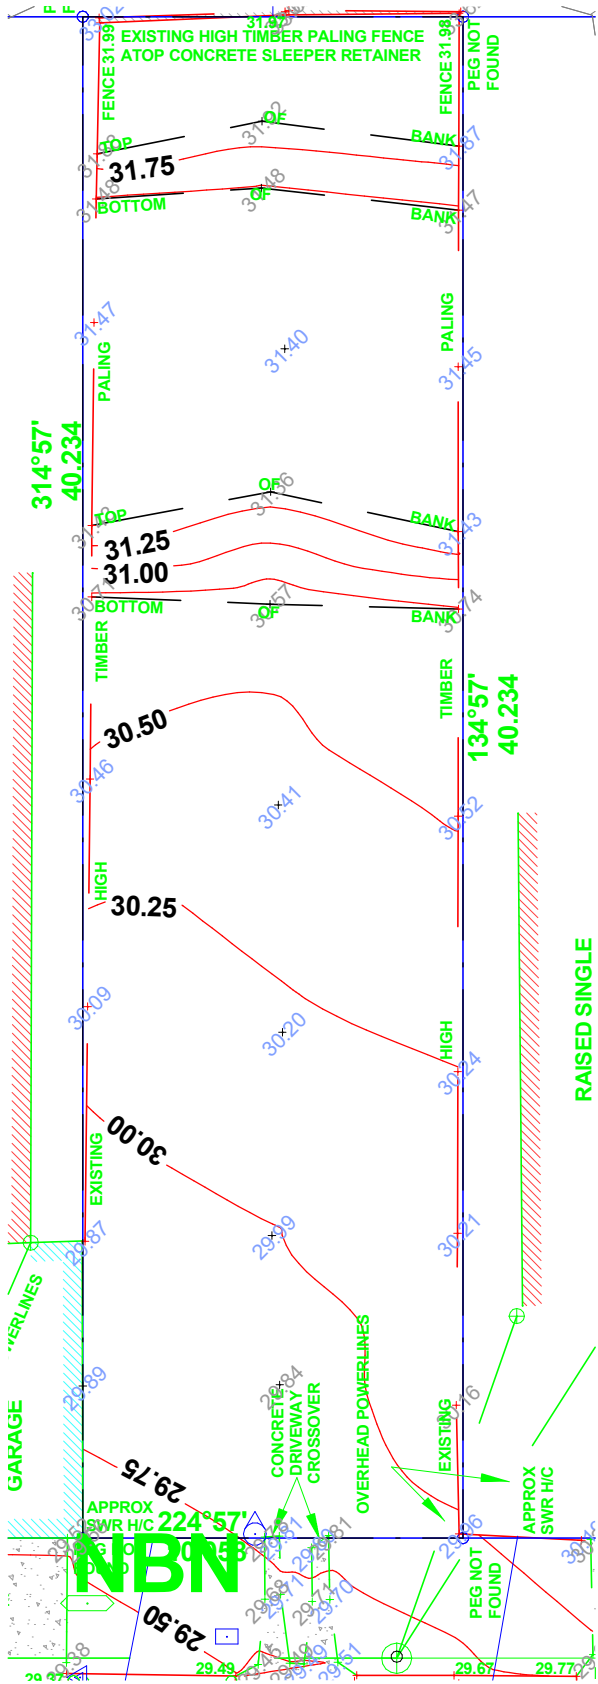


EXISTING SITE PLAN

1
A-03-01/ SCALE 1 : 200

PROPOSED SITE PLAN

2
A-03-01/ SCALE 1 : 200

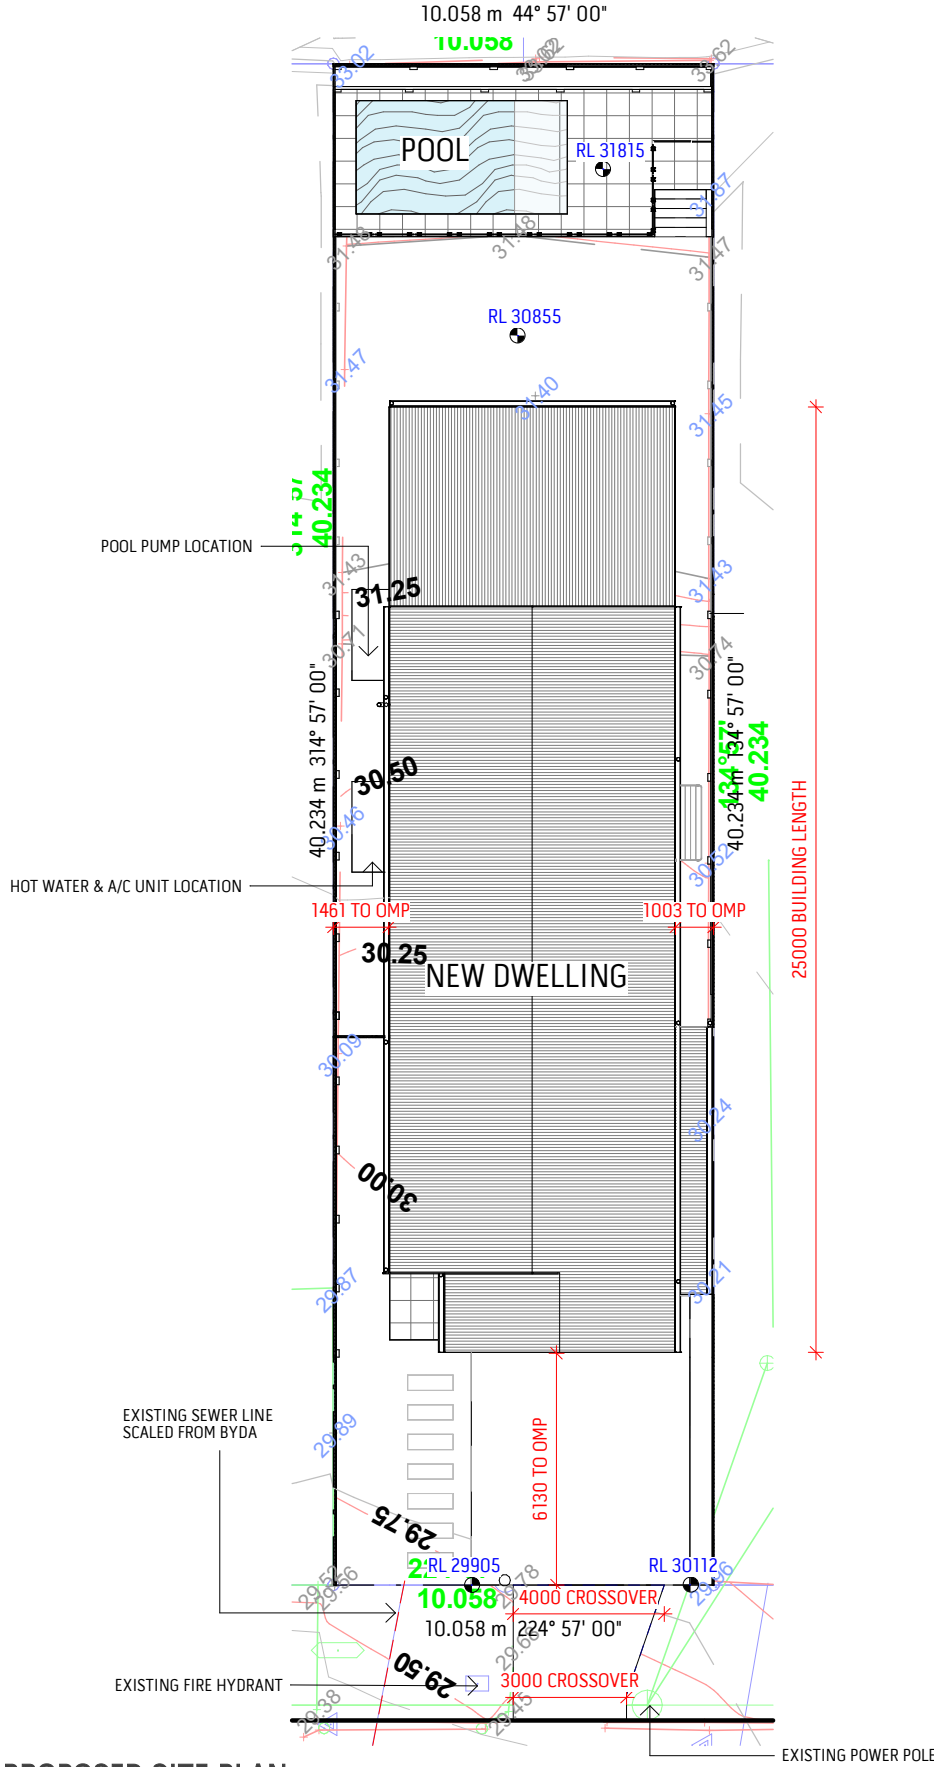


HAROLD STREET

DATE	DESCRIPTION	REV. NO.	DRAWING TITLE :	SCALE :
03-02-2026	TECHNICAL UPDATES	H	SITE PLAN	As indicated
10-02-2026	TECHNICAL UPDATES	I		
18-02-2026	CONSTRUCTION REVIEW	J		
PILGRIM retains copyright in all documents and drawings and in any works executed from those documents and drawings. The PILGRIM reserves all present and future moral rights in all intellectual property in the designs, the documents, drawings and any works executed or to be executed from them.				ABN: 89 639 943 187
PILGRIM by agreement grants the client a license to use the documents and drawings to produce the project, for which they were intended, conditional upon the following:				QBLCL: 1523 8743
- the license applies only to the site or that part of the site to which the design relates.				DRAWN : TH
- PILGRIM has completed the particular stage or stages of design service for which PILGRIM has been commissioned.				CHECK BY : CA
- fees properly due to the designer have been paid in full.				DRAWING NO: A-01-01
Do not scale from drawings, verify all dimensions prior to commencement of construction or fabrication, notify the designer of any discrepancies.				DATE 18-02-2026
				REV J

PAD AREAS

PATHWAY:	8.5m ²
GARAGE:	46m ²
LOWER PAD:	37m ²
UPPER PAD:	65m ²
DRIVEWAY:	44m ²
CROSSOVER:	12m ²
BATTER/FILL:	77m ²
YARD:	82m ²

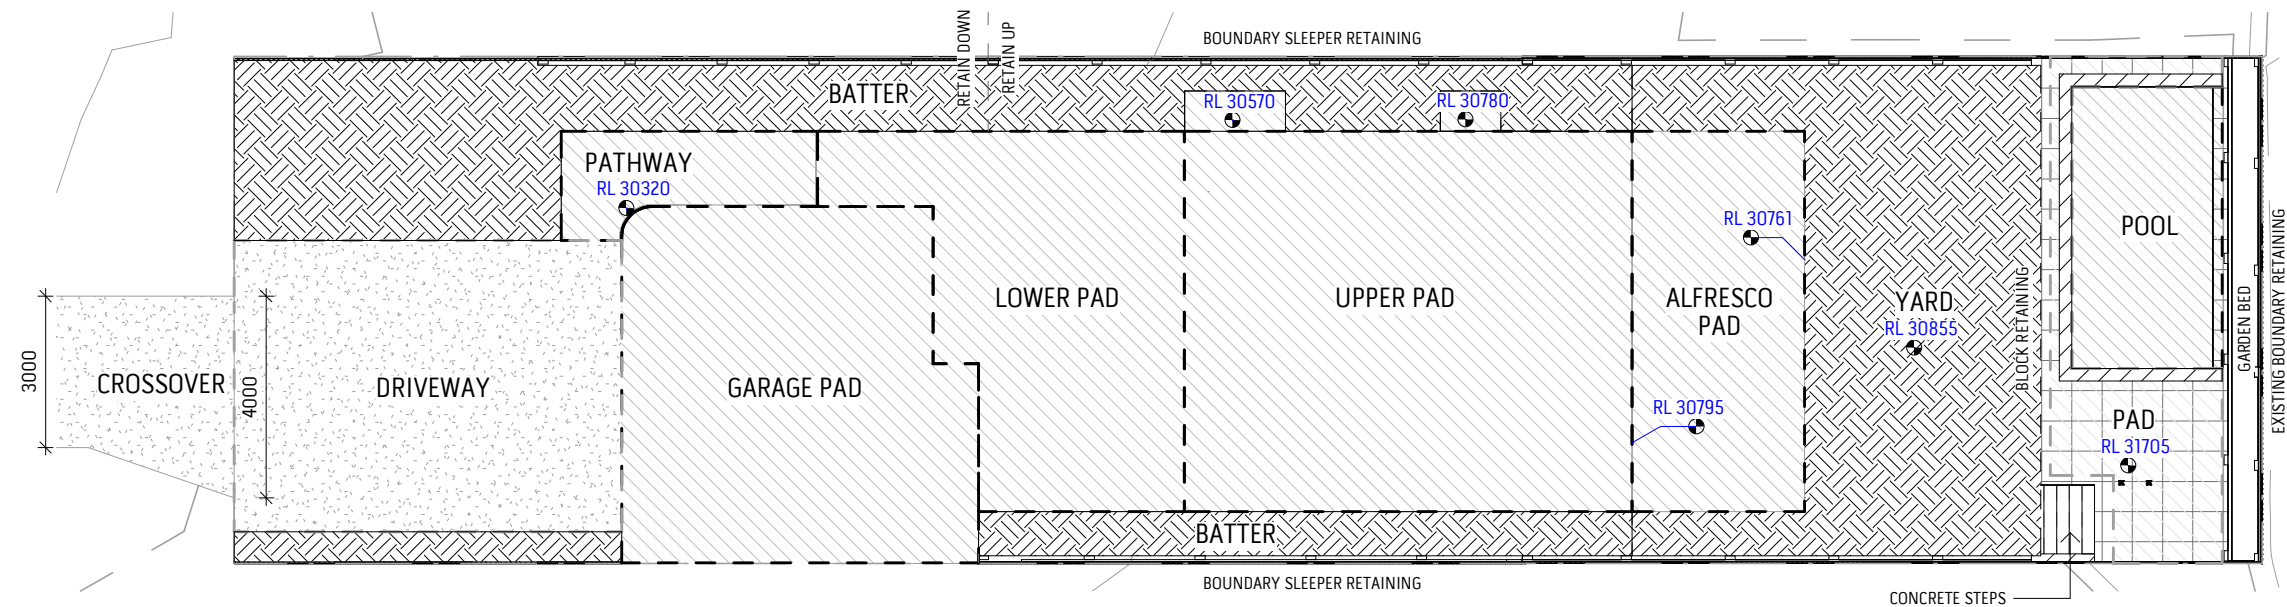

1
A-03-01/ EARTHWORKS PLAN
SCALE 1 : 150


SLAB/EARTHWORKS NOTES:

- ALL FOOTINGS AND SLABS TO BE CONSTRUCTED PER STRUCTURAL ENGINEER'S DRAWINGS
- VERIFY FINISHED FLOOR LEVELS (FFLs) ON SITE PRIOR TO POUR
- SLAB REBATES TO ALIGN WITH WINDOW, DOOR AND WET AREA REQUIREMENTS
- PLUMBING PENETRATIONS TO BE COORDINATED WITH PLUMBING CONTRACTOR PRIOR TO CONCRETE WORKS
- TERMITE PROTECTION SYSTEM TO BE INSTALLED AS PER NCC AND MANUFACTURE STANDARDS

DATE	DESCRIPTION	REV. NO.	DRAWING TITLE :		PILGRIM[®]	SCALE : As indicated					
03-02-2026	TECHNICAL UPDATES	H	EARTHWORKS PLAN			ABN:	89 639 943 187				
10-02-2026	TECHNICAL UPDATES	I				QBCC:	1523 8743				
18-02-2026	CONSTRUCTION REVIEW	J				DRAWN :	TH	CHECK BY :	CA		
PILGRIM retains copyright in all documents and drawings and in any works executed from those documents and drawings. The PILGRIM reserves all present and future moral rights in all intellectual property in the designs, the documents, drawings and any works executed or to be executed from them. PILGRIM by agreement grants the client a license to use the documents and drawings to produce the project, for which they were intended, conditional upon the following: - the license applies only to the site or that part of the site to which the design relates. - PILGRIM has completed the particular stage or stages of design service for which PILGRIM has been commissioned. - fees properly due to the designer have been paid in full. Do not scale from drawings, verify all dimensions prior to commencement of construction or fabrication, notify the designer of any discrepancies. <td colspan="2">106 HAROLD STREET, HOLLAND PARK</td> <td colspan="2">MADELEINE & NICHOLAS CHILDS</td> <td colspan="3">DRAWING NO: A-01-02</td>			106 HAROLD STREET, HOLLAND PARK		MADELEINE & NICHOLAS CHILDS		DRAWING NO: A-01-02				
						DATE	18-02-2026		REV	J	

LEGEND:

A/C	AIR CONDITIONING UNIT	HWU	HOT WATER UNIT
BA	BASIN	MB	METER BOX
BN	BIN LOCATION	MH	MANHOLE
CLY	CUTLERY LOCATION	NBW	NIB WALL (1200H)
CPB	CUPBOARD	OHC	OVERHEAD CUPBOARD
D	DRYER LOCATION	PL	POOL PUMP EQUIPMENT
DN	DOWN DIRECTION	REF.	REFRIGERATOR
DP	DOWN PIPE	SK	SINK
DW	DISHWASHER LOCATION	STK	PLUMBING STACK
FG	FIELD GULLY DRAIN	STR	STACKED TOWEL RAIL
FLG	FLUTED GLASS	TP	EXTERNAL TAP LOCATION
FW	FLOOR WASTE	WC	TOILET
HOB	HOB RECESS	WM	WASHING MACHINE

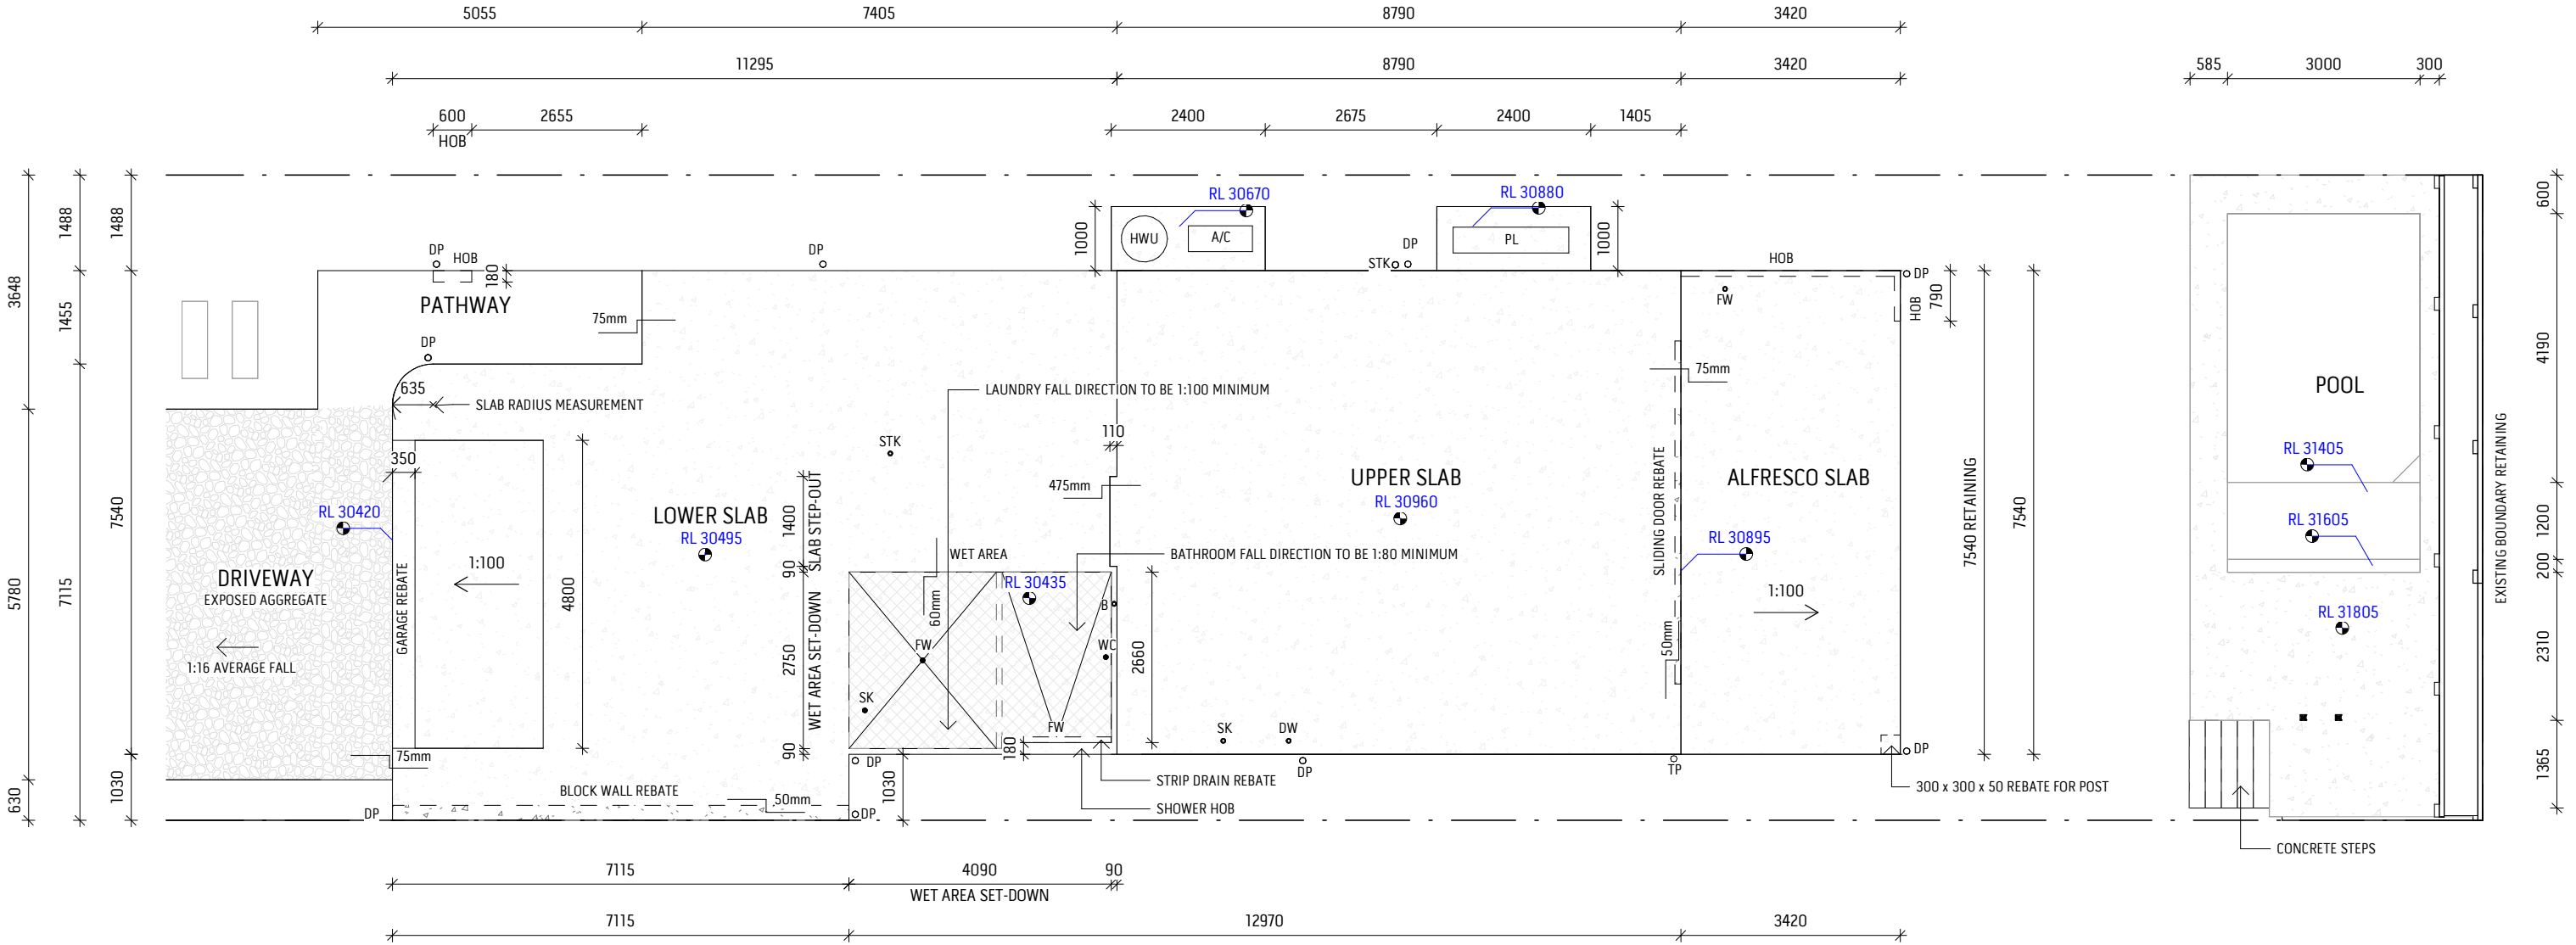

1
A-03-01/
SLAB SETOUT
SCALE 1 : 100


SLAB/EARTHWORKS NOTES:

- ALL FOOTINGS AND SLABS TO BE CONSTRUCTED PER STRUCTURAL ENGINEER'S DRAWINGS
- VERIFY FINISHED FLOOR LEVELS (FFLs) ON SITE PRIOR TO POUR
- SLAB REBATES TO ALIGN WITH WINDOW, DOOR AND WET AREA REQUIREMENTS
- PLUMBING PENETRATIONS TO BE COORDINATED WITH PLUMBING CONTRACTOR PRIOR TO CONCRETE WORKS
- TERMITE PROTECTION SYSTEM TO BE INSTALLED AS PER NCC AND MANUFACTURE STANDARDS

DATE		DESCRIPTION	REV. NO.	DRAWING TITLE :	MADELEINE & NICHOLAS CHILDS	PILGRIM [®]	SCALE :				
03-02-2026		TECHNICAL UPDATES	H				1 : 100				
10-02-2026		TECHNICAL UPDATES	I				ABN: 89 639 943 187				
18-02-2026		CONSTRUCTION REVIEW	J				QBCCL: 1523 8743				
PILGRIM retains copyright in all documents and drawings and in any works executed from those documents and drawings. The PILGRIM reserves all present and future moral rights in all intellectual property in the designs, the documents, drawings and any works executed or to be executed from them.				SLAB SETOUT	106 HAROLD STREET, HOLLAND PARK	DRAWN :		TH	CHECK BY :	CA	
PILGRIM by agreement grants the client a license to use the documents and drawings to produce the project, for which they were intended, conditional upon the following: - the license applies only to the site or that part of the site to which the design relates. - PILGRIM has completed the particular stage or stages of design service for which PILGRIM has been commissioned. - fees properly due to the designer have been paid in full. Do not scale from drawings, verify all dimensions prior to commencement of construction or fabrication, notify the designer of any discrepancies.						DRAWING NO:			A-01-03		
						DATE			18-02-2026	REV	J

LEGEND:

A/C	AIR CONDITIONING UNIT	HWU	HOT WATER UNIT
BA	BASIN	MB	METER BOX
BN	BIN LOCATION	MH	MANHOLE
CLY	CUTLERY LOCATION	NBW	NIB WALL (1200H)
CPB	CUPBOARD	OHC	OVERHEAD CUPBOARD
D	DRYER LOCATION	PL	POOL PUMP EQUIPMENT
DN	DOWN DIRECTION	REF.	REFRIGERATOR
DP	DOWN PIPE	SK	SINK
DW	DISHWASHER LOCATION	STK	PLUMBING STACK
FG	FIELD GULLY DRAIN	STR	STACKED TOWEL RAIL
FLG	FLUTED GLASS	TP	EXTERNAL TAP LOCATION
FW	FLOOR WASTE	WC	TOILET
HOB	HOB RECESS	WM	WASHING MACHINE

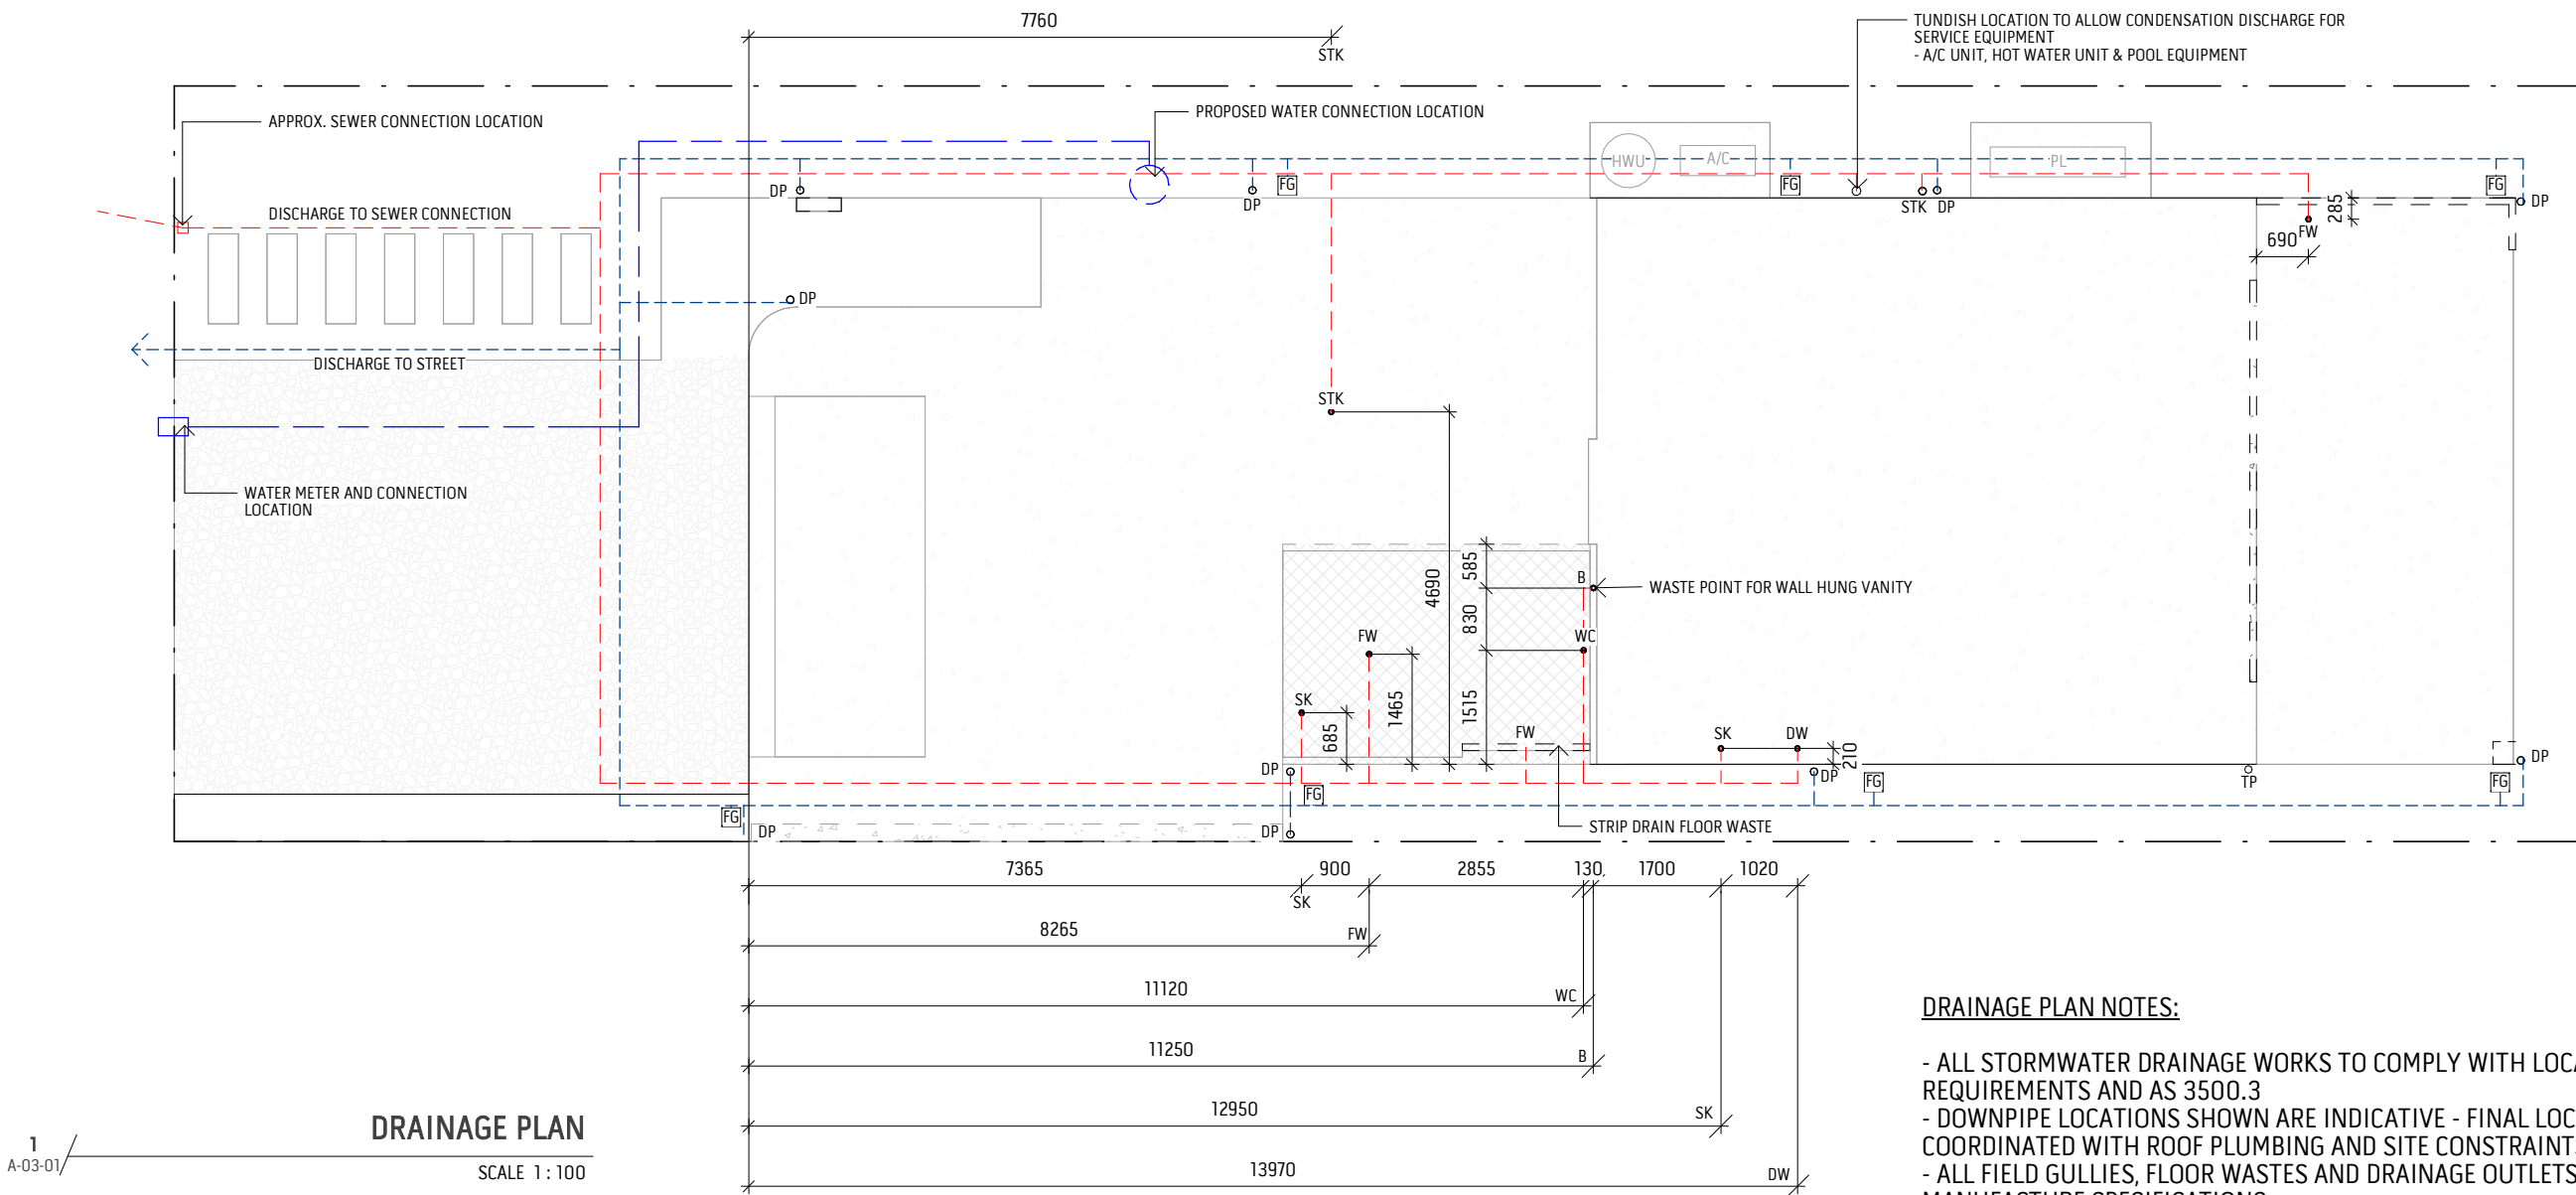


DRAINAGE PLAN NOTES:

- ALL STORMWATER DRAINAGE WORKS TO COMPLY WITH LOCAL COUNCIL REQUIREMENTS AND AS 3500.3
- DOWNPIPE LOCATIONS SHOWN ARE INDICATIVE - FINAL LOCATIONS TO BE COORDINATED WITH ROOF PLUMBING AND SITE CONSTRAINTS
- ALL FIELD GULLIES, FLOOR WASTES AND DRAINAGE OUTLETS TO BE INSTALLED PER MANUFACTURE SPECIFICATIONS
- ROOFWATER TO BE DIRECTED TO LEGAL POINT OF DISCHARGE AS NOMINATED BY COUNCIL
- ENSURE SEPARATION BETWEEN STORMWATER AND SEWER SYSTEMS IN ACCORDANCE WITH REGULATORY REQUIREMENTS

DATE	DESCRIPTION	REV. NO.	DRAWING TITLE :	SCALE :	1 : 100
03-02-2026	TECHNICAL UPDATES	H	DRAINAGE PLAN	ABN:	89 639 943 187
10-02-2026	TECHNICAL UPDATES	I		QBLCL:	1523 8743
18-02-2026	CONSTRUCTION REVIEW	J		DRAWN :	TH
PILGRIM retains copyright in all documents and drawings and in any works executed from those documents and drawings. The PILGRIM reserves all present and future moral rights in all intellectual property in the designs, the documents, drawings and any works executed or to be executed from them. PILGRIM by agreement grants the client a license to use the documents and drawings to produce the project, for which they were intended, conditional upon the following: - the license applies only to the site or that part of the site to which the design relates. - PILGRIM has completed the particular stage or stages of design service for which PILGRIM has been commissioned. - fees properly due to the designer have been paid in full. Do not scale from drawings, verify all dimensions prior to commencement of construction or fabrication, notify the designer of any discrepancies.				CHECK BY :	CA
106 HAROLD STREET, HOLLAND PARK				DRAWING NO.:	A-01-04
				DATE	18-02-2026
				REV	J


AREAS

GROUND LEVEL:	102m²
GARAGE:	44m²
ALFRESCO:	26m²
PORTICO:	5m²
	177m²
FIRST FLOOR:	124m²
BALCONY:	9.5m²
VOID:	6.5m²
	136m²
GRAND TOTAL:	317m²

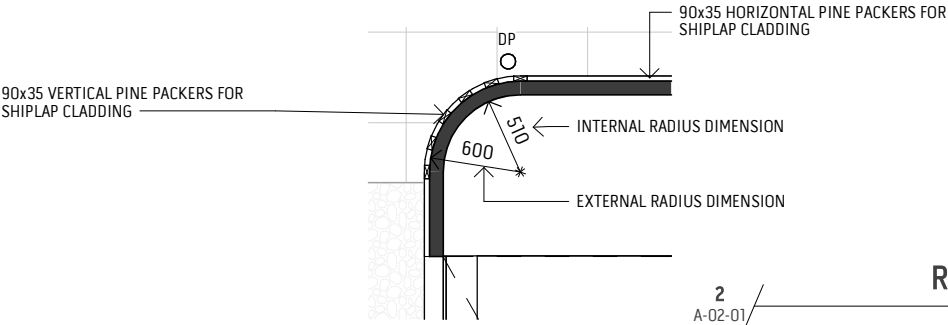

LEGEND:

A/C	AIR CONDITIONING UNIT	HWU	HOT WATER UNIT
BA	BASIN	MB	METER BOX
BN	BIN LOCATION	MH	MANHOLE
CLY	CUTLERY LOCATION	NBW	NIB WALL (1200H)
CPB	CUPBOARD	OHC	OVERHEAD CUPBOARD
D	DRYER LOCATION	PL	POOL PUMP EQUIPMENT
DN	DOWN DIRECTION	REF.	REFRIGERATOR
DP	DOWN PIPE	SK	SINK
DW	DISHWASHER LOCATION	STK	PLUMBING STACK
FG	FIELD GULLY DRAIN	STR	STACKED TOWEL RAIL
FLG	FLUTED GLASS	TP	EXTERNAL TAP LOCATION
FW	FLOOR WASTE	WC	TOILET
HOB	HOB RECESS	WM	WASHING MACHINE

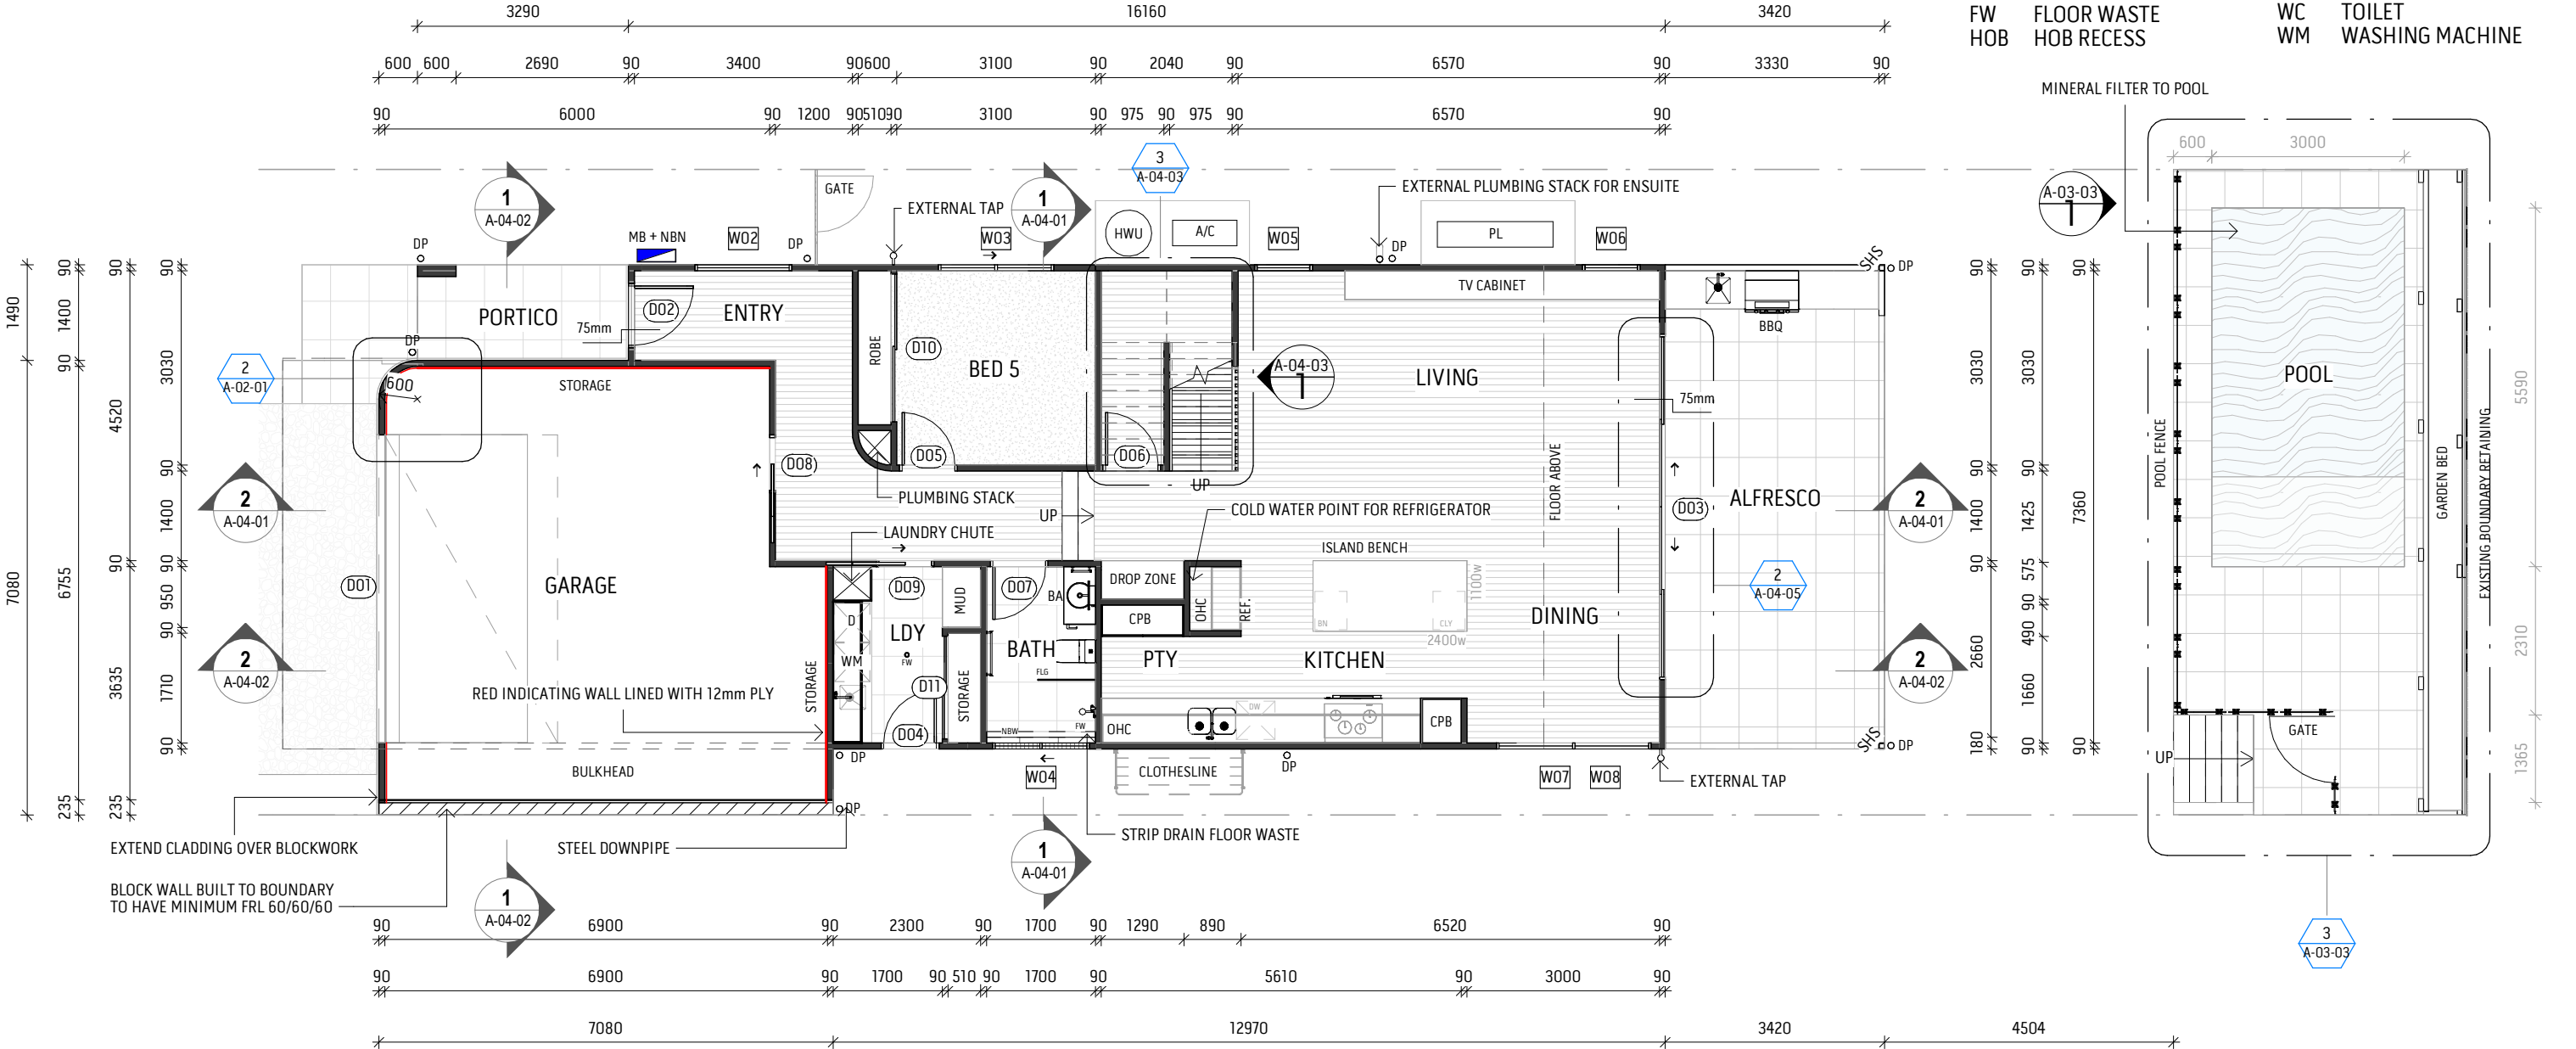

GROUND FLOOR PLAN

1
A-03-01
SCALE 1 : 100


FLOOR PLAN NOTES:

- ALL INTERNAL DIMENSIONS ARE SHOWN TO FRAMING/STRUCTURE UNLESS OTHERWISE NOTED
- CHECK DOOR SWINGS, CLEARANCES AND WINDOW HEIGHTS PRIOR TO FRAMING
- WET AREAS TO BE WATERPROOFED AS PER AS 3740
- STAIR CONSTRUCTION TO COMPLY WITH NCC VOLUME 2 - PART 11.2
- HANDRAILS AND BALUSTRADES TO COMPLY WITH NCC VOLUME 2 - PART 11.3
- ALL CABINETRY LAYOUTS TO BE CONFIRMED WITH JOINERY SHOP DRAWINGS

DATE		DESCRIPTION	REV. NO.	DRAWING TITLE :		PILGRIM[®]	SCALE :		As indicated		
03-02-2026		TECHNICAL UPDATES	H	GROUND FLOOR PLAN			ABN:		89 639 943 187		
10-02-2026		TECHNICAL UPDATES	I				QBCC:		1523 8743		
18-02-2026		CONSTRUCTION REVIEW	J	106 HAROLD STREET, HOLLAND PARK			DRAWN :		TH	CHECK BY :	CA
							DRAWING NO:		A-02-01		
PILGRIM retains copyright in all documents and drawings and in any works executed from those documents and drawings. The PILGRIM reserves all present and future moral rights in all intellectual property in the designs, the documents, drawings and any works executed or to be executed from them. PILGRIM by agreement grants the client a license to use the documents and drawings to produce the project, for which they were intended, conditional upon the following: - the license applies only to the site or that part of the site to which the design relates. - PILGRIM has completed the particular stage or stages of design service for which PILGRIM has been commissioned. - fees properly due to the designer have been paid in full. Do not scale from drawings, verify all dimensions prior to commencement of construction or fabrication, notify the designer of any discrepancies.						DATE		18-02-2026	REV	J	

AREAS

GROUND LEVEL:	102m²
GARAGE:	44m²
ALFRESCO:	26m²
PORTICO:	5m²
	177m²
FIRST FLOOR:	124m²
BALCONY:	9.5m²
VOID:	6.5m²
	136m²
GRAND TOTAL:	317m²

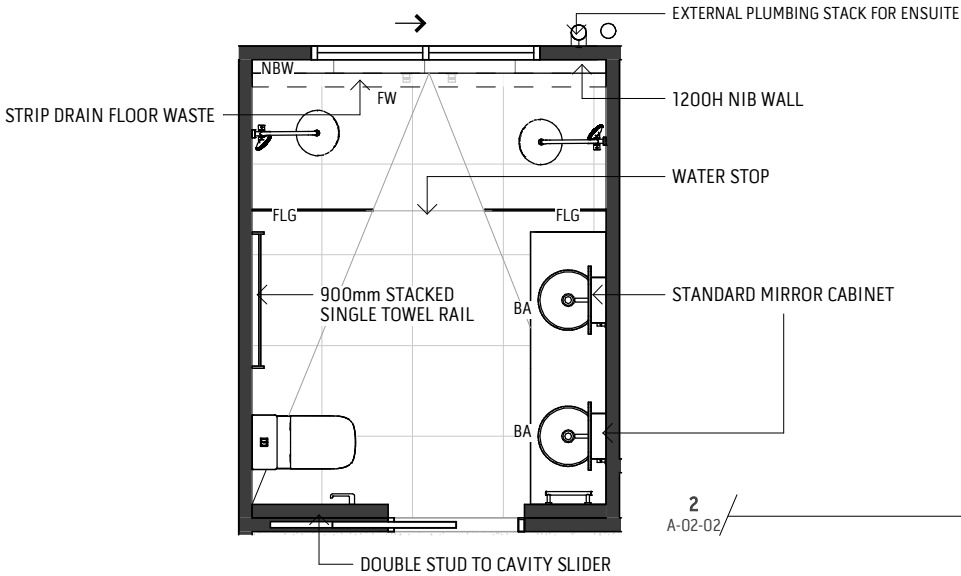


ENSUITE - CALLOUT

SCALE 1 : 50

LEGEND:

A/C	AIR CONDITIONING UNIT	HWU	HOT WATER UNIT
BA	BASIN	MB	METER BOX
BN	BIN LOCATION	MH	MANHOLE
CLY	CUTLERY LOCATION	NBW	NIB WALL (1200H)
CPB	CUPBOARD	OHC	OVERHEAD CUPBOARD
D	DRYER LOCATION	PL	POOL PUMP EQUIPMENT
DN	DOWN DIRECTION	REF.	REFRIGERATOR
DP	DOWN PIPE	SK	SINK
DW	DISHWASHER LOCATION	STK	PLUMBING STACK
FG	FIELD GULLY DRAIN	STR	STACKED TOWEL RAIL
FLG	FLUTED GLASS	TP	EXTERNAL TAP LOCATION
FW	FLOOR WASTE	WC	TOILET
HOB	HOB RECESS	WM	WASHING MACHINE

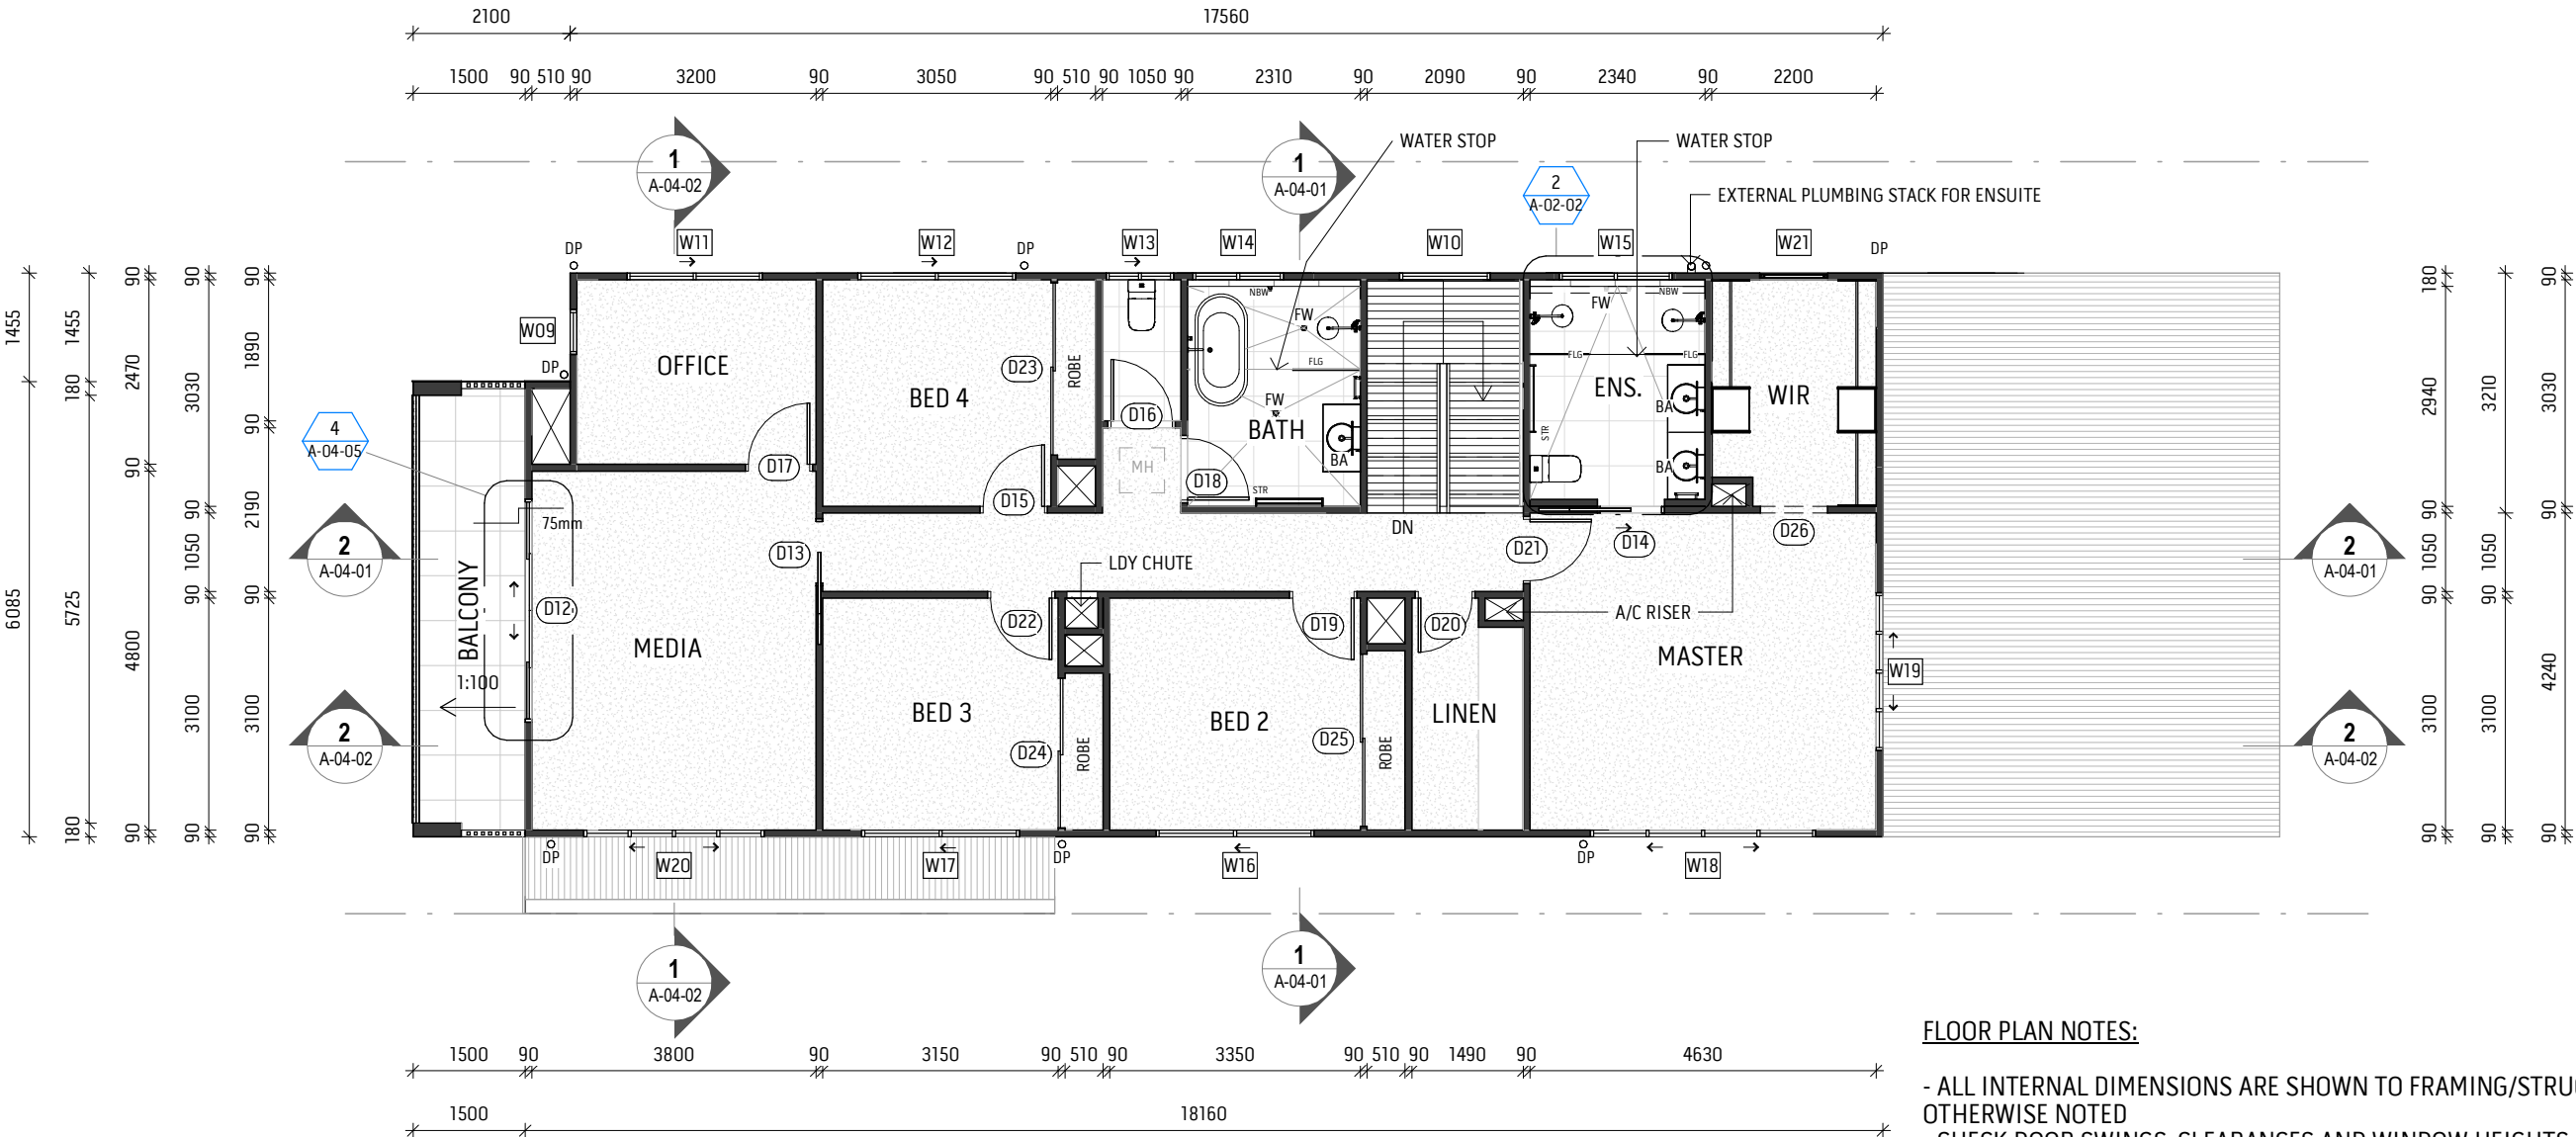

LEVEL 1 FLOOR PLAN

SCALE 1 : 100

FLOOR PLAN NOTES:

- ALL INTERNAL DIMENSIONS ARE SHOWN TO FRAMING/STRUCTURE UNLESS OTHERWISE NOTED
- CHECK DOOR SWINGS, CLEARANCES AND WINDOW HEIGHTS PRIOR TO FRAMING
- WET AREAS TO BE WATERPROOFED AS PER AS 3740
- STAIR CONSTRUCTION TO COMPLY WITH NCC VOLUME 2 - PART 11.2
- HANDRAILS AND BALUSTRADES TO COMPLY WITH NCC VOLUME 2 - PART 11.3
- ALL CABINERY LAYOUTS TO BE CONFIRMED WITH JOINERY SHOP DRAWINGS

DATE	DESCRIPTION	REV. NO.
03-02-2026	TECHNICAL UPDATES	H
10-02-2026	TECHNICAL UPDATES	I
18-02-2026	CONSTRUCTION REVIEW	J

PILGRIM retains copyright in all documents and drawings and in any works executed from those documents and drawings.
The PILGRIM reserves all present and future moral rights in all intellectual property in the designs, the documents, drawings and any works executed or to be executed from them.

PILGRIM by agreement grants the client a license to use the documents and drawings to produce the project, for which they were intended, conditional upon the following:

- the license applies only to the site or that part of the site to which the design relates.
- PILGRIM has completed the particular stage or stages of design service for which PILGRIM has been commissioned.
- fees properly due to the designer have been paid in full.

Do not scale from drawings, verify all dimensions prior to commencement of construction or fabrication, notify the designer of any discrepancies.

DRAWING TITLE :

LEVEL 1 FLOOR PLAN

MADELEINE & NICHOLAS CHILDS


106 HAROLD STREET, HOLLAND PARK

PILGRIM®

SCALE :	As indicated
ABN:	89 639 943 187
QBCCL:	1523 8743
DRAWN :	TH
CHECK BY :	CA
DRAWING NO:	A-02-02
DATE	18-02-2026
REV	J

LEGEND:


A/C	AIR CONDITIONING UNIT	HWU	HOT WATER UNIT
BA	BASIN	MB	METER BOX
BN	BIN LOCATION	MH	MANHOLE
CLY	CUTLERY LOCATION	NBW	NIB WALL (1200H)
CPB	CUPBOARD	OHC	OVERHEAD CUPBOARD
D	DRYER LOCATION	PL	POOL PUMP EQUIPMENT
DN	DOWN DIRECTION	REF.	REFRIGERATOR
DP	DOWN PIPE	SK	SINK
DW	DISHWASHER LOCATION	STK	PLUMBING STACK
FG	FIELD GULLY DRAIN	STR	STACKED TOWEL RAIL
FLG	FLUTED GLASS	TP	EXTERNAL TAP LOCATION
FW	FLOOR WASTE	WC	TOILET
HOB	HOB RECESS	WM	WASHING MACHINE

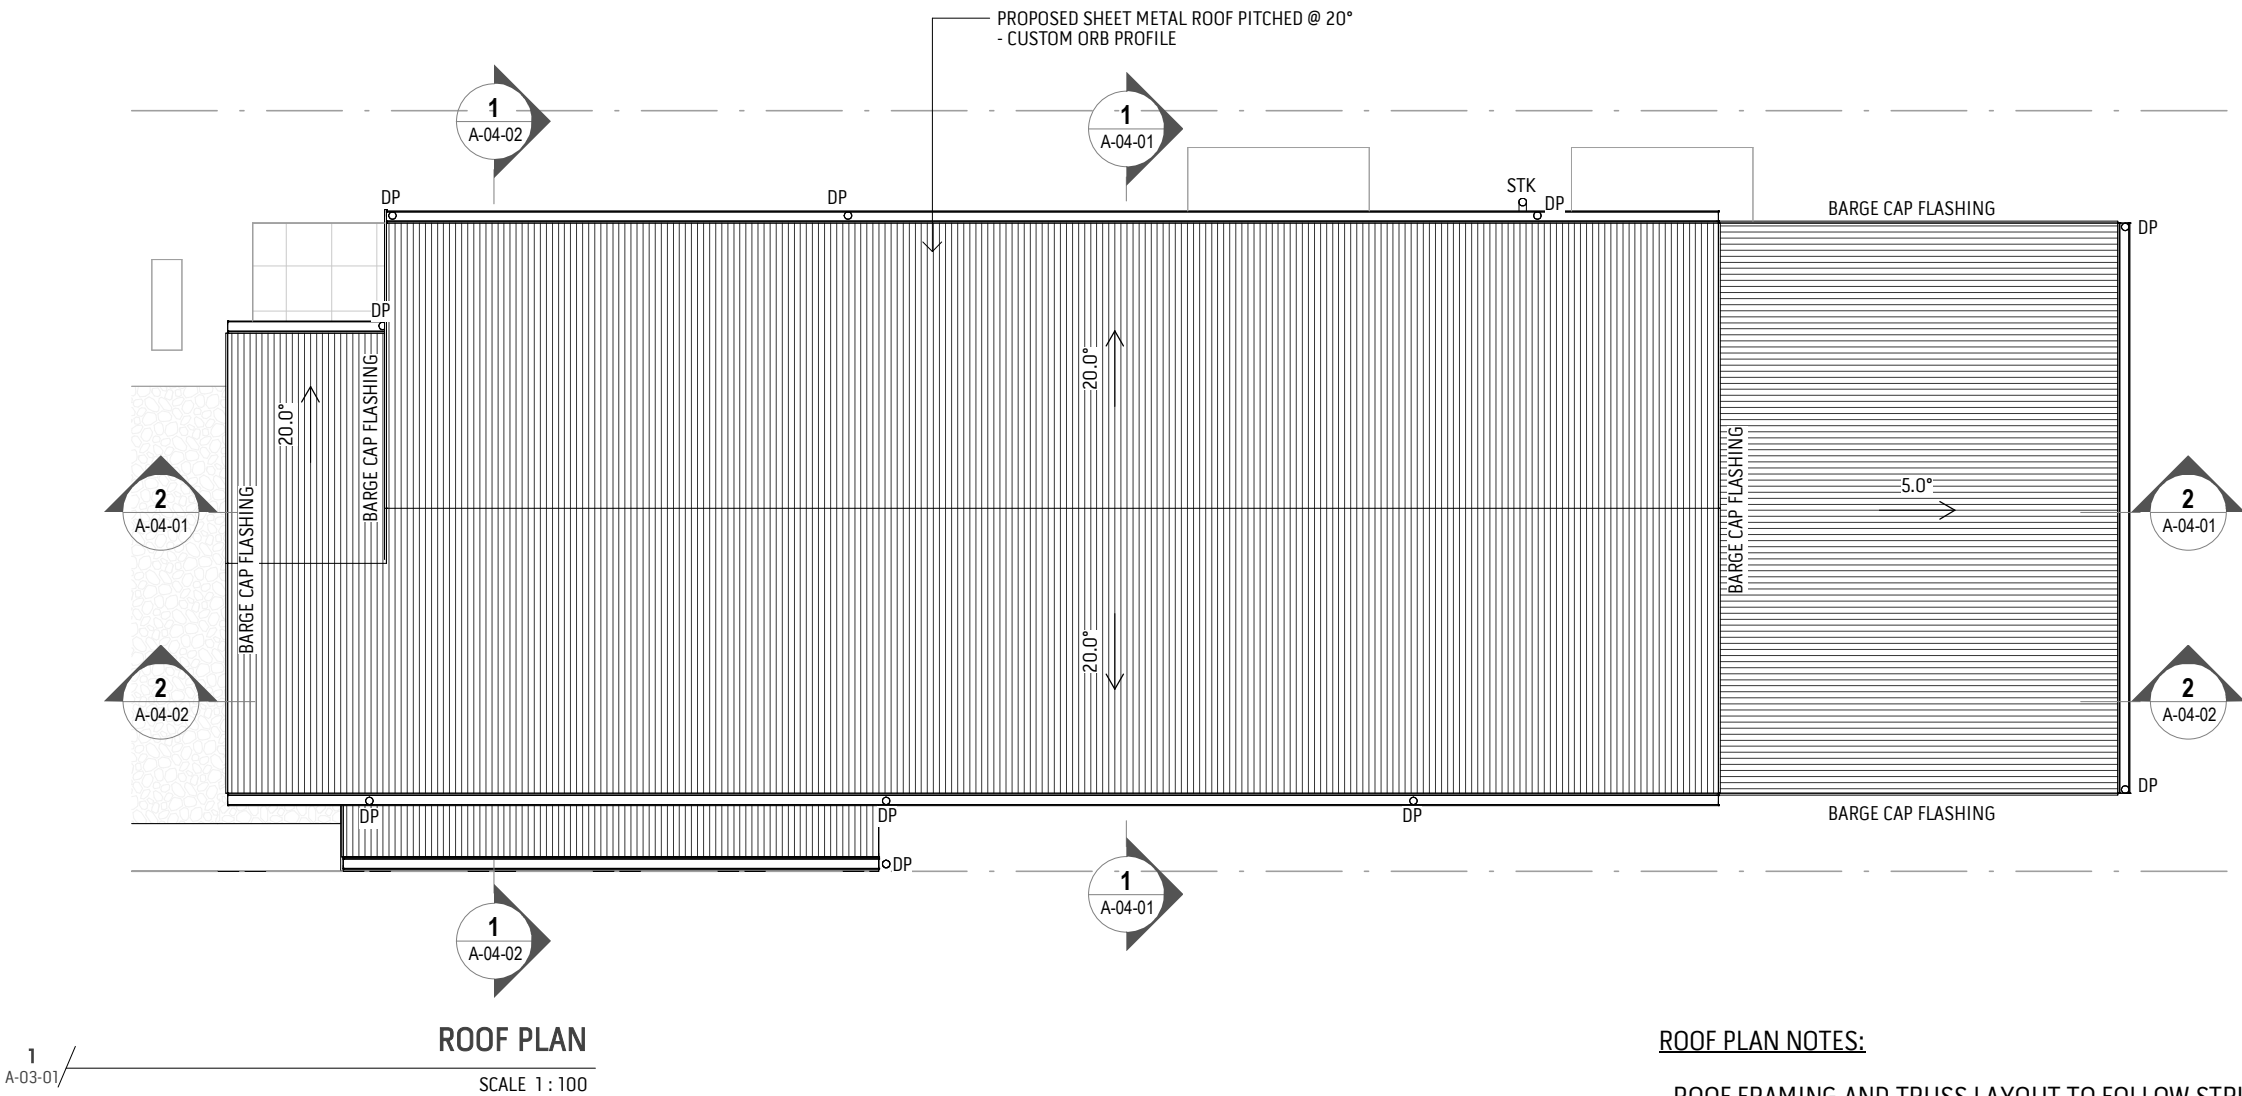

ROOF PLAN NOTES:

- ROOF FRAMING AND TRUSS LAYOUT TO FOLLOW STRUCTURAL ENGINEER'S DOCUMENTS
- PROVIDE COMPLIANT SARKING, INSULATION AND TIE-DOWNS
- ROOF PITCH AND DIRECTION TO BE CONFIRMED WITH TRUSS MANUFACTURER
- FLASHING, GUTTERS AND DOWNPIPES TO COMPLY WITH AS 3500.3 - DOWNPIPES CONNECTED TO LAWFUL POINT OF DISCHARGE

DATE	DESCRIPTION	REV. NO.	DRAWING TITLE :		SCALE :				
03-02-2026	TECHNICAL UPDATES	H	ROOF PLAN	MADELEINE & NICHOLAS CHILDS	1 : 100				
10-02-2026	TECHNICAL UPDATES	I			ABN: 89 639 943 187				
18-02-2026	CONSTRUCTION REVIEW	J			QBCC: 1523 8743				
PILGRIM retains copyright in all documents and drawings and in any works executed from those documents and drawings. The PILGRIM reserves all present and future moral rights in all intellectual property in the designs, the documents, drawings and any works executed or to be executed from them.			106 HAROLD STREET, HOLLAND PARK						
PILGRIM by agreement grants the client a license to use the documents and drawings to produce the project, for which they were intended, conditional upon the following: - the license applies only to the site or that part of the site to which the design relates. - PILGRIM has completed the particular stage or stages of design service for which PILGRIM has been commissioned. - fees properly due to the designer have been paid in full. Do not scale from drawings, verify all dimensions prior to commencement of construction or fabrication, notify the designer of any discrepancies.									
					DRAWN :	TH	CHECK BY :	CA	
					DRAWING NO:	A-02-03			
					DATE	18-02-2026		REV	J

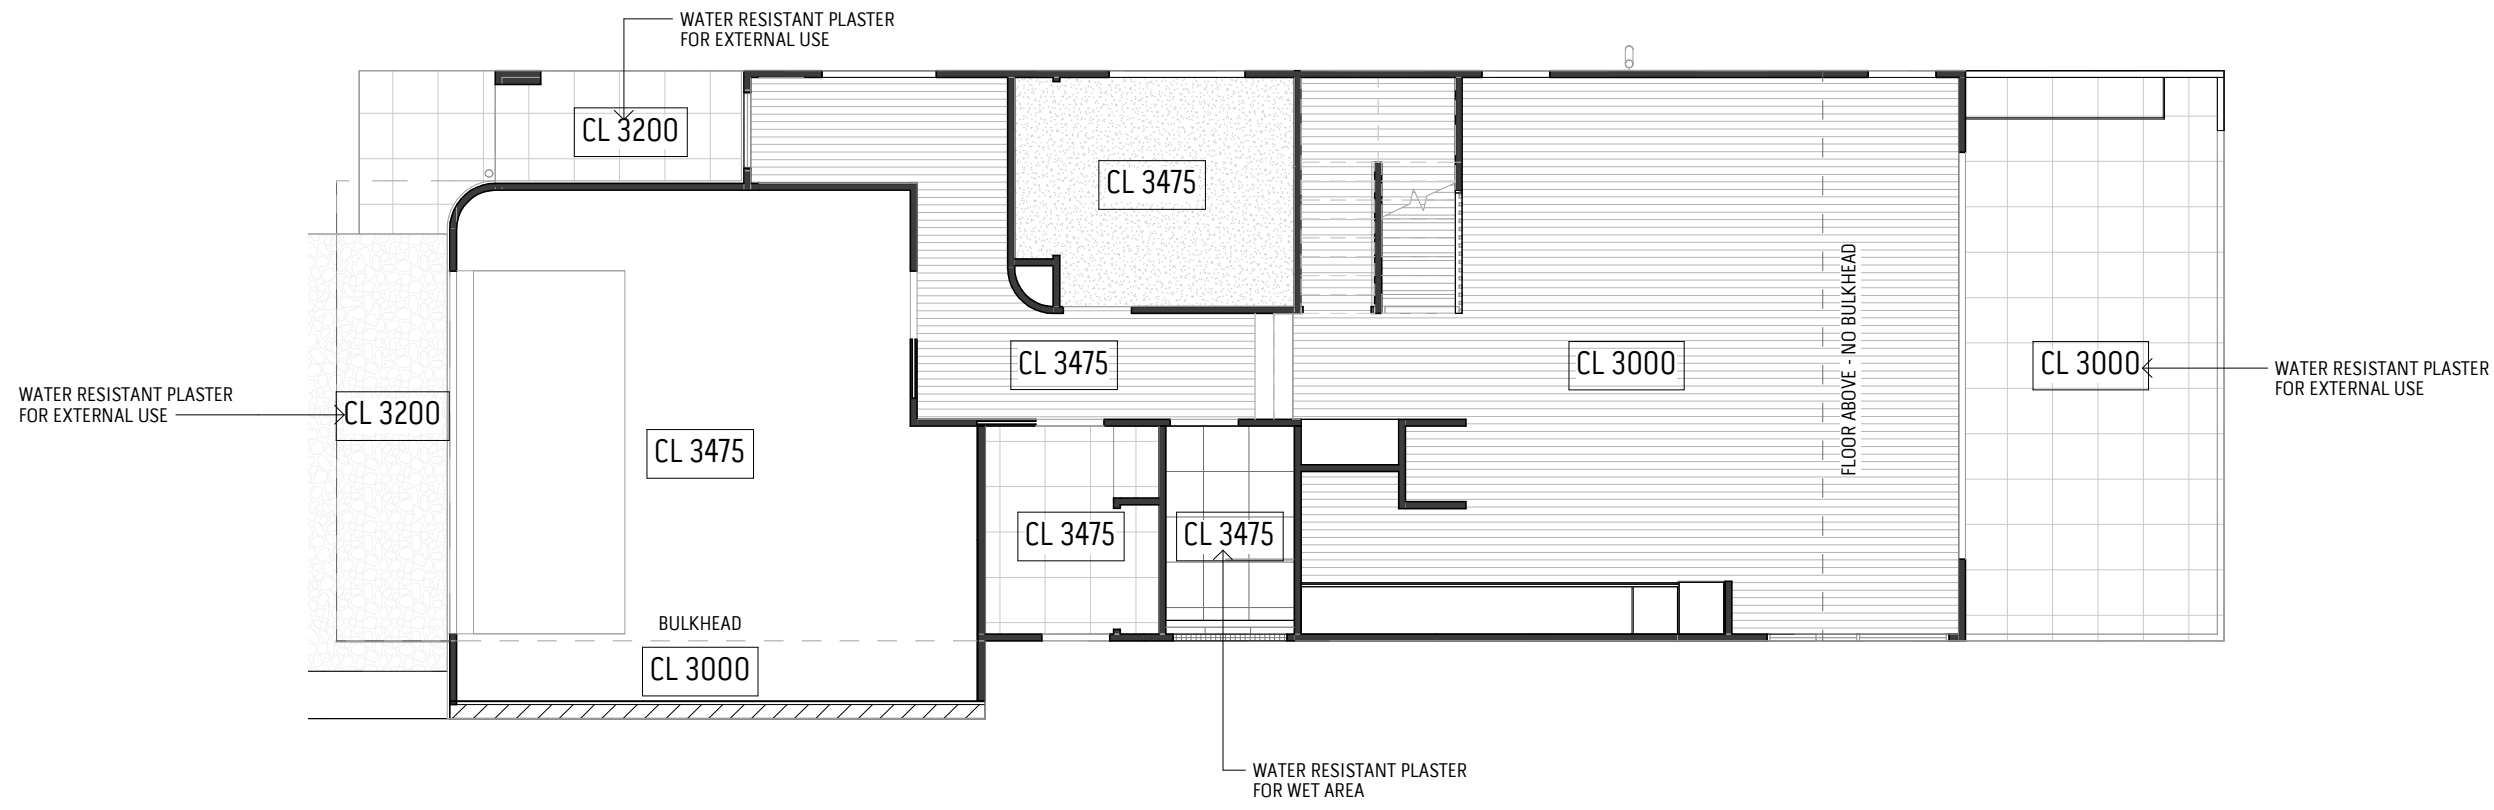


1
A-03-01/

GROUND FLOOR CEILING PLAN

SCALE 1 : 100

- CEILING PLAN NOTES:**
- CEILING HEIGHTS ARE REFERENCED FROM THE FFL OF EACH LEVEL
 - CEILING HEIGHTS ARE TO BE VERIFIED ON SITE PRIOR TO FRAMING OR PLASTER INSTALLATION
 - STANDARD CEILING ALLOWANCE FROM PLATE HEIGHT INCLUDES 30mm CEILING BATTENS AND 10mm LINING
 - BULKHEAD LOCATIONS AND DIMENSIONS ARE INDICATIVE - CONFIRM WITH MECHANICAL, ELECTRICAL AND CABINETRY LAYOUTS
 - FOR INSULATION INSTALLATION, ENSURE CONTINUOUS ACROSS ENTIRE CEILING SPACE, EXCLUDING DOWNLIGHT SAFETY CLEARANCES
 - REFER TO ELECTRICAL PLANS FOR LOCATIONS OF CEILING FAN, DOWNLIGHT AND OTHER ELECTRICAL FIXTURES MOUNTED ON CEILING

DATE	DESCRIPTION	REV. NO.	DRAWING TITLE :	MADELEINE & NICHOLAS CHILDS	PILGRIM®	SCALE : 1 : 100			
03-02-2026	TECHNICAL UPDATES	H				ABN: 89 639 943 187			
10-02-2026	TECHNICAL UPDATES	I				QBCC: 1523 8743			
18-02-2026	CONSTRUCTION REVIEW	J				DRAWN : TH CHECK BY : CA			
PILGRIM retains copyright in all documents and drawings and in any works executed from those documents and drawings. The PILGRIM reserves all present and future moral rights in all intellectual property in the designs, the documents, drawings and any works executed or to be executed from them.			GROUND CEILING PLAN	106 HAROLD STREET, HOLLAND PARK	DRAWING NO: A-02-04	DATE 18-02-2026		REV	J
PILGRIM by agreement grants the client a license to use the documents and drawings to produce the project, for which they were intended, conditional upon the following: - the license applies only to the site or that part of the site to which the design relates. - PILGRIM has completed the particular stage or stages of design service for which PILGRIM has been commissioned. - fees properly due to the designer have been paid in full. Do not scale from drawings, verify all dimensions prior to commencement of construction or fabrication, notify the designer of any discrepancies.									

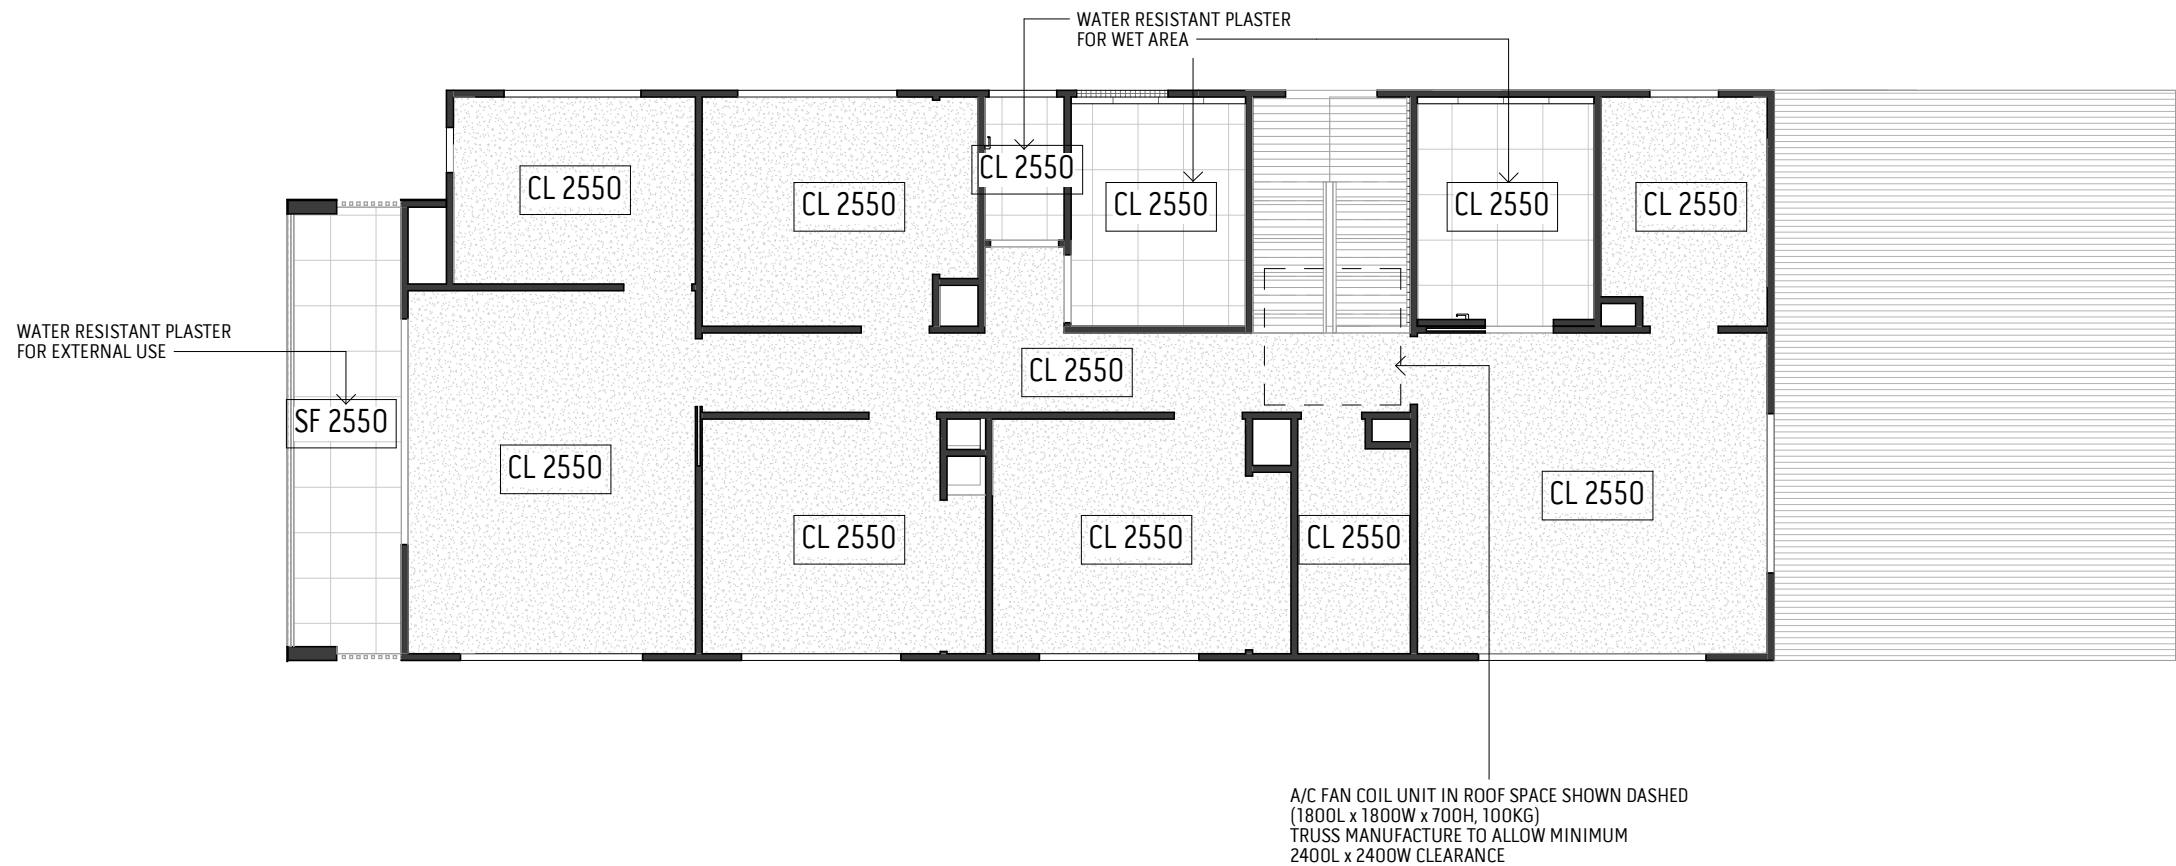



1
A-03-01 / **LEVEL 1 CEILING PLAN**
SCALE 1 : 100

- CEILING PLAN NOTES:**
- CEILING HEIGHTS ARE REFERENCED FROM THE FFL OF EACH LEVEL
 - CEILING HEIGHTS ARE TO BE VERIFIED ON SITE PRIOR TO FRAMING OR PLASTER INSTALLATION
 - STANDARD CEILING ALLOWANCE FROM PLATE HEIGHT INCLUDES 30mm CEILING BATTENS AND 10mm LINING
 - BULKHEAD LOCATIONS AND DIMENSIONS ARE INDICATIVE - CONFIRM WITH MECHANICAL, ELECTRICAL AND CABINETRY LAYOUTS
 - FOR INSULATION INSTALLATION, ENSURE CONTINUOUS ACROSS ENTIRE CEILING SPACE, EXCLUDING DOWNLIGHT SAFETY CLEARANCES
 - REFER TO ELECTRICAL PLANS FOR LOCATIONS OF CEILING FAN, DOWNLIGHT AND OTHER ELECTRICAL FIXTURES MOUNTED ON CEILING

DATE		DESCRIPTION	REV. NO.	DRAWING TITLE :		SCALE :	
03-02-2026	TECHNICAL UPDATES		H	LEVEL 1 CEILING PLAN	MADELEINE & NICHOLAS CHILDS	1 : 100	
10-02-2026	TECHNICAL UPDATES		I			ABN: 89 639 943 187 QBCC: 1523 8743	
18-02-2026	CONSTRUCTION REVIEW		J			DRAWN : TH CHECK BY : CA	
PILGRIM retains copyright in all documents and drawings and in any works executed from those documents and drawings. The PILGRIM reserves all present and future moral rights in all intellectual property in the designs, the documents, drawings and any works executed or to be executed from them. PILGRIM by agreement grants the client a license to use the documents and drawings to produce the project, for which they were intended, conditional upon the following: - the license applies only to the site or that part of the site to which the design relates. - PILGRIM has completed the particular stage or stages of design service for which PILGRIM has been commissioned. - fees properly due to the designer have been paid in full. Do not scale from drawings, verify all dimensions prior to commencement of construction or fabrication, notify the designer of any discrepancies.				DRAWING NO: A-02-05		DATE 18-02-2026	
				106 HAROLD STREET, HOLLAND PARK		REV J	
				PILGRIM [®]			

ELEVATION PLAN NOTES:

- ALL EXTERNAL WALL FINISHES AND MATERIALS TO BE INSTALLED PER MANUFACTURE INSTRUCTIONS
- ROOF PITCH, FLASHING AND GUTTERING TO COMPLY WITH AS 3500.3 AND ROOFING MANUFACTURE REQUIREMENTS
- EXTERNAL CLADDING JUNCTIONS TO BE SEALED TO MANUFACTURE SPECIFICATIONS
- GLAZING PERFORMANCE TO COMPLY WITH ENERGY REPORT

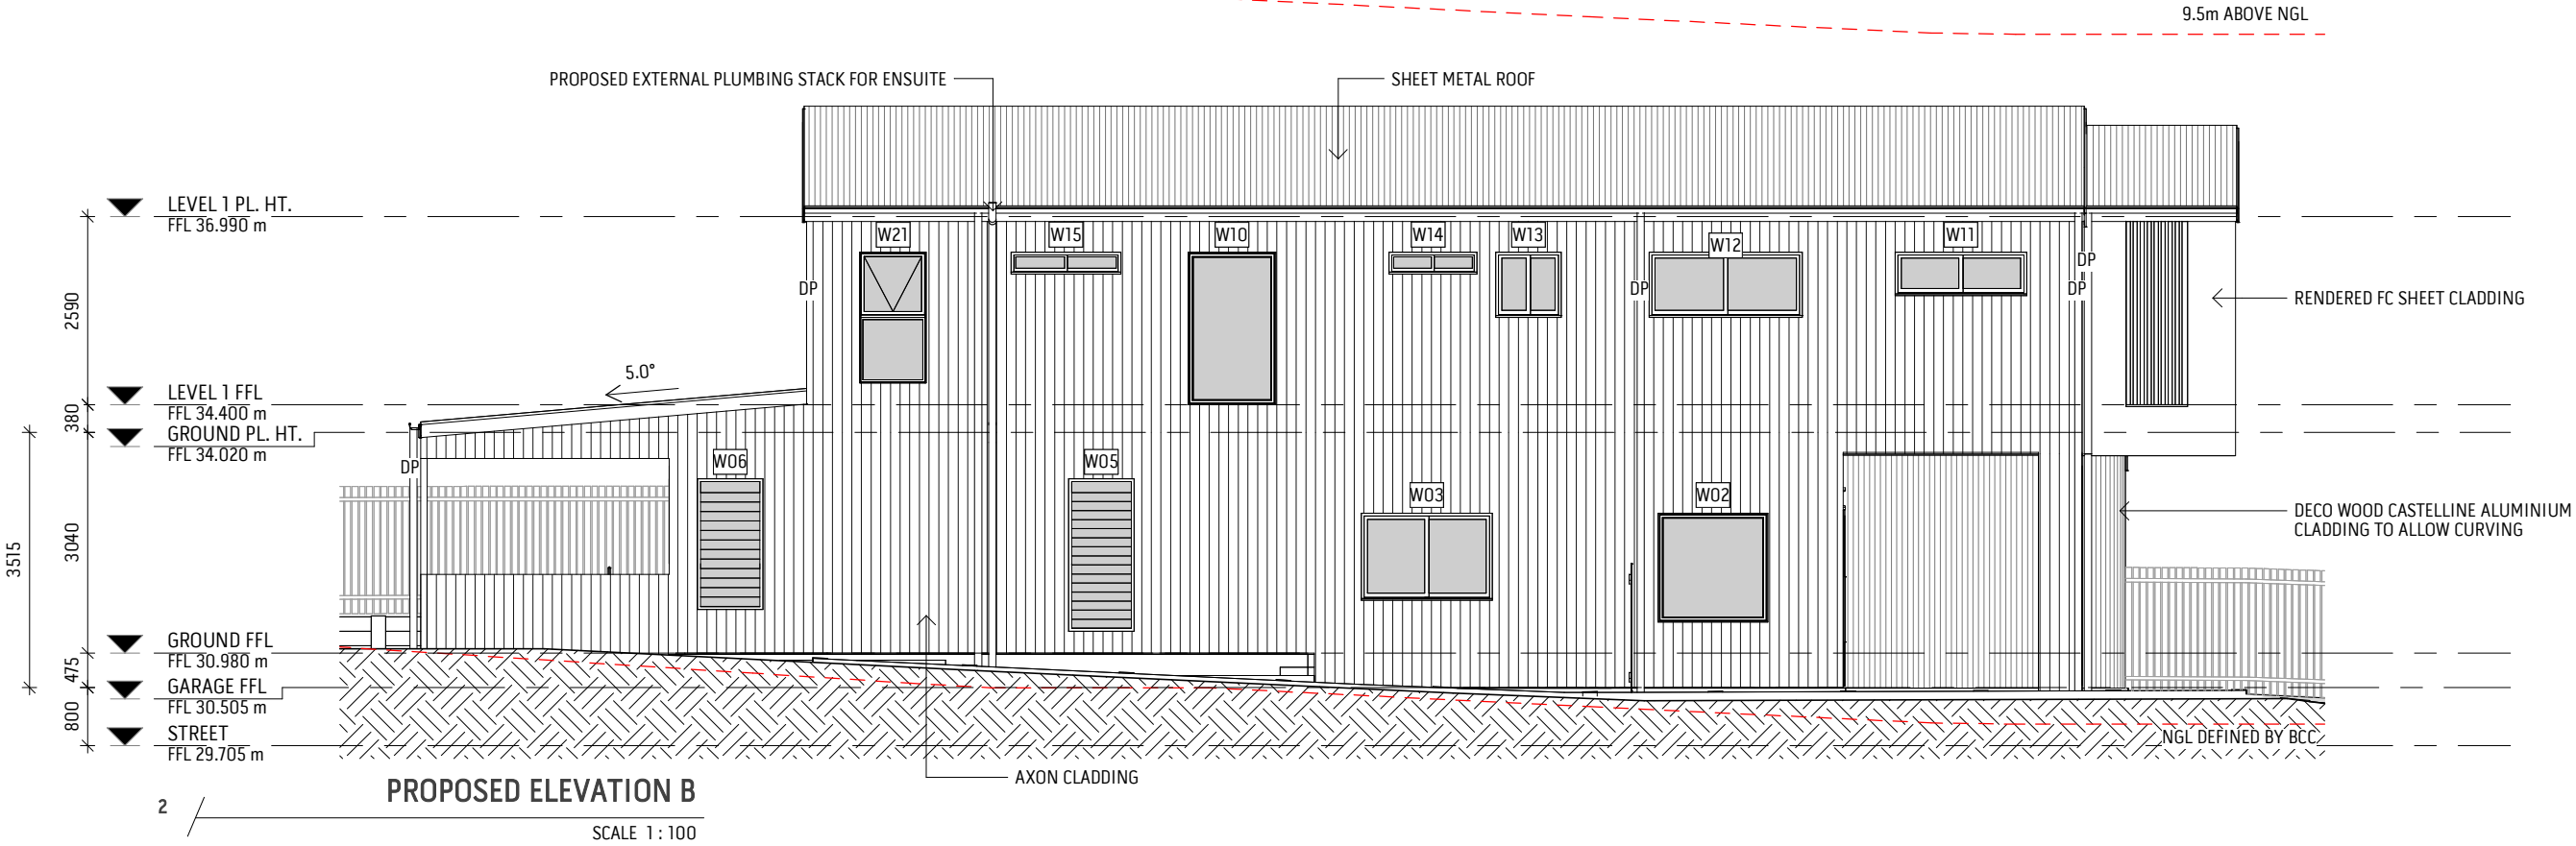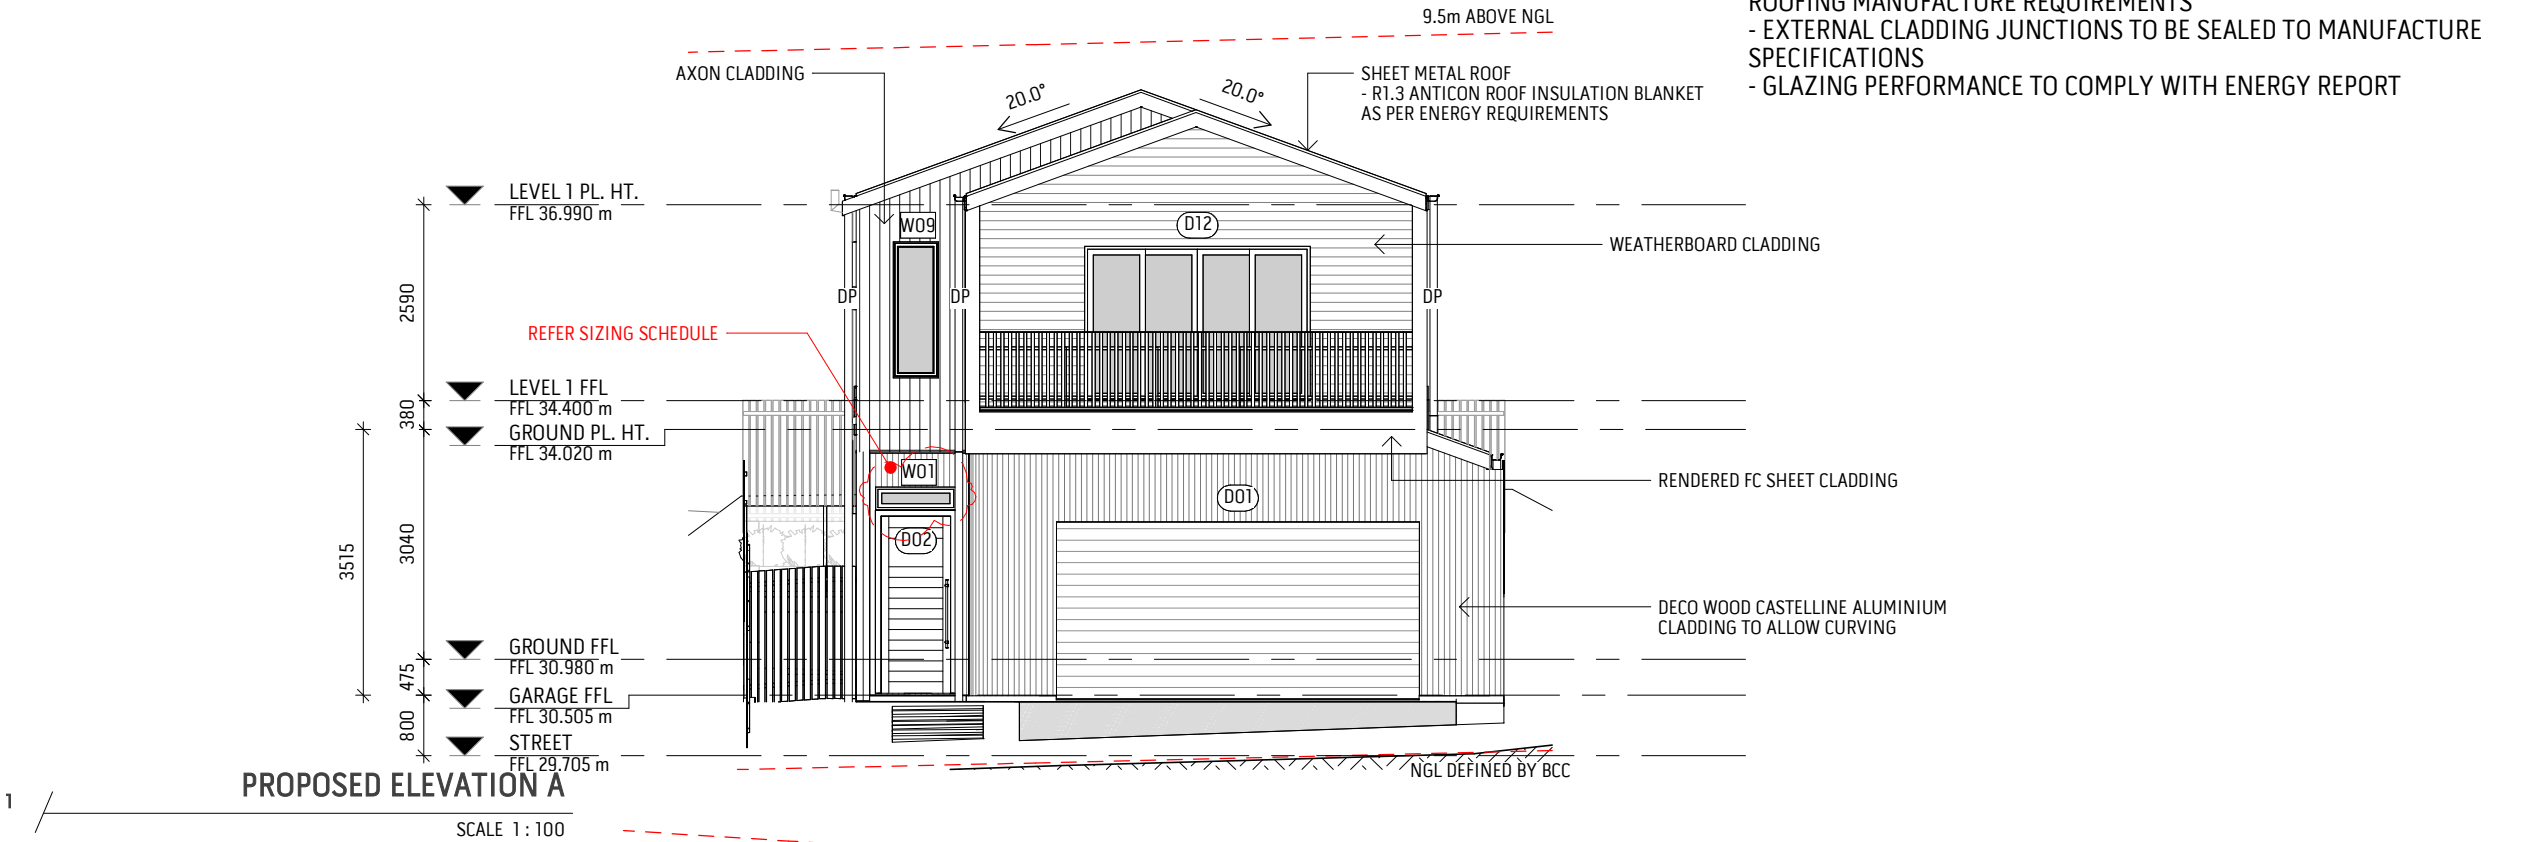

DATE	DESCRIPTION	REV. NO.
03-02-2026	TECHNICAL UPDATES	H
10-02-2026	TECHNICAL UPDATES	I
18-02-2026	CONSTRUCTION REVIEW	J

PILGRIM retains copyright in all documents and drawings and in any works executed from those documents and drawings. The PILGRIM reserves all present and future moral rights in all intellectual property in the designs, the documents, drawings and any works executed or to be executed from them.

PILGRIM by agreement grants the client a license to use the documents and drawings to produce the project, for which they were intended, conditional upon the following:

- the license applies only to the site or that part of the site to which the design relates.
- PILGRIM has completed the particular stage or stages of design service for which PILGRIM has been commissioned.
- fees properly due to the designer have been paid in full.


Do not scale from drawings, verify all dimensions prior to commencement of construction or fabrication, notify the designer of any discrepancies.

DRAWING TITLE :	MADELEINE & NICHOLAS CHILDS
PROPOSED ELEVATIONS	
106 HAROLD STREET, HOLLAND PARK	

SCALE :	1 : 100
ABN:	89 639 943 187
QBLCL:	1523 8743
DRAWN :	TH
CHECK BY :	CA
DRAWING NO:	A-03-01
DATE	18-02-2026
REV	J

ELEVATION PLAN NOTES:

- ALL EXTERNAL WALL FINISHES AND MATERIALS TO BE INSTALLED PER MANUFACTURE INSTRUCTIONS
- ROOF PITCH, FLASHING AND GUTTERING TO COMPLY WITH AS 3500.3 AND ROOFING MANUFACTURE REQUIREMENTS
- EXTERNAL CLADDING JUNCTIONS TO BE SEALED TO MANUFACTURE SPECIFICATIONS
- GLAZING PERFORMANCE TO COMPLY WITH ENERGY REPORT

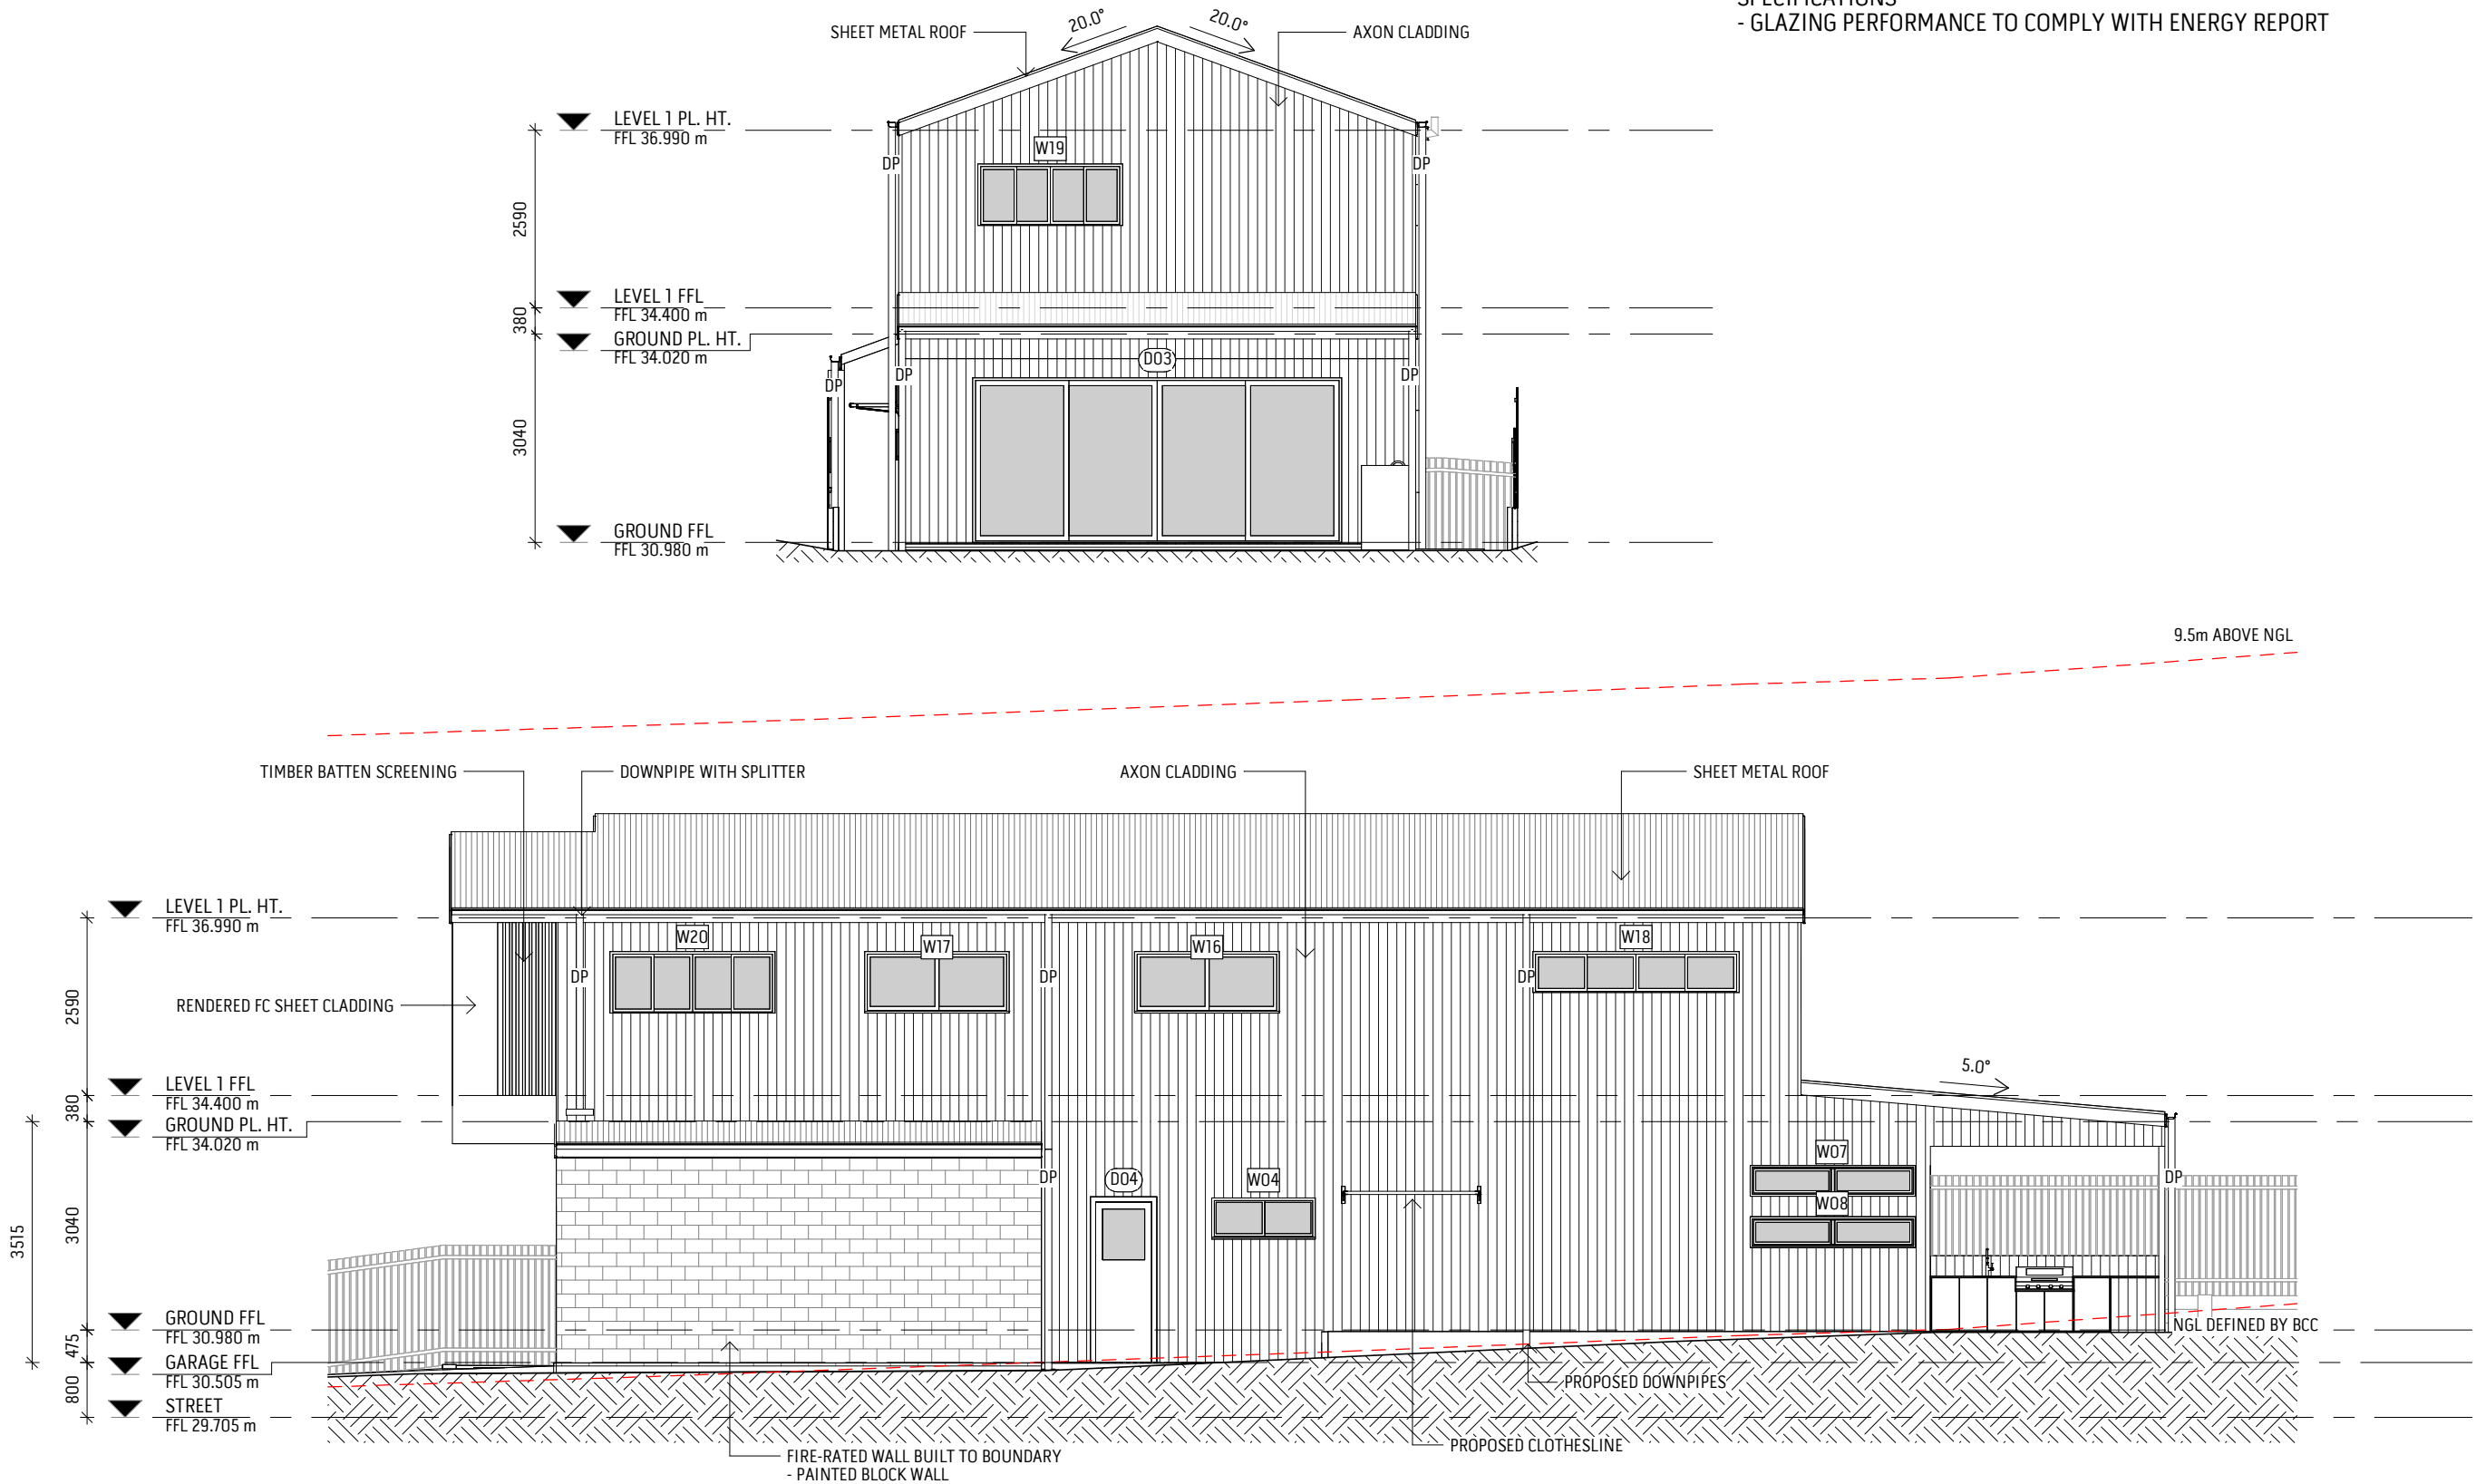

DATE	DESCRIPTION	REV. NO.
03-02-2026	TECHNICAL UPDATES	H
10-02-2026	TECHNICAL UPDATES	I
18-02-2026	CONSTRUCTION REVIEW	J

PILGRIM retains copyright in all documents and drawings and in any works executed from those documents and drawings.
The PILGRIM reserves all present and future moral rights in all intellectual property in the designs, the documents, drawings and any works executed or to be executed from them.
PILGRIM by agreement grants the client a license to use the documents and drawings to produce the project, for which they were intended, conditional upon the following:
- the license applies only to the site or that part of the site to which the design relates.
- PILGRIM has completed the particular stage or stages of design service for which PILGRIM has been commissioned.
- fees properly due to the designer have been paid in full.
Do not scale from drawings, verify all dimensions prior to commencement of construction or fabrication, notify the designer of any discrepancies.

DRAWING TITLE :

PROPOSED ELEVATIONS

MADELEINE & NICHOLAS CHILDS

106 HAROLD STREET, HOLLAND PARK

SCALE : 1:100




ABN: 89 639 943 187
QBCC: 1523 8743

DRAWN : TH
CHECK BY : CA

DRAWING NO: A-03-02

DATE 18-02-2026
REV J

PILGRIM[®]

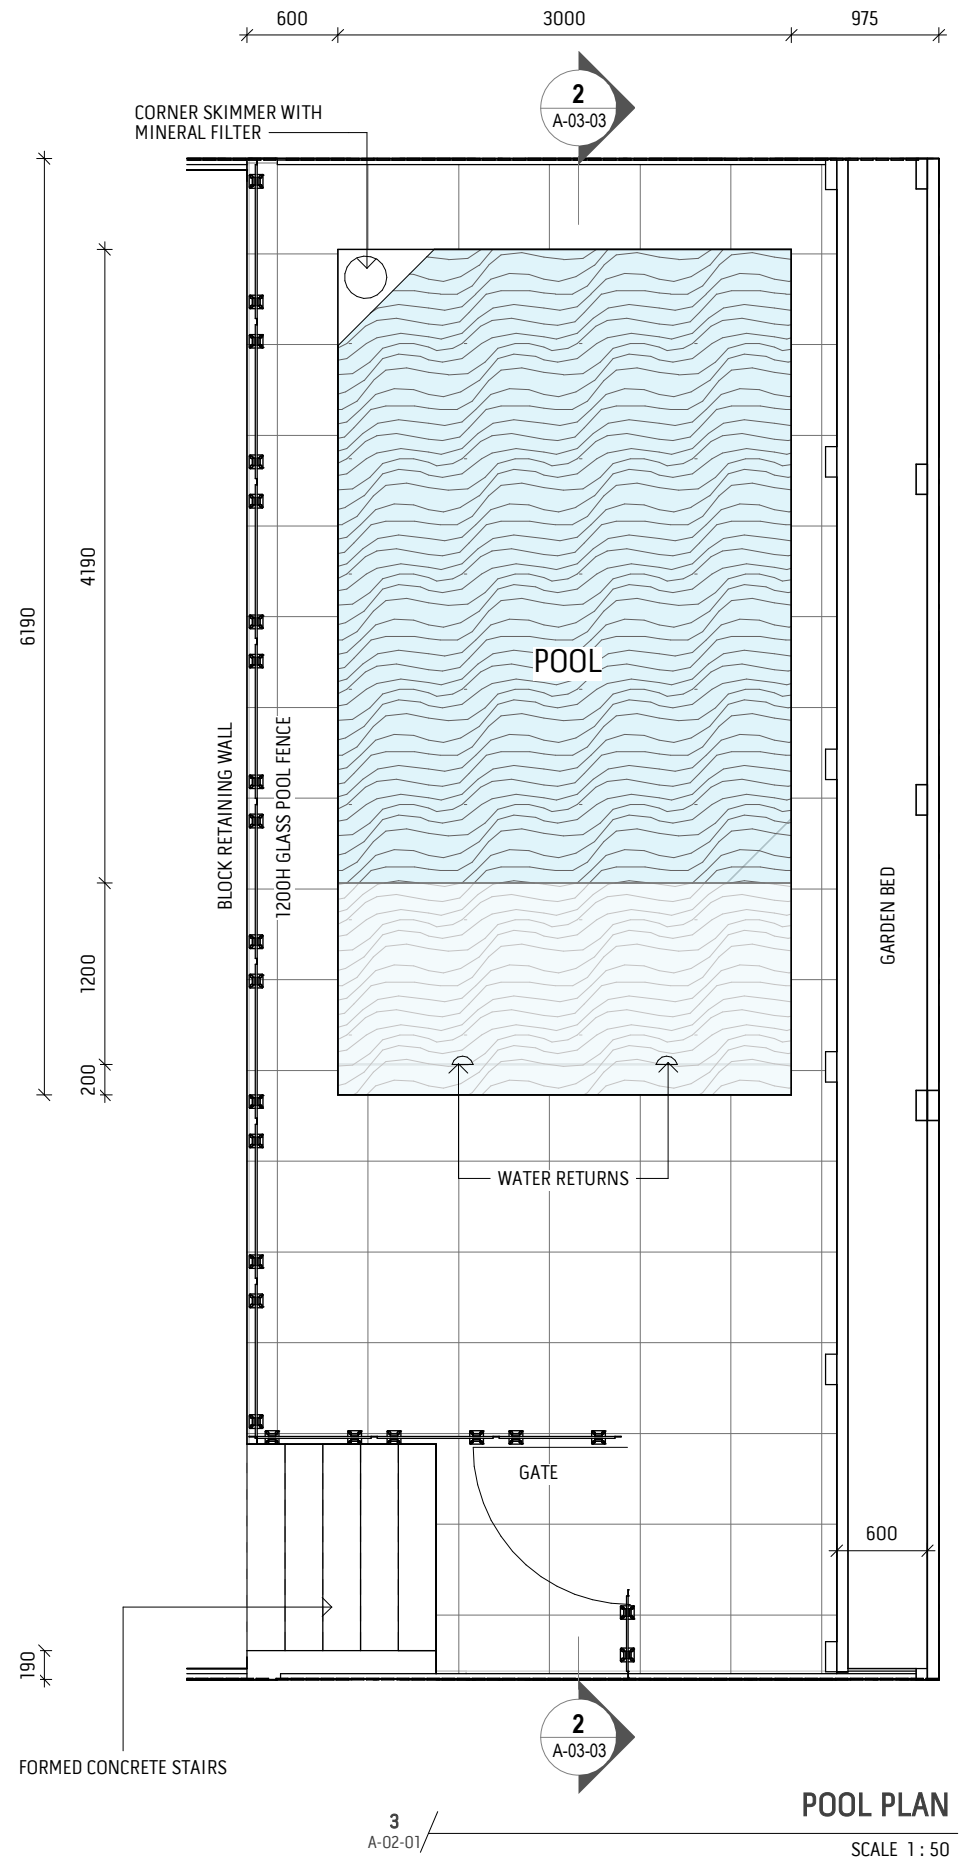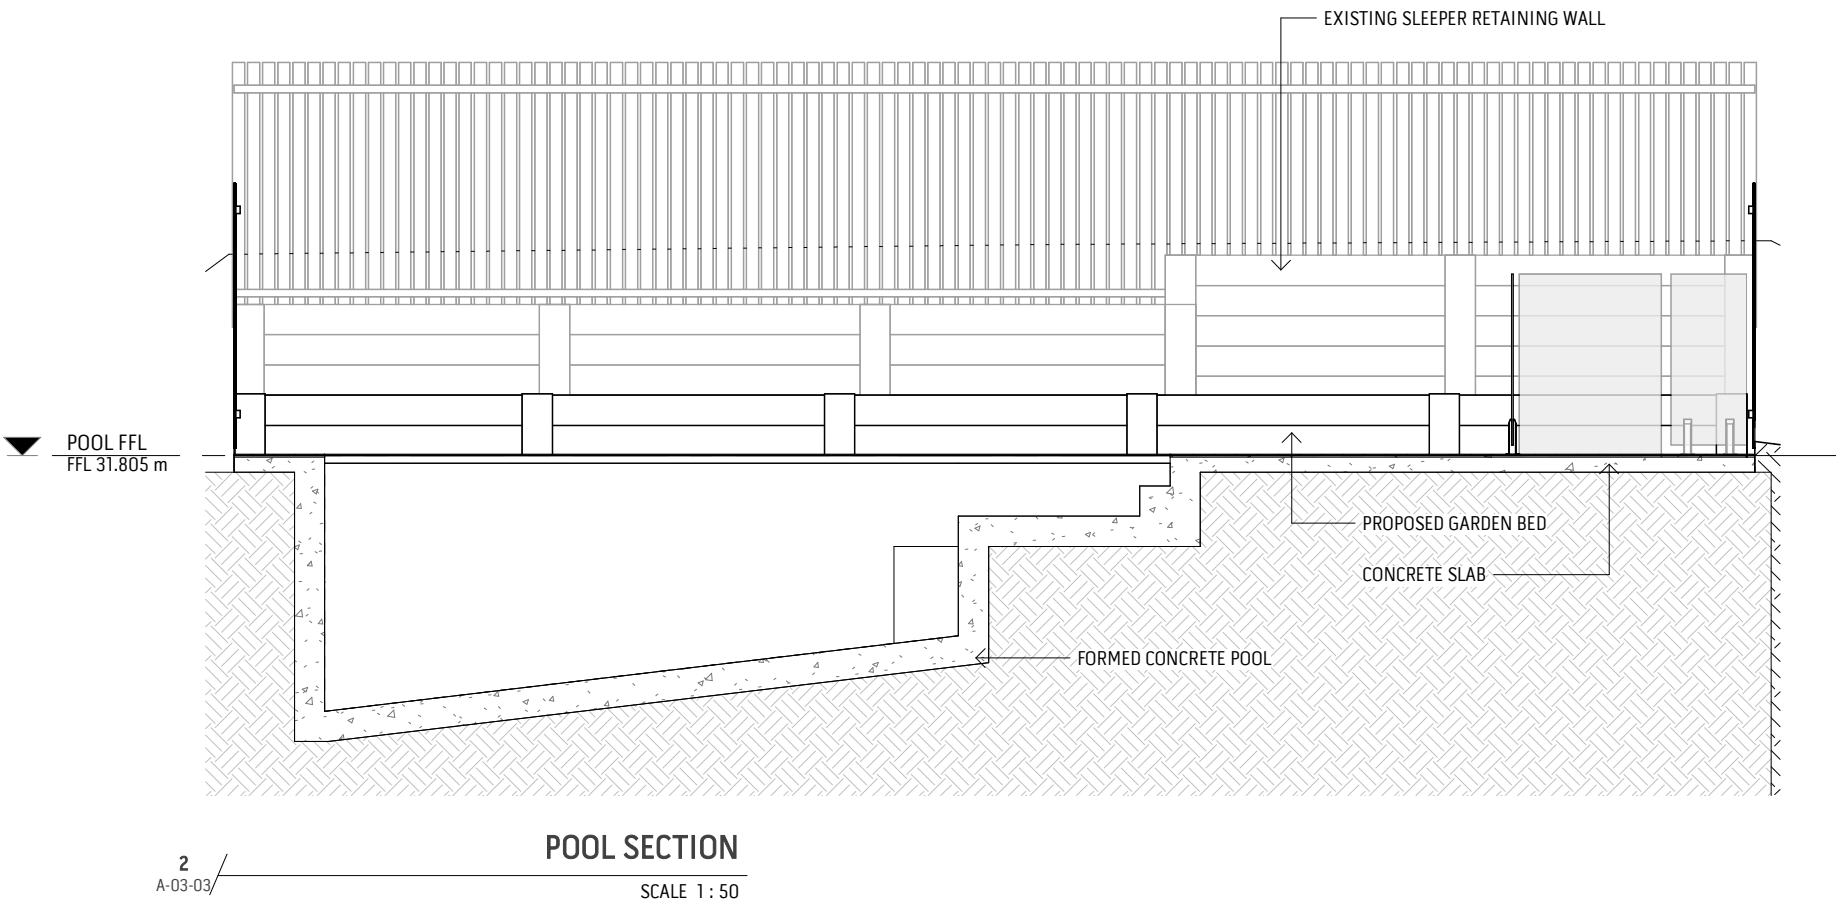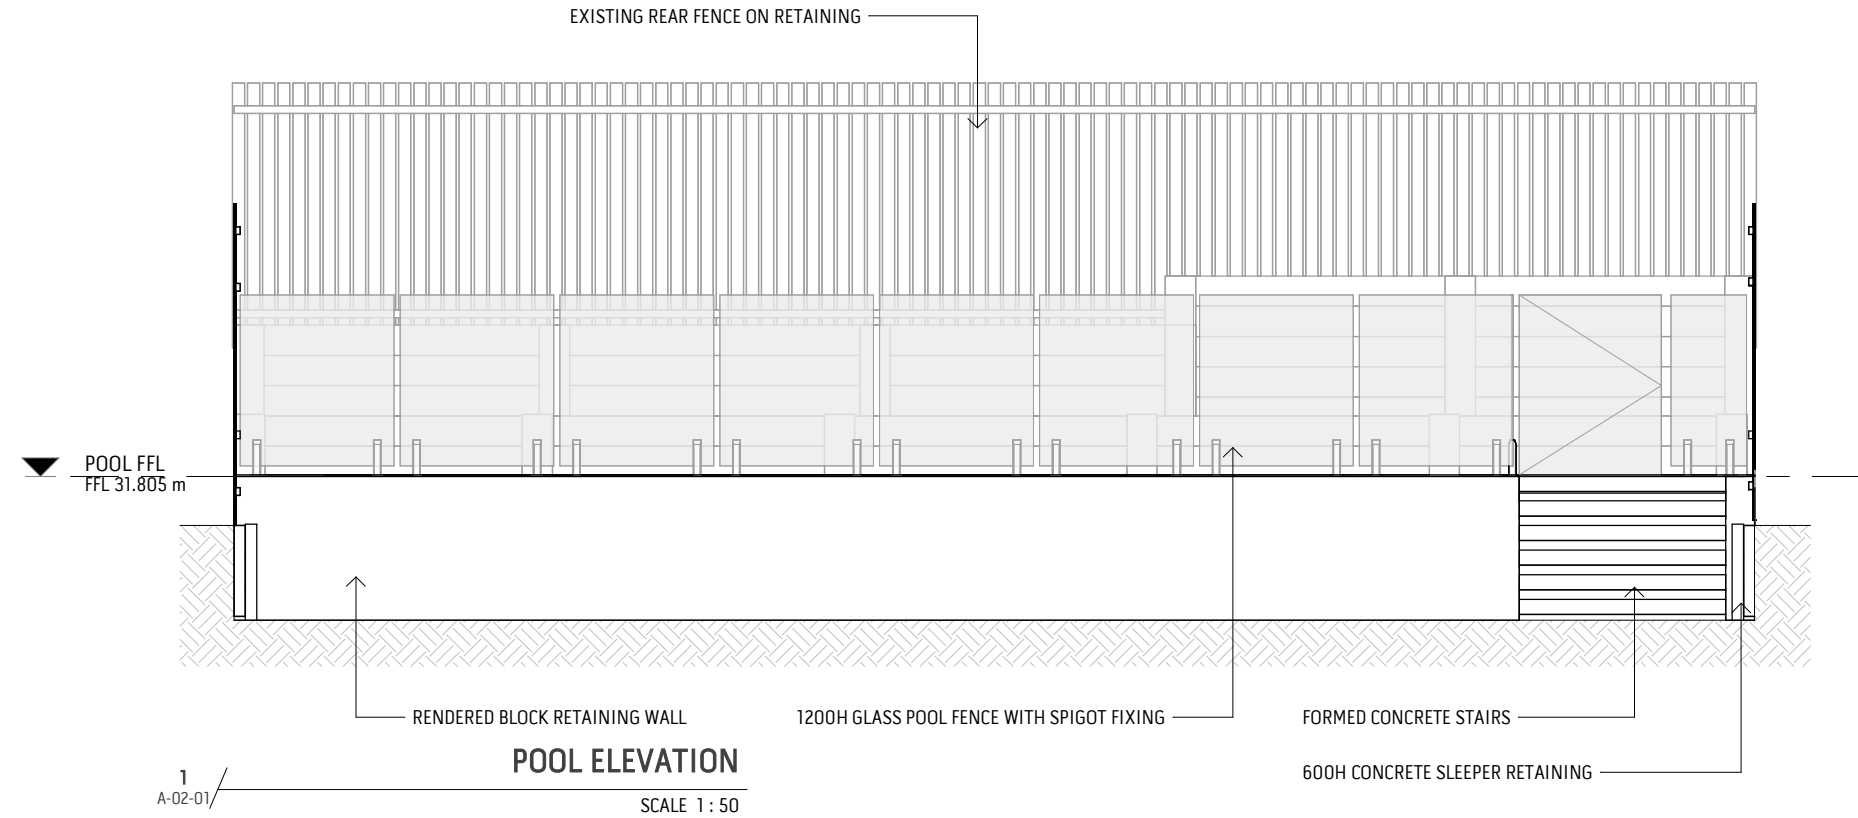

DATE	DESCRIPTION	REV. NO.
03-02-2026	TECHNICAL UPDATES	H
10-02-2026	TECHNICAL UPDATES	I
18-02-2026	CONSTRUCTION REVIEW	J

PILGRIM retains copyright in all documents and drawings and in any works executed from those documents and drawings.
The PILGRIM reserves all present and future moral rights in all intellectual property in the designs, the documents, drawings and any works executed or to be executed from them.

PILGRIM by agreement grants the client a license to use the documents and drawings to produce the project, for which they were intended, conditional upon the following:

- the license applies only to the site or that part of the site to which the design relates,
- PILGRIM has completed the particular stage or stages of design service for which PILGRIM has been commissioned,
- fees properly due to the designer have been paid in full.


Do not scale from drawings, verify all dimensions prior to commencement of construction or fabrication, notify the designer of any discrepancies.

DRAWING TITLE :	MADELEINE & NICHOLAS CHILDS
POOL PLAN	
106 HAROLD STREET, HOLLAND PARK	

SCALE :	1 : 50
ABN:	89 639 943 187
QBCC:	1523 8743
DRAWN :	TH
CHECK BY :	CA
DRAWING NO:	A-03-03
DATE	18-02-2026
REV	J

FENCE ELEVATION NOTES:


- FENCE HEIGHTS AND LOCATIONS TO COMPLY WITH COUNCIL REGULATIONS, SETBACKS AND RELEVANT OVERLAYS
- ALL FENCING TO BE CONSTRUCTED IN ACCORDANCE WITH MANUFACTURER GUIDELINES AND AUSTRALIAN STANDARDS APPLICABLE TO THE MATERIAL TYPE
- WHERE FENCES SIT ATOP RETAINING WALLS, ENSURE STRUCTURAL ENGINEER CONFIRMS WALL CAPACITY AND FIXING METHOD
- ALL DIMENSIONS SHOWN ARE INDICATIVE - CONFIRM ON SITE BEFORE FABRICATION
- TIMBER FENCING TO RECEIVE APPROPRIATE TREATMENT LEVEL FOR IN-GROUND OR ABOVE-GROUND USE
- METAL OR ALUMINIUM FENCING TO BE POWDERCOATED AND CORROSION PROTECTED
- CONFIRM FINAL LOCATIONS AND HEIGHTS OF FENCES RELATIVE TO FINISHED GROUND LEVELS

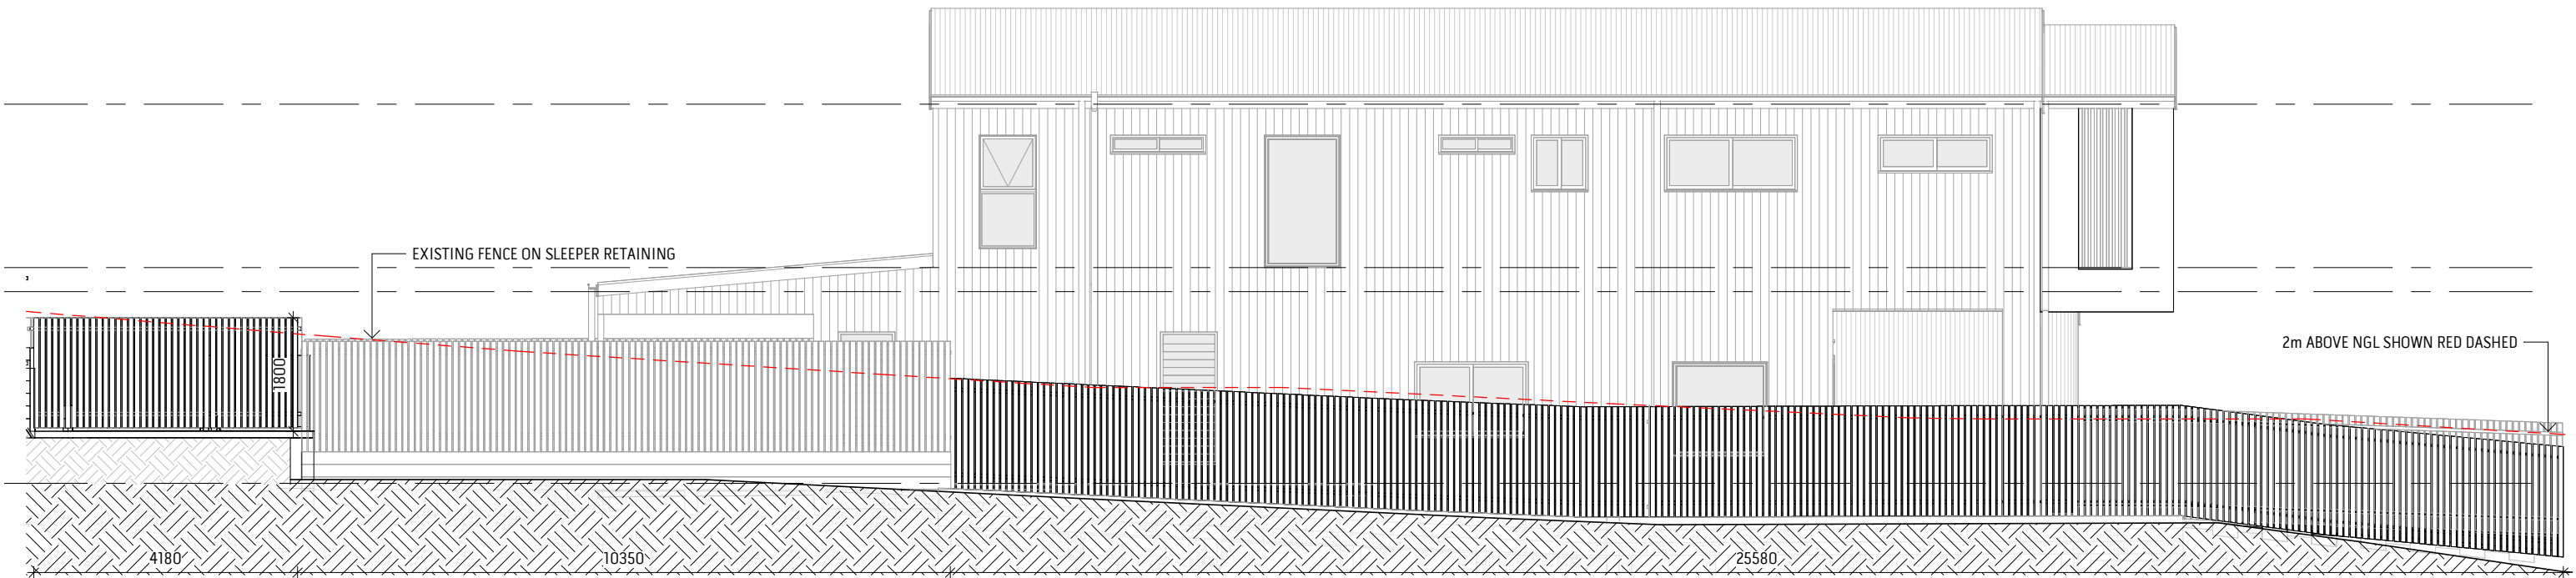

FENCE ELEVATION A

2
A-03-03/

SCALE 1 : 100

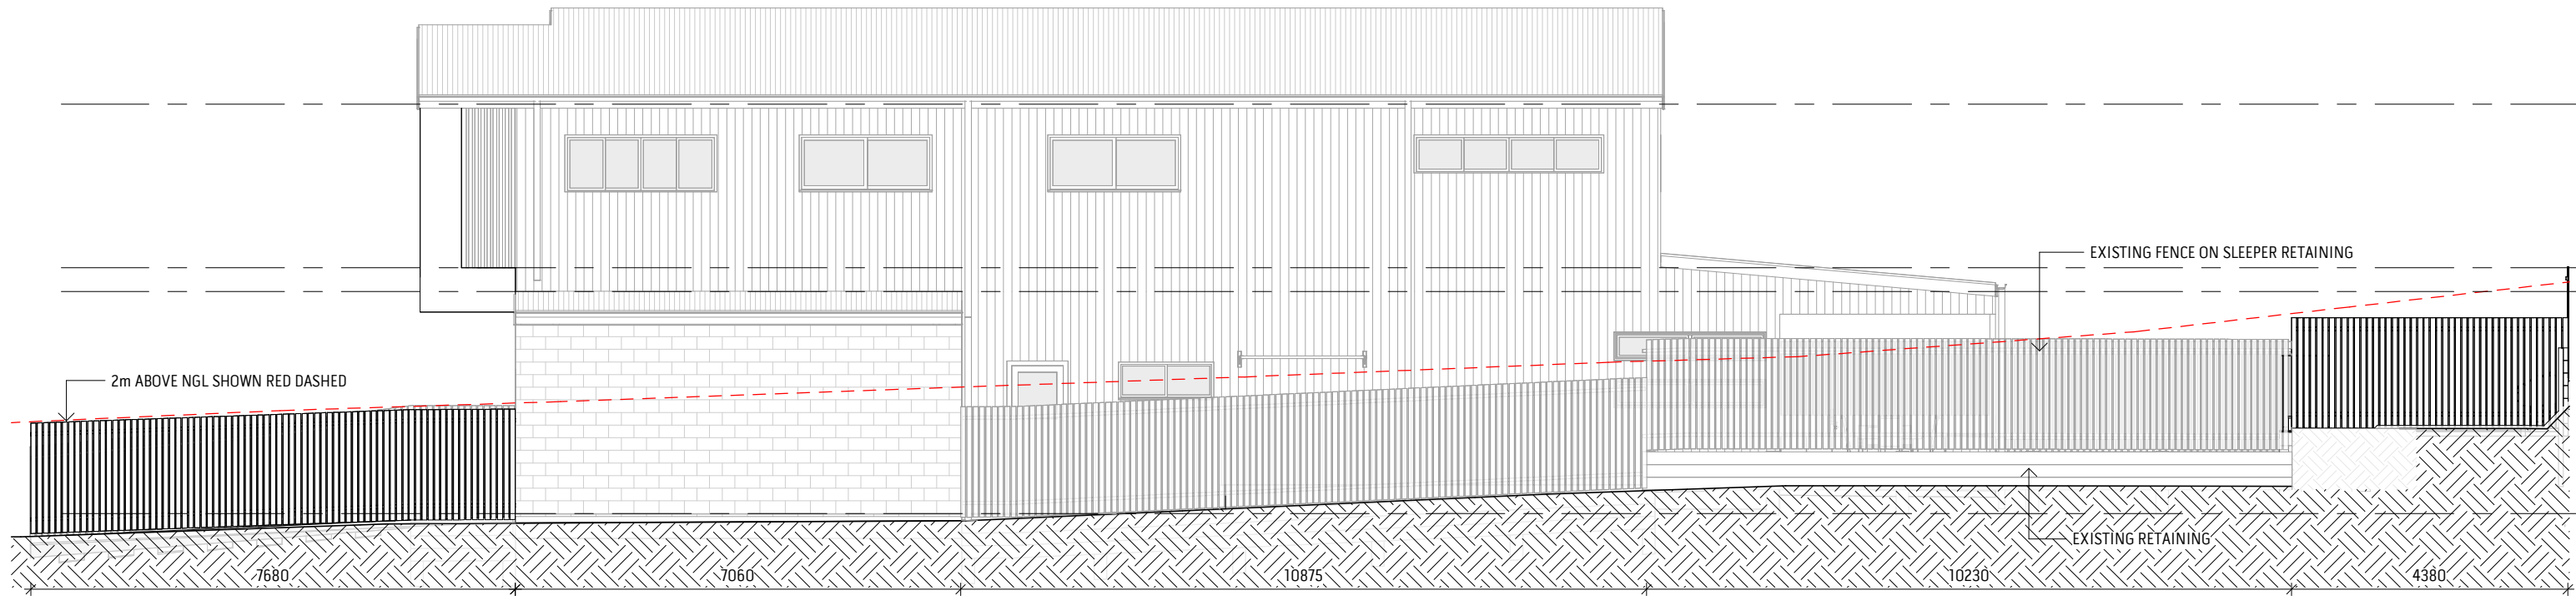

FENCE ELEVATION B

1
A-03-03/

SCALE 1 : 100

DATE	DESCRIPTION	REV. NO.
03-02-2026	TECHNICAL UPDATES	H
10-02-2026	TECHNICAL UPDATES	I
18-02-2026	CONSTRUCTION REVIEW	J

PILGRIM retains copyright in all documents and drawings and in any works executed from those documents and drawings.
The PILGRIM reserves all present and future moral rights in all intellectual property in the designs, the documents, drawings and any works executed or to be executed from them.
PILGRIM by agreement grants the client a license to use the documents and drawings to produce the project, for which they were intended, conditional upon the following:
- the license applies only to the site or that part of the site to which the design relates.
- PILGRIM has completed the particular stage or stages of design service for which PILGRIM has been commissioned.
- fees properly due to the designer have been paid in full.
Do not scale from drawings, verify all dimensions prior to commencement of construction or fabrication, notify the designer of any discrepancies.

DRAWING TITLE :


FENCE ELEVATIONS

MADELEINE & NICHOLAS CHILDS


106 HAROLD STREET, HOLLAND PARK

PILGRIM®

SCALE :	1:100		
ABN:	89 639 943 187		
QBCC:	1523 8743		
DRAWN :	TH	CHECK BY :	CA
DRAWING NO:	A-03-04		
DATE	18-02-2026	REV	J

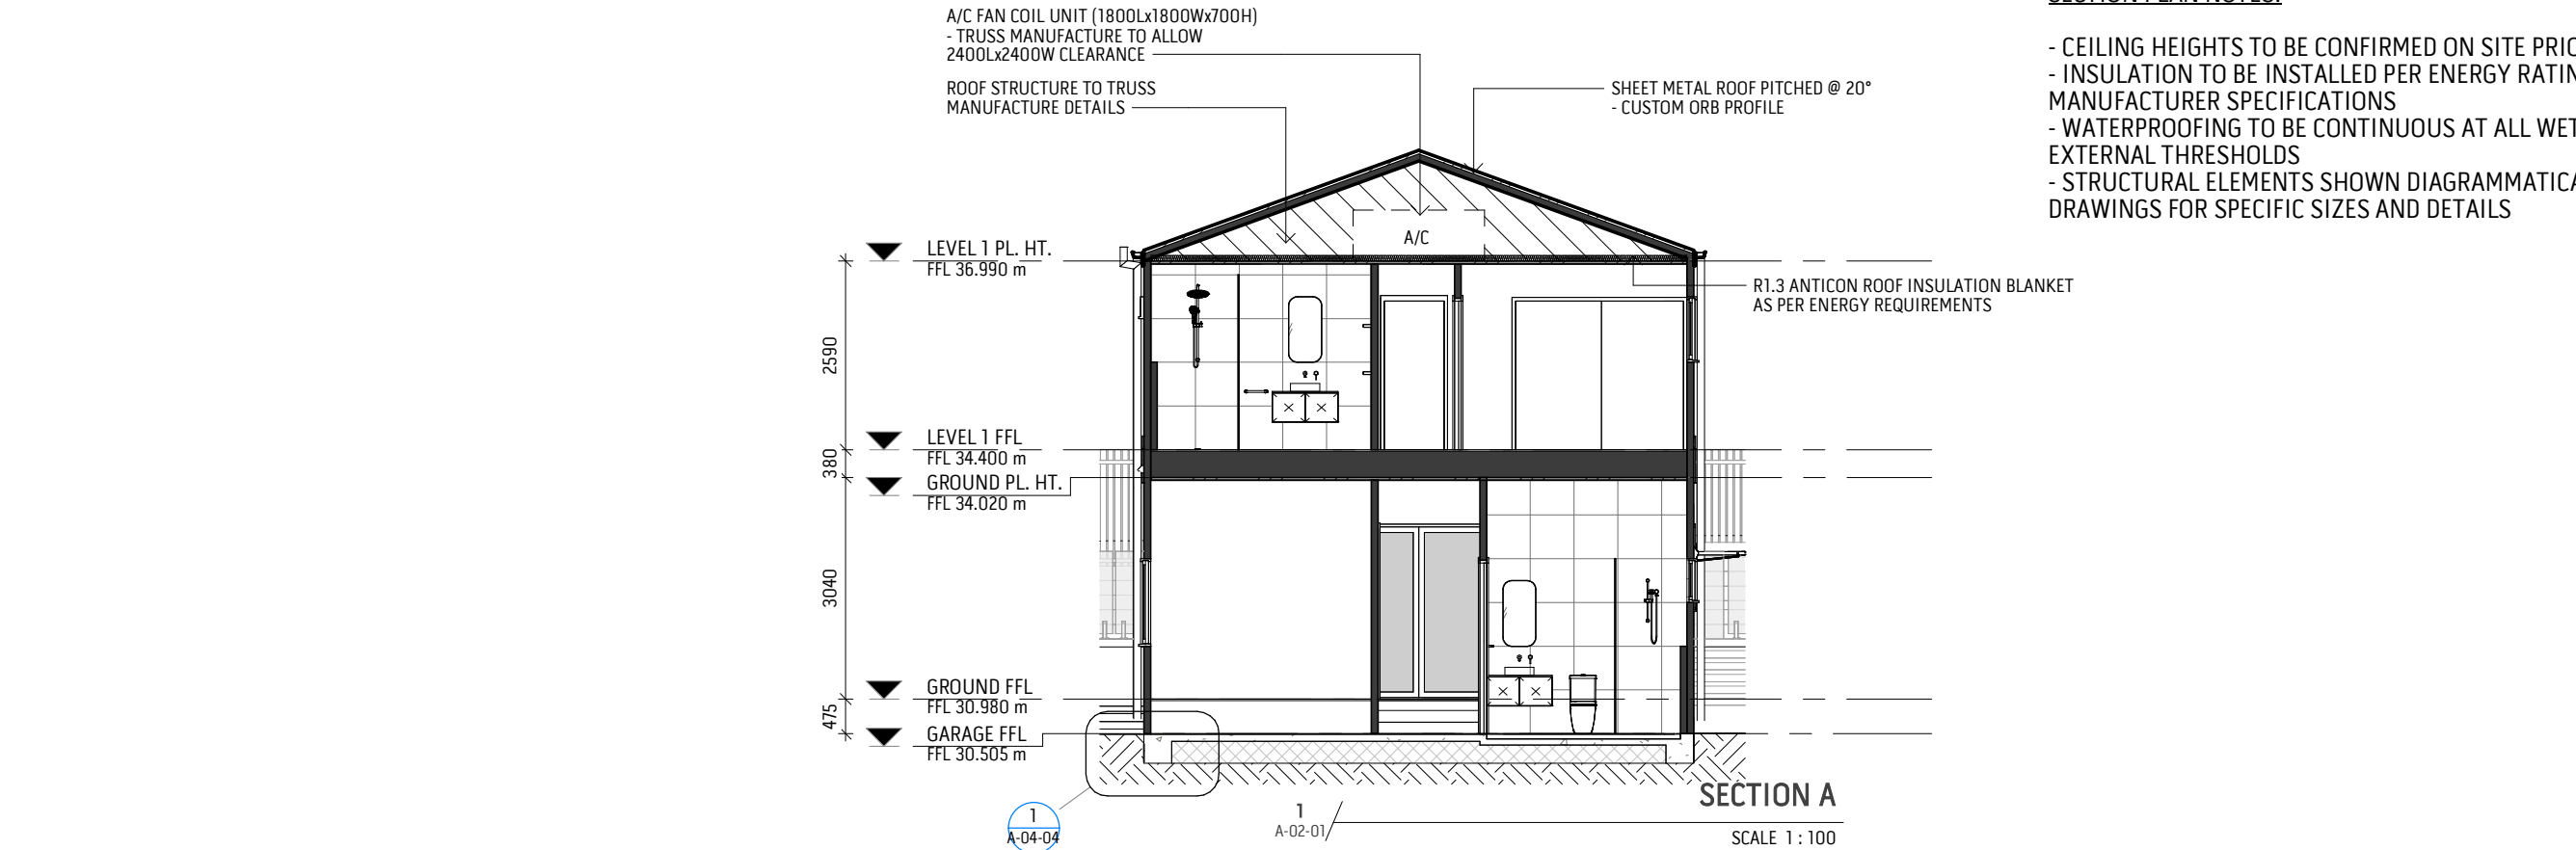


- SECTION PLAN NOTES:
- CEILING HEIGHTS TO BE CONFIRMED ON SITE PRIOR TO FRAMING
 - INSULATION TO BE INSTALLED PER ENERGY RATING REQUIREMENTS AND MANUFACTURER SPECIFICATIONS
 - WATERPROOFING TO BE CONTINUOUS AT ALL WET AREAS, BALCONIES AND EXTERNAL THRESHOLDS
 - STRUCTURAL ELEMENTS SHOWN DIAGRAMMATICALLY - REFER TO STRUCTURAL DRAWINGS FOR SPECIFIC SIZES AND DETAILS

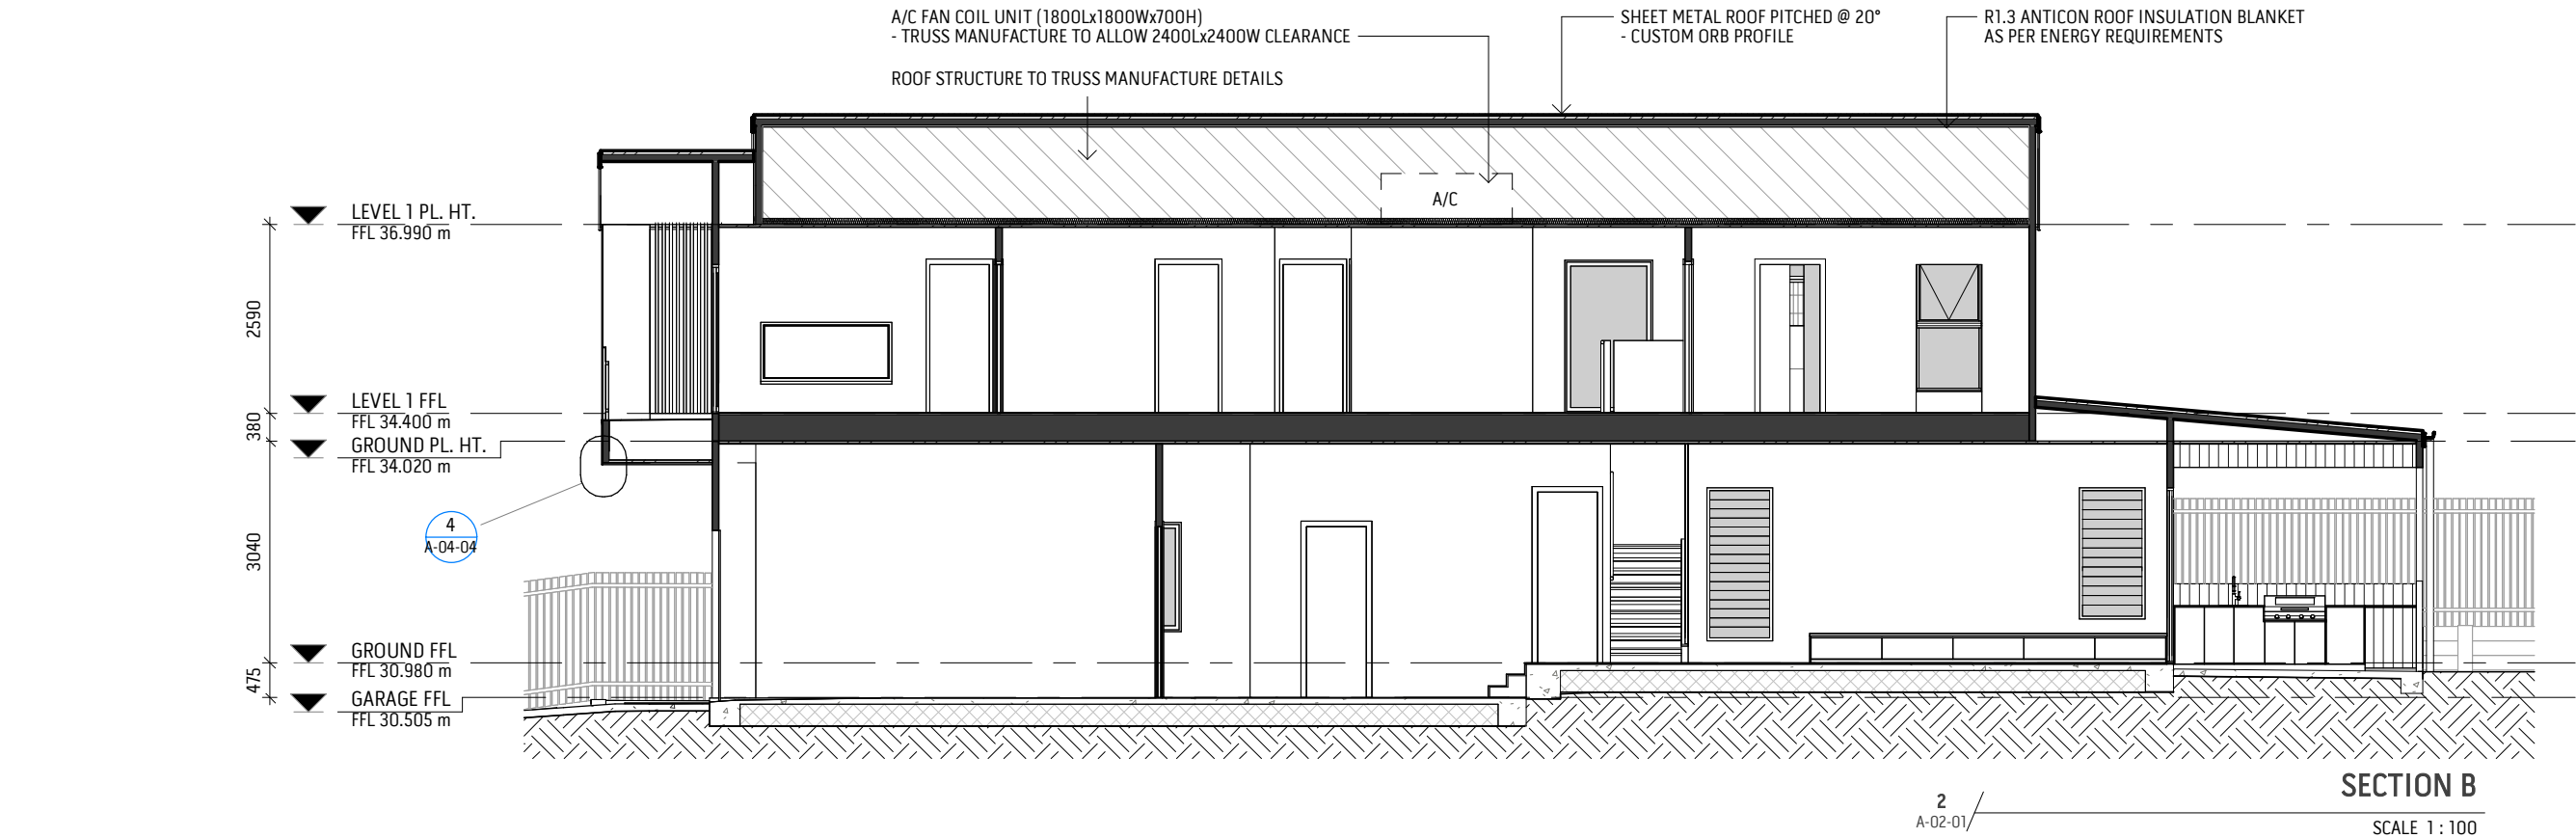

DATE	DESCRIPTION	REV. NO.	DRAWING TITLE : SECTIONS MADELEINE & NICHOLAS CHILDS 106 HAROLD STREET, HOLLAND PARK	PILGRIM®	SCALE : 1 : 100		
03-02-2026	TECHNICAL UPDATES	H			ABN: 89 639 943 187		
10-02-2026	TECHNICAL UPDATES	I			QBCC: 1523 8743		
18-02-2026	CONSTRUCTION REVIEW	J			DRAWN : TH	CHECK BY : CA	
PILGRIM retains copyright in all documents and drawings and in any works executed from those documents and drawings. The PILGRIM reserves all present and future moral rights in all intellectual property in the designs, the documents, drawings and any works executed or to be executed from them.			DRAWING NO: A-04-01				
PILGRIM by agreement grants the client a license to use the documents and drawings to produce the project, for which they were intended, conditional upon the following: - the license applies only to the site or that part of the site to which the design relates. - PILGRIM has completed the particular stage or stages of design service for which PILGRIM has been commissioned. - fees properly due to the designer have been paid in full. Do not scale from drawings, verify all dimensions prior to commencement of construction or fabrication, notify the designer of any discrepancies.			DATE 18-02-2026				
			REV J				

PILGRIM®


- SECTION PLAN NOTES:
- CEILING HEIGHTS TO BE CONFIRMED ON SITE PRIOR TO FRAMING
 - INSULATION TO BE INSTALLED PER ENERGY RATING REQUIREMENTS AND MANUFACTURER SPECIFICATIONS
 - WATERPROOFING TO BE CONTINUOUS AT ALL WET AREAS, BALCONIES AND EXTERNAL THRESHOLDS
 - STRUCTURAL ELEMENTS SHOWN DIAGRAMMATICALLY - REFER TO STRUCTURAL DRAWINGS FOR SPECIFIC SIZES AND DETAILS

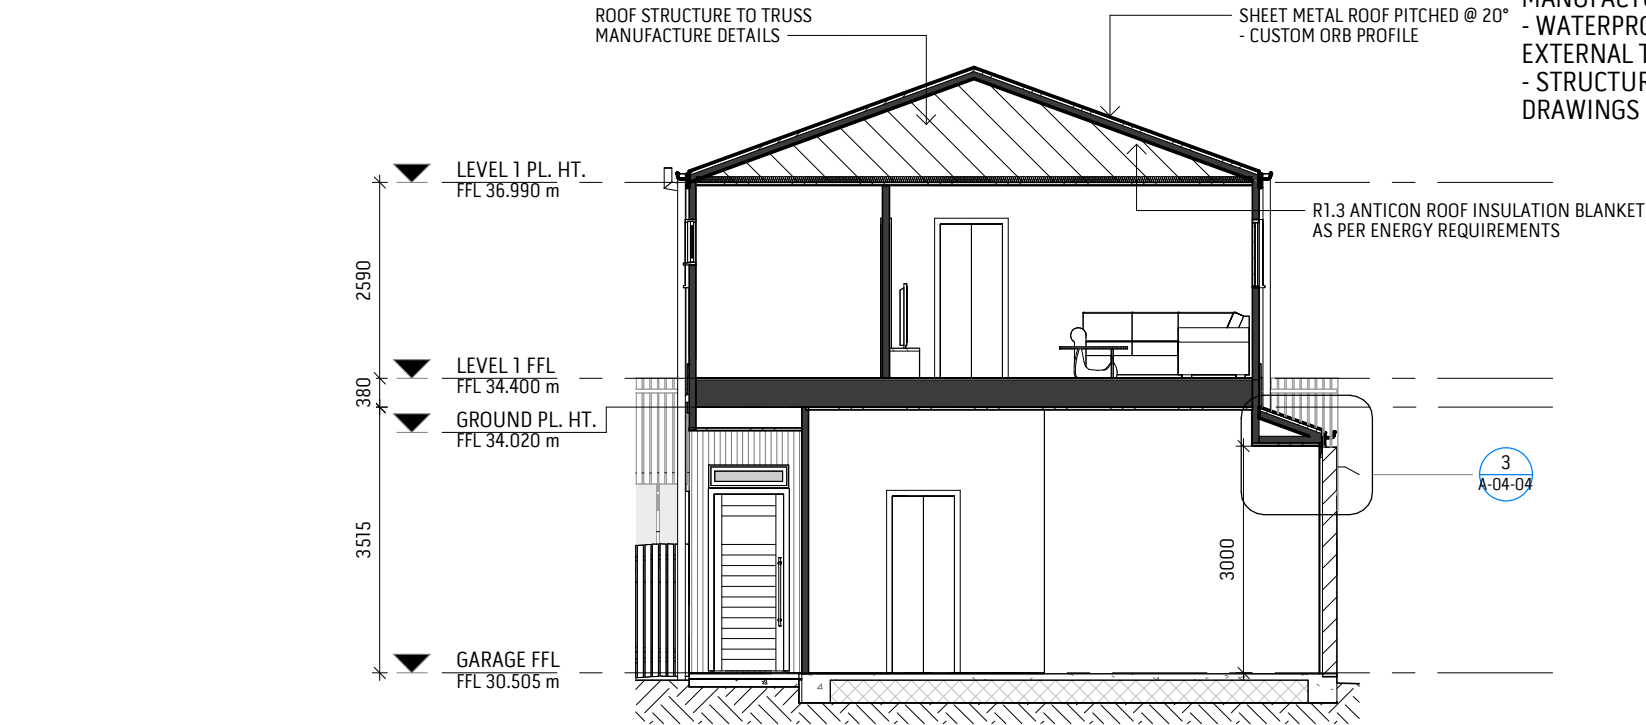

1
A-02-01

SECTION C

SCALE 1 : 100

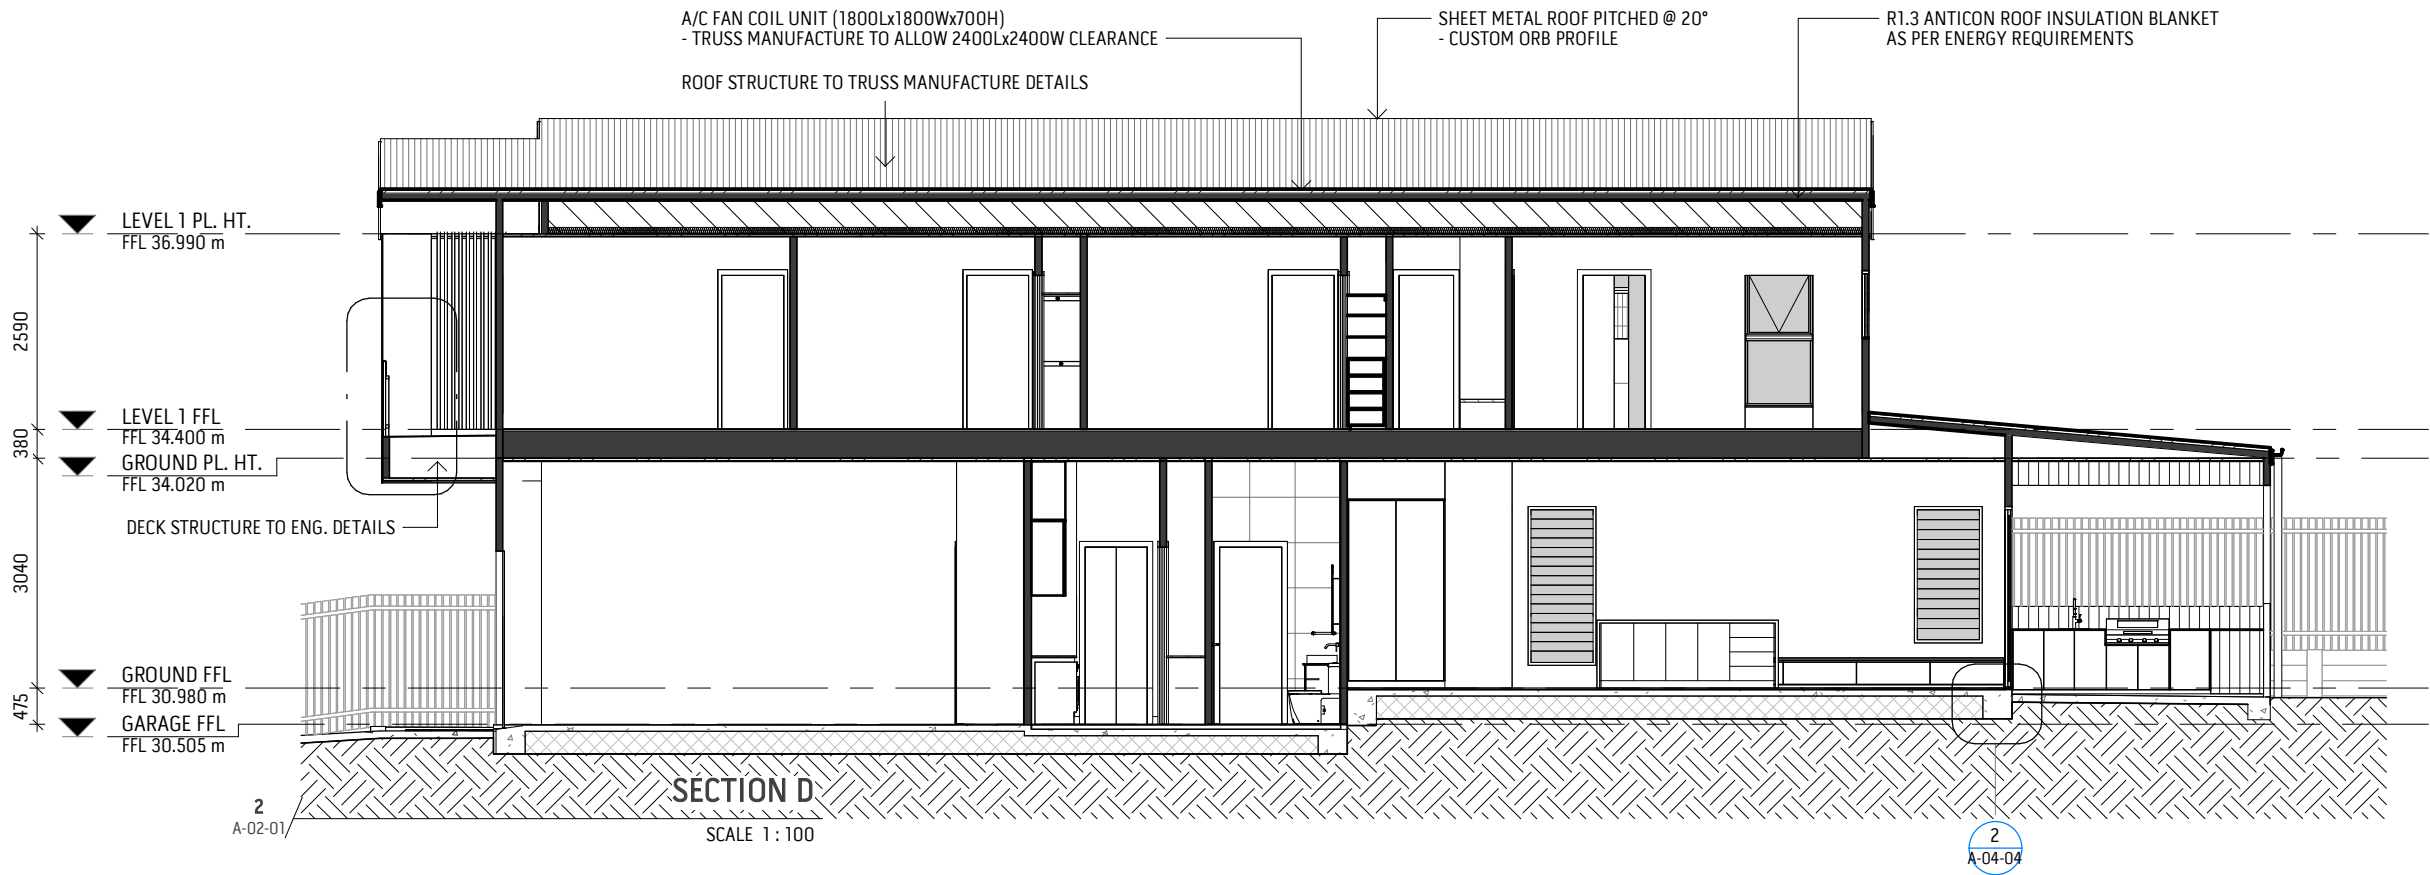

2
A-02-01

SECTION D

SCALE 1 : 100

DATE	DESCRIPTION	REV. NO.
03-02-2026	TECHNICAL UPDATES	H
10-02-2026	TECHNICAL UPDATES	I
18-02-2026	CONSTRUCTION REVIEW	J

PILGRIM retains copyright in all documents and drawings and in any works executed from those documents and drawings.
The PILGRIM reserves all present and future moral rights in all intellectual property in the designs, the documents, drawings and any works executed or to be executed from them.





PILGRIM by agreement grants the client a license to use the documents and drawings to produce the project, for which they were intended, conditional upon the following:

- the license applies only to the site or that part of the site to which the design relates.
- PILGRIM has completed the particular stage or stages of design service for which PILGRIM has been commissioned.
- fees properly due to the designer have been paid in full.

Do not scale from drawings, verify all dimensions prior to commencement of construction or fabrication, notify the designer of any discrepancies.

DRAWING TITLE :	MADELEINE & NICHOLAS CHILDS
SECTIONS	
106 HAROLD STREET, HOLLAND PARK	

SCALE :	1 : 100
ABN:	89 639 943 187
QBCC:	1523 8743
DRAWN :	TH
CHECK BY :	CA
DRAWING NO:	A-04-02
DATE	18-02-2026
REV	J

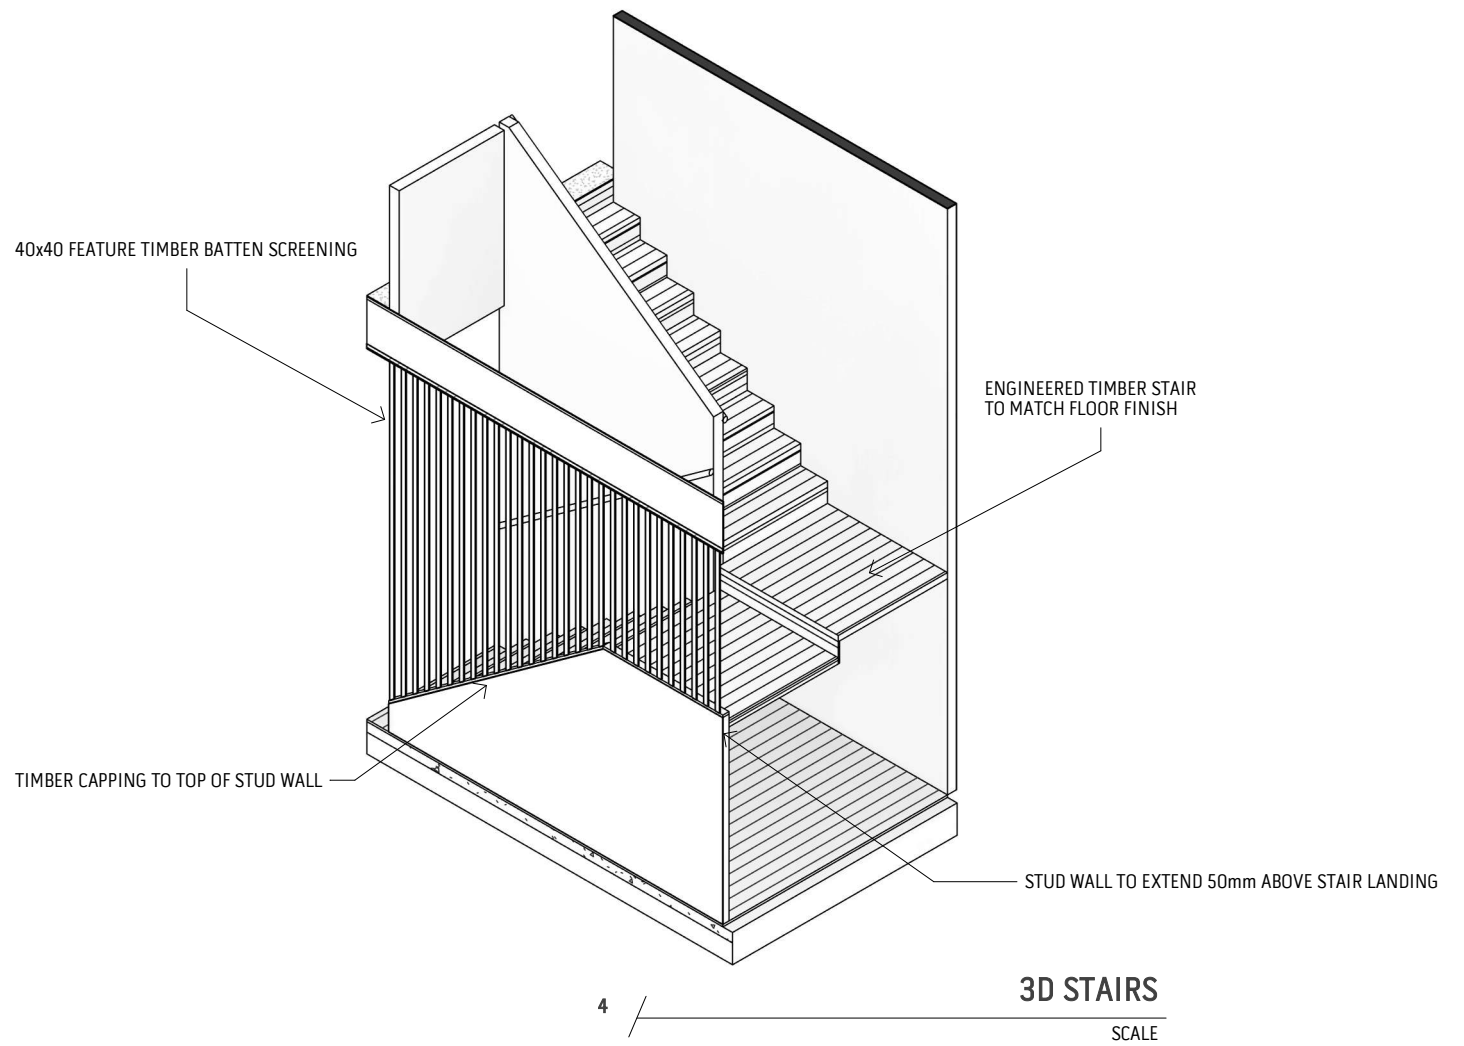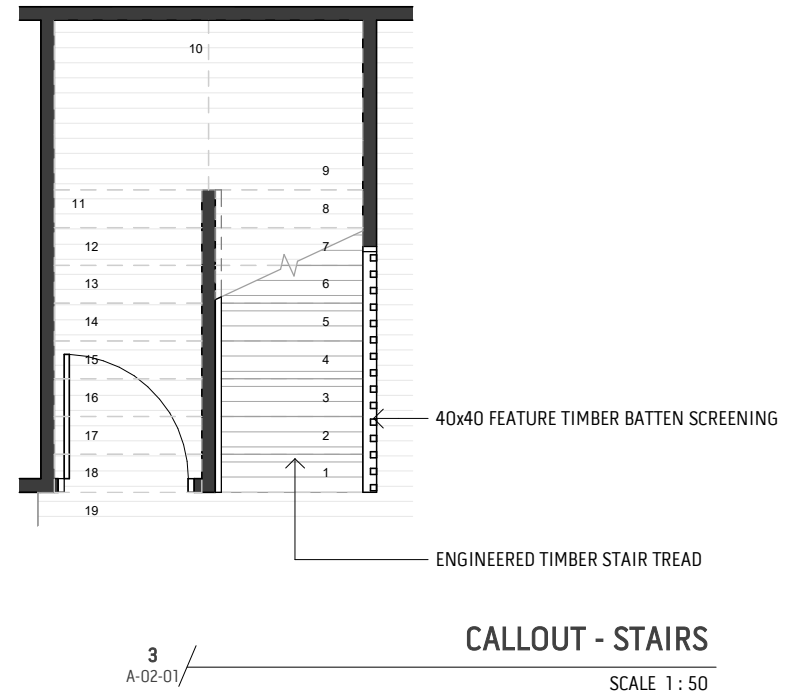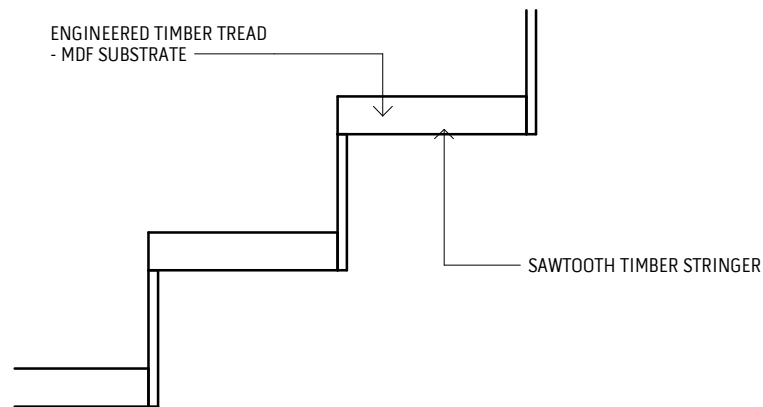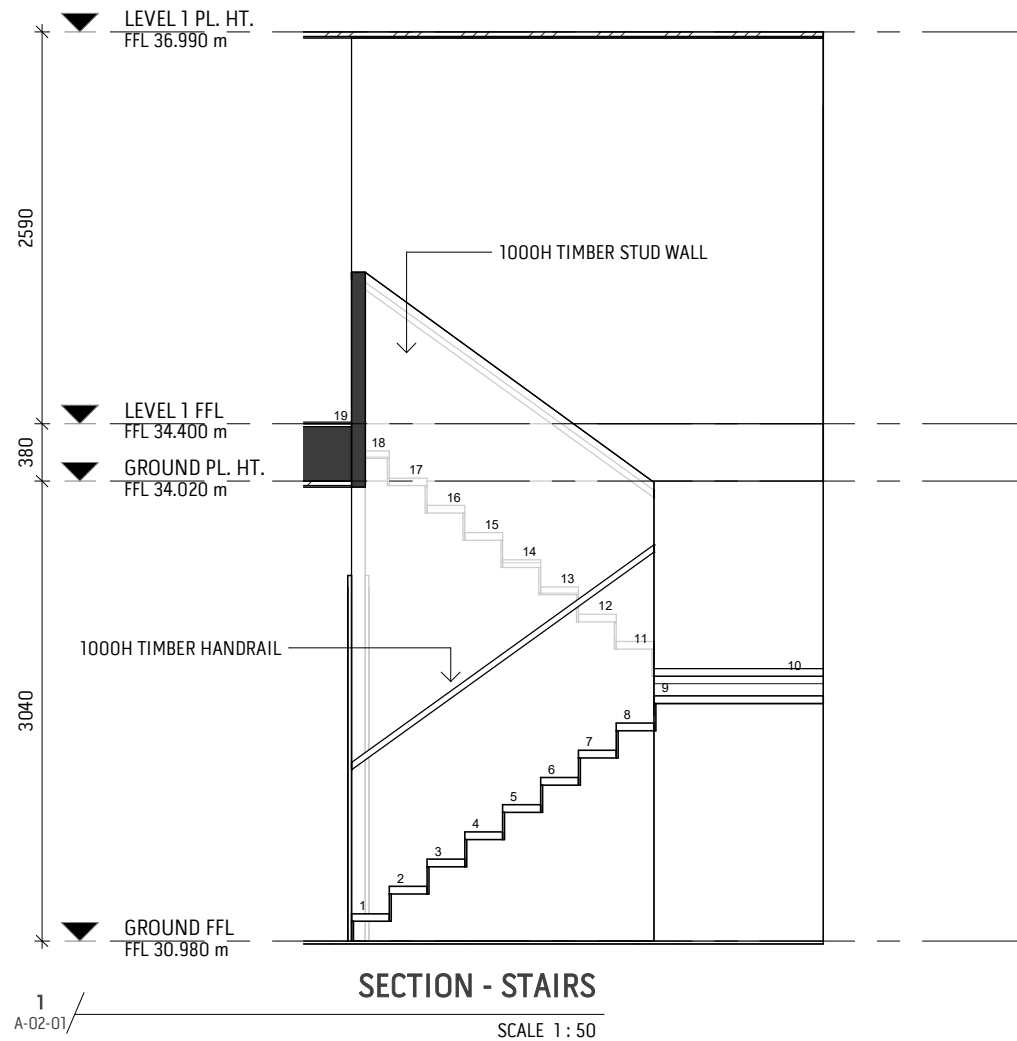

DATE	DESCRIPTION	REV. NO.
03-02-2026	TECHNICAL UPDATES	H
10-02-2026	TECHNICAL UPDATES	I
18-02-2026	CONSTRUCTION REVIEW	J

PILGRIM retains copyright in all documents and drawings and in any works executed from those documents and drawings.
The PILGRIM reserves all present and future moral rights in all intellectual property in the designs, the documents, drawings and any works executed or to be executed from them.


PILGRIM by agreement grants the client a license to use the documents and drawings to produce the project, for which they were intended, conditional upon the following:

- the license applies only to the site or that part of the site to which the design relates.
- PILGRIM has completed the particular stage or stages of design service for which PILGRIM has been commissioned.
- fees properly due to the designer have been paid in full.

Do not scale from drawings, verify all dimensions prior to commencement of construction or fabrication, notify the designer of any discrepancies.


DRAWING TITLE :	MADELEINE & NICHOLAS CHILDS
STAIR DETAIL	
106 HAROLD STREET, HOLLAND PARK	

SCALE :	As indicated
ABN:	89 639 943 187
QBCC:	1523 8743
DRAWN :	TH
CHECK BY :	CA
DRAWING NO:	A-04-03
DATE	18-02-2026
REV	J

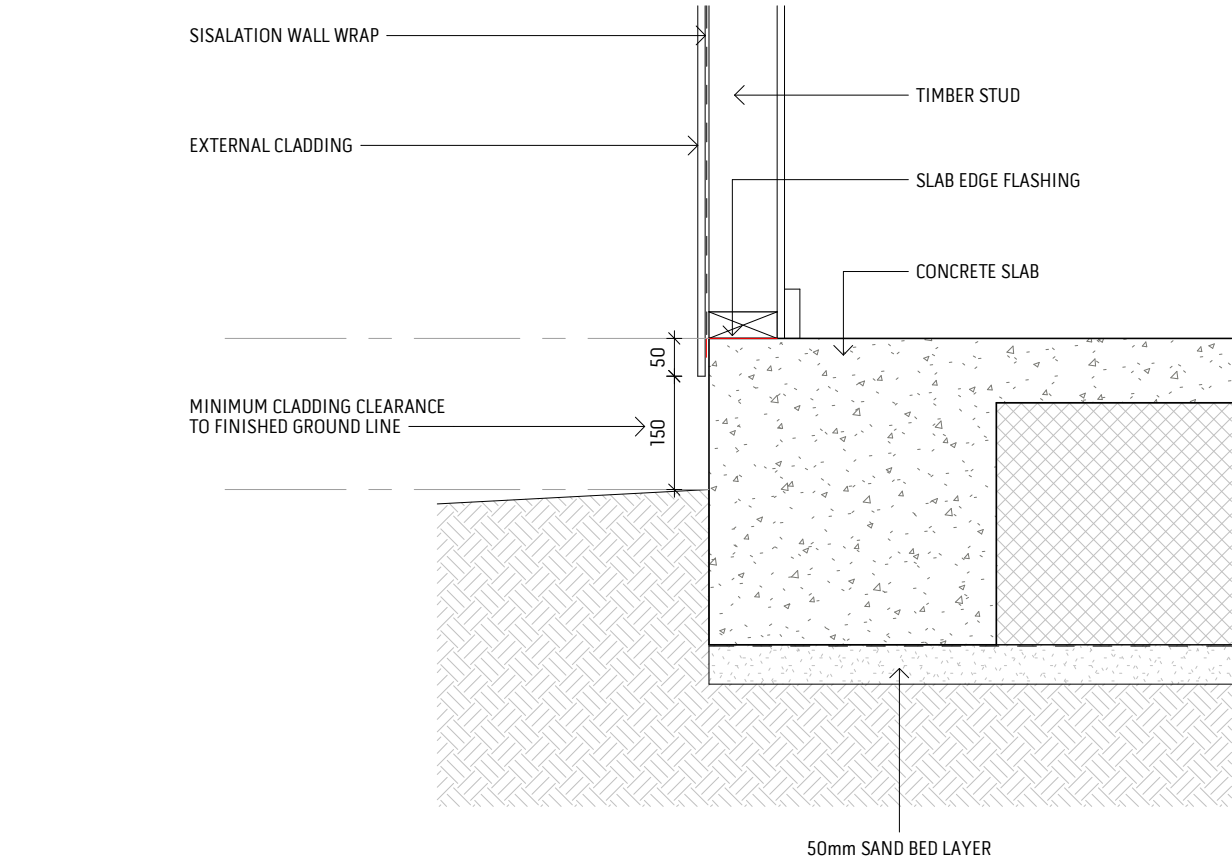


SLAB EDGE DETAIL - CLADDING

1
A-04-01/ SCALE 1 : 10

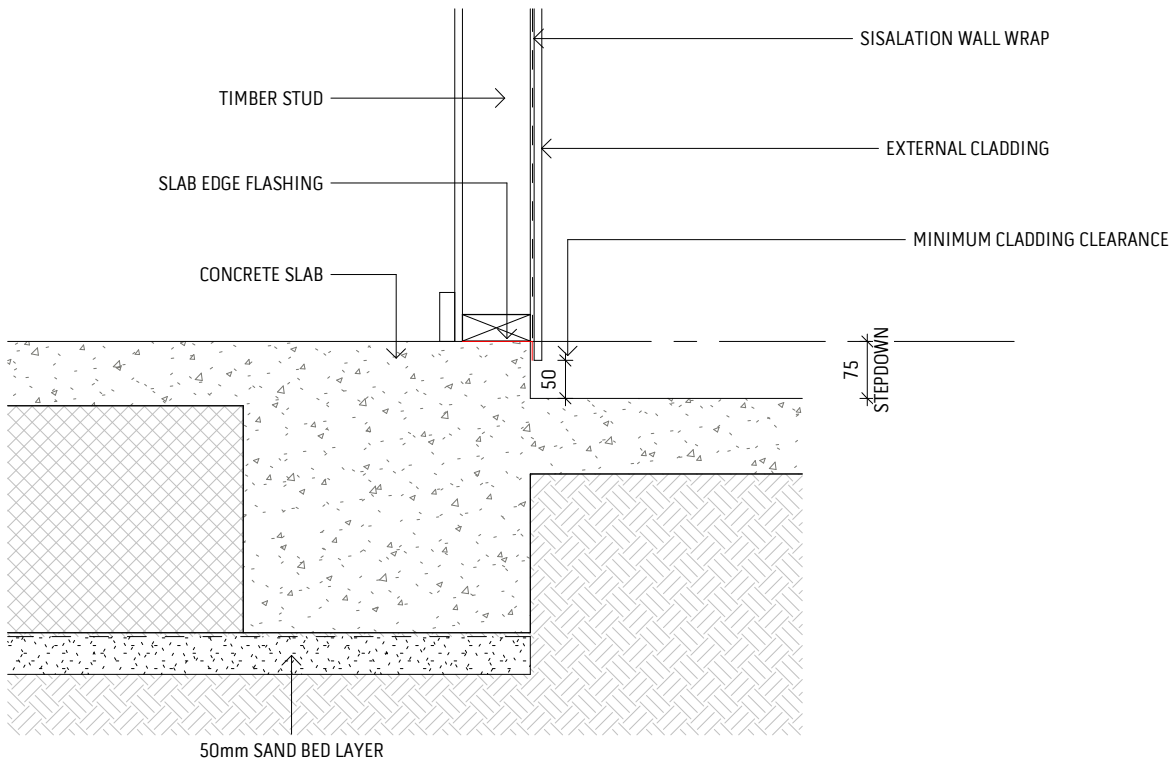


SLAB EDGE DETAIL - ALFRESCO

2
A-04-02/ SCALE 1 : 10

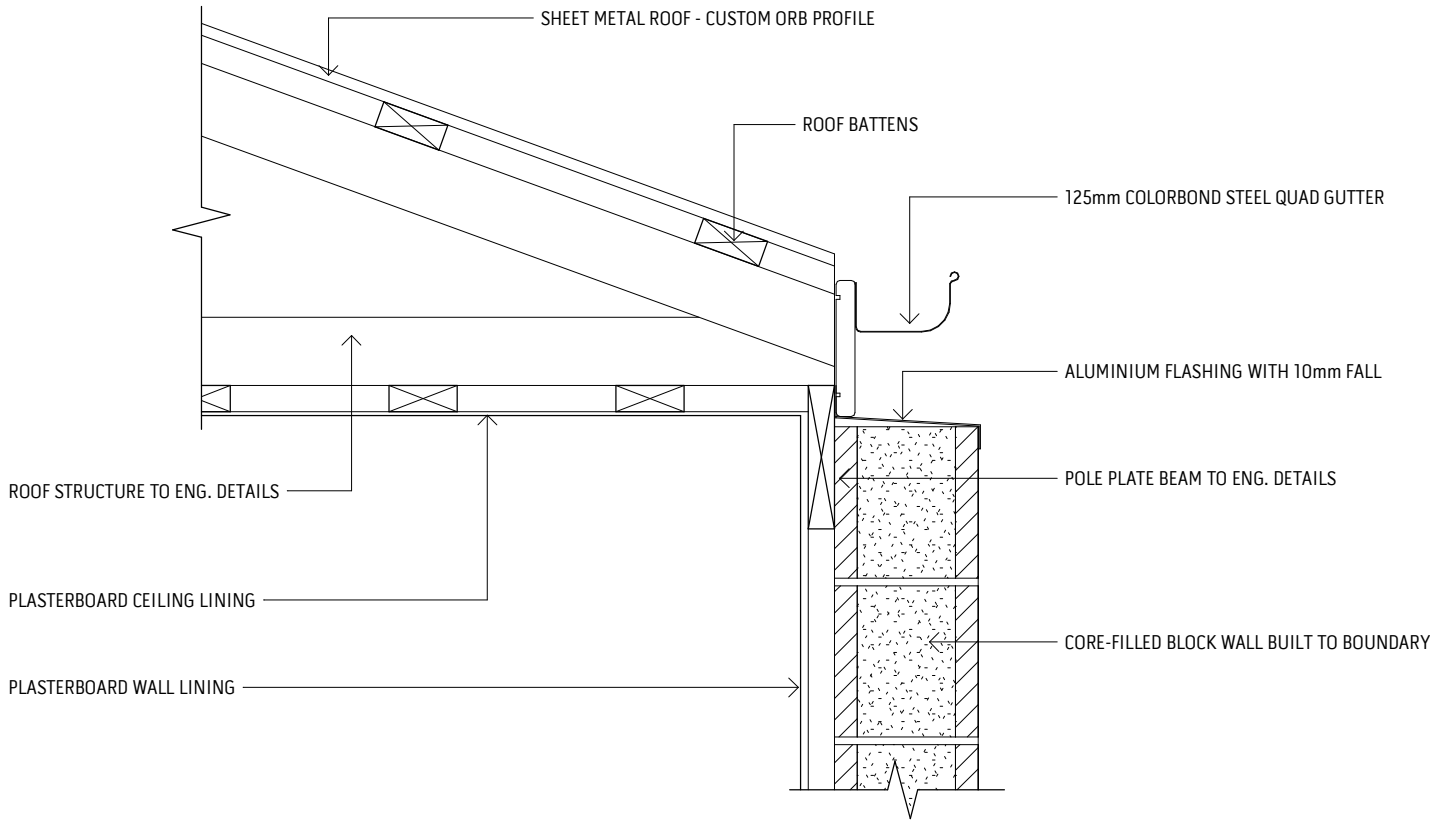

GUTTER OVER BLOCKWORK


3
A-04-02/ SCALE 1 : 10

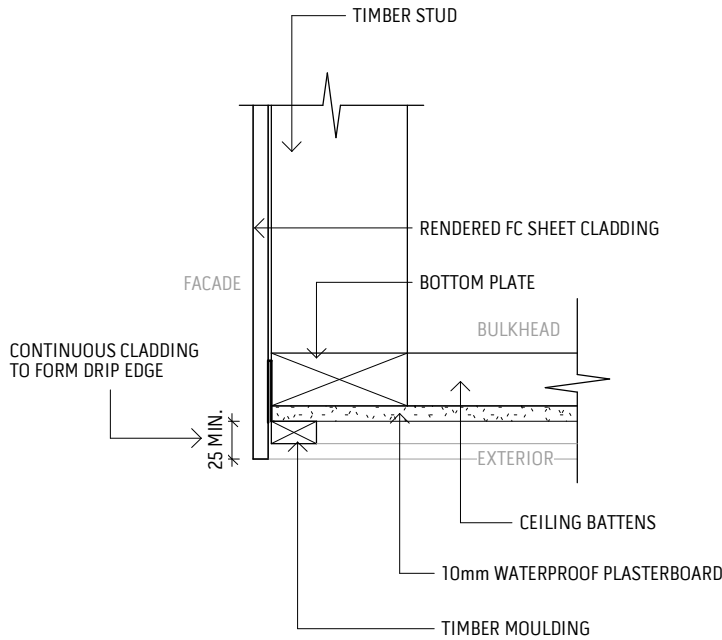


DRIP EDGE DETAIL

4
A-04-01/ SCALE 1 : 5


DATE	DESCRIPTION	REV. NO.	DRAWING TITLE :	SCALE :	As indicated	
03-02-2026	TECHNICAL UPDATES	H	SECTION DETAILS	ABN:	89 639 943 187	
10-02-2026	TECHNICAL UPDATES	I		MADELEINE & NICHOLAS CHILDS	QBCC:	1523 8743
18-02-2026	CONSTRUCTION REVIEW	J		106 HAROLD STREET, HOLLAND PARK	DRAWN :	TH
PILGRIM retains copyright in all documents and drawings and in any works executed from those documents and drawings. The PILGRIM reserves all present and future moral rights in all intellectual property in the designs, the documents, drawings and any works executed or to be executed from them. PILGRIM by agreement grants the client a license to use the documents and drawings to produce the project, for which they were intended, conditional upon the following: - the license applies only to the site or that part of the site to which the design relates. - PILGRIM has completed the particular stage or stages of design service for which PILGRIM has been commissioned. - fees properly due to the designer have been paid in full. Do not scale from drawings, verify all dimensions prior to commencement of construction or fabrication, notify the designer of any discrepancies.			CHECK BY :		CA	
			DRAWING NO: A-04-04			
			DATE		18-02-2026	REV

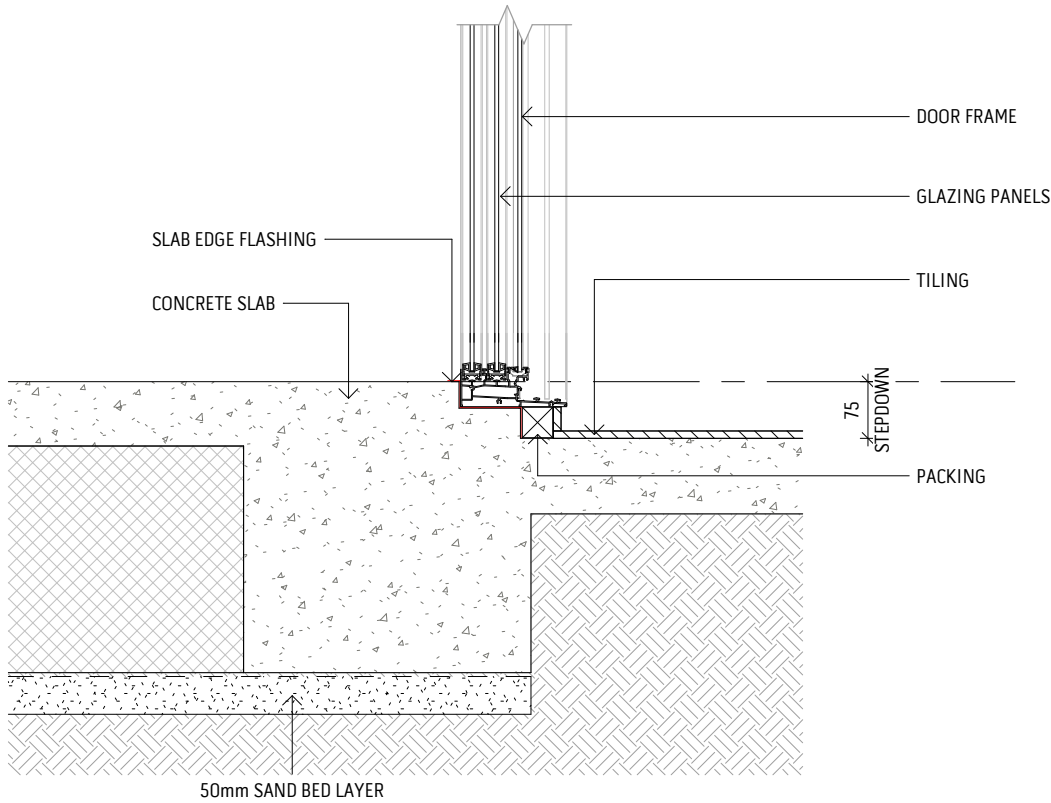


1 / **ALFRESCO SLIDING DOOR - DETAIL**
SCALE 1 : 10

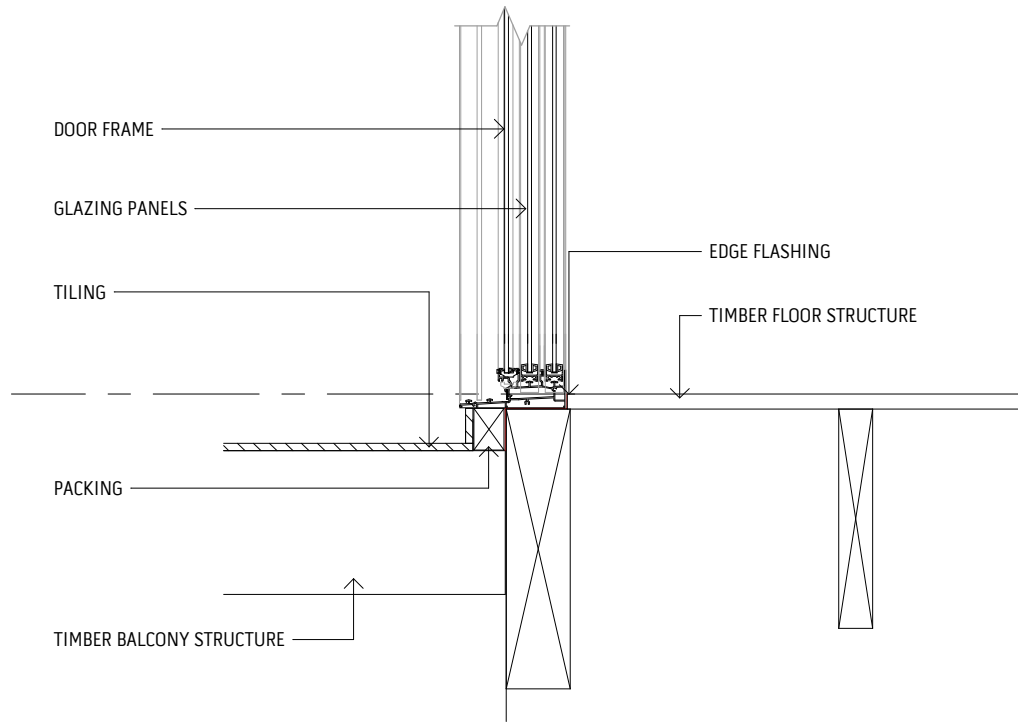

3 / **BALCONY SLIDING DOOR - DETAIL**
SCALE 1 : 10

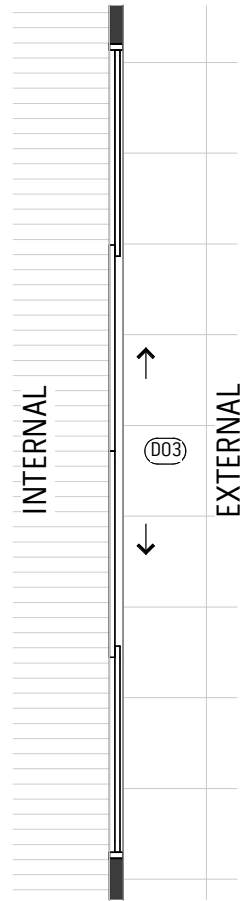

2 / **ALFRESCO SLIDING DOOR - CALLOUT**
SCALE 1 : 50

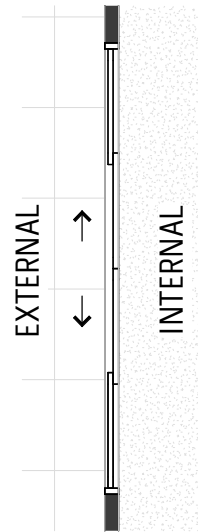


4 / **BALCONY SLIDING DOOR - CALLOUT**
SCALE 1 : 50


DATE	DESCRIPTION	REV. NO.	DRAWING TITLE :		SCALE :		As indicated	
03-02-2026	TECHNICAL UPDATES	H	SECTION DETAILS		MADELEINE & NICHOLAS CHILDS		PILGRIM[®]	
10-02-2026	TECHNICAL UPDATES	I						
18-02-2026	CONSTRUCTION REVIEW	J						
PILGRIM retains copyright in all documents and drawings and in any works executed from those documents and drawings. The PILGRIM reserves all present and future moral rights in all intellectual property in the designs, the documents, drawings and any works executed or to be executed from them. PILGRIM by agreement grants the client a license to use the documents and drawings to produce the project, for which they were intended, conditional upon the following: - the license applies only to the site or that part of the site to which the design relates. - PILGRIM has completed the particular stage or stages of architectural service for which PILGRIM has been commissioned. - fees properly due to the designer have been paid in full. Do not scale from drawings, verify all dimensions prior to commencement of construction or fabrication, notify the designer of any discrepancies.			106 HAROLD STREET, HOLLAND PARK		DRAWN : TH		CHECK BY : CA	
					DRAWING NO: A-04-05			
					DATE	18-02-2026	REV	J

ELEVATION PLAN NOTES:

- ALL EXTERNAL WALL FINISHES AND MATERIALS TO BE INSTALLED PER MANUFACTURE INSTRUCTIONS
- ROOF PITCH, FLASHING AND GUTTERING TO COMPLY WITH AS 3500.3 AND ROOFING MANUFACTURE REQUIREMENTS
- EXTERNAL CLADDING JUNCTIONS TO BE SEALED TO MANUFACTURE SPECIFICATIONS
- GLAZING PERFORMANCE TO COMPLY WITH ENERGY REPORT

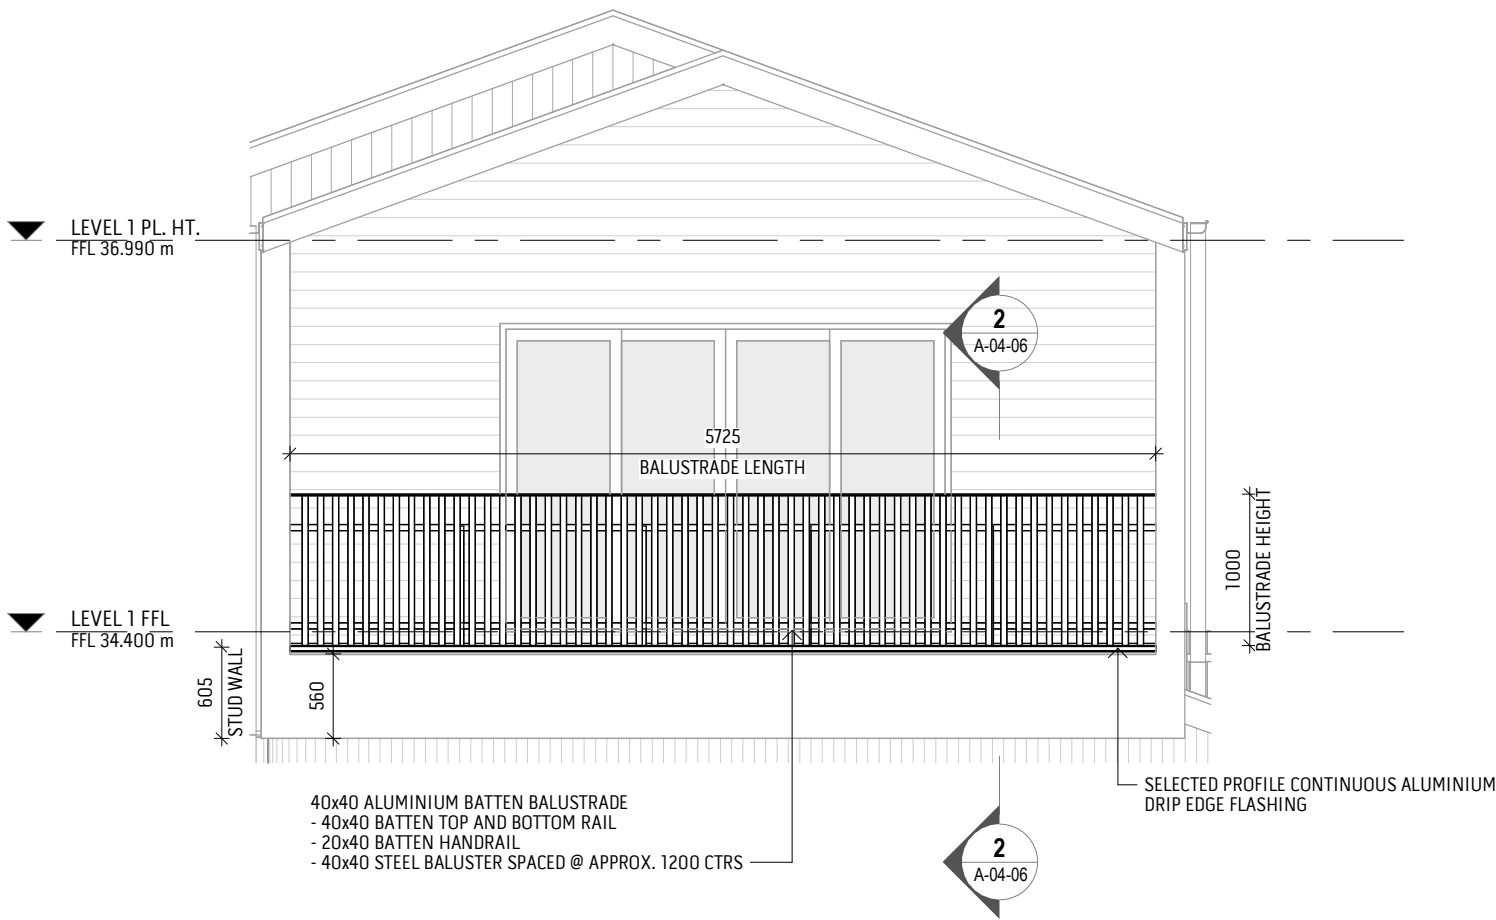


1 / BALUSTRADE DETAIL
SCALE 1 : 50

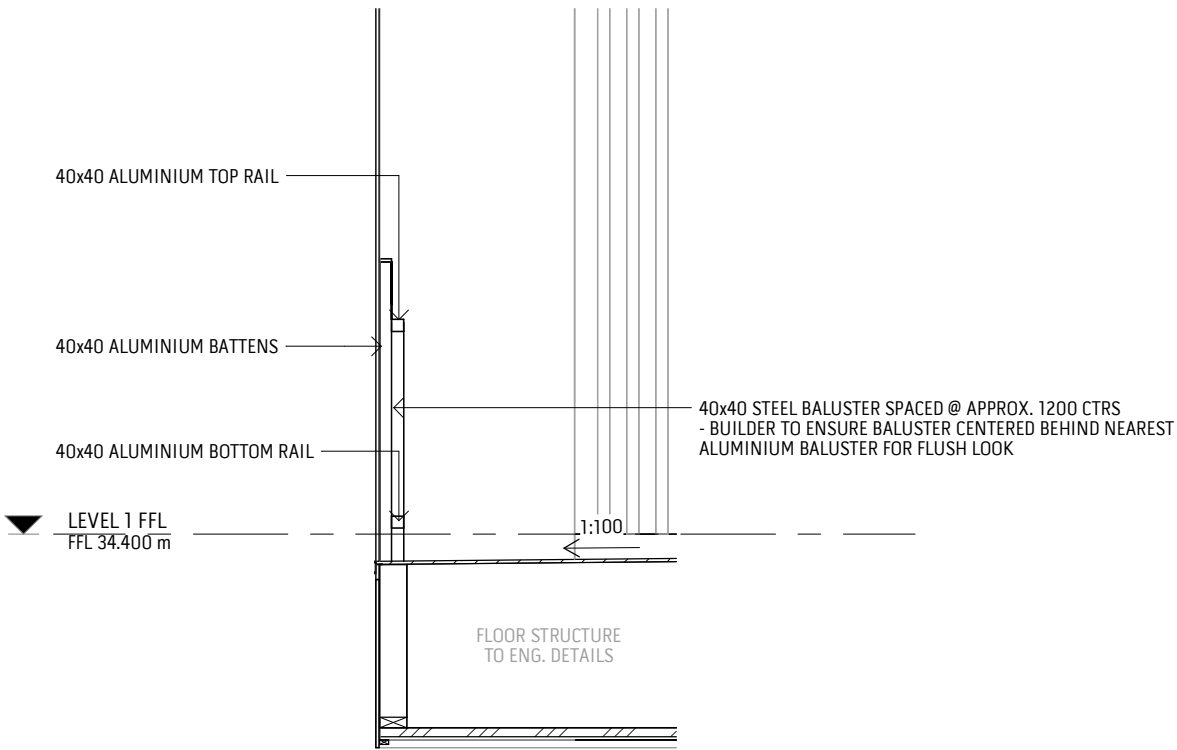


2 / BALUSTRADE SECTION
SCALE 1 : 25


DATE	DESCRIPTION	REV. NO.	DRAWING TITLE :		SCALE :	
03-02-2026	TECHNICAL UPDATES	H	FACADE CALLOUT	MADELEINE & NICHOLAS CHILDS	As indicated	
10-02-2026	TECHNICAL UPDATES	I			ABN: 89 639 943 187	
18-02-2026	CONSTRUCTION REVIEW	J			QBCC: 1523 8743	
PILGRIM retains copyright in all documents and drawings and in any works executed from those documents and drawings. The PILGRIM reserves all present and future moral rights in all intellectual property in the designs, the documents, drawings and any works executed or to be executed from them. PILGRIM by agreement grants the client a license to use the documents and drawings to produce the project, for which they were intended, conditional upon the following: - the license applies only to the site or that part of the site to which the design relates. - PILGRIM has completed the particular stage or stages of design service for which PILGRIM has been commissioned. - fees properly due to the designer have been paid in full. Do not scale from drawings, verify all dimensions prior to commencement of construction or fabrication, notify the designer of any discrepancies.			106 HAROLD STREET, HOLLAND PARK		PILGRIM®	
					DRAWING NO: A-04-06	
					DRAWN : TH CHECK BY : CA	
					DATE 18-02-2026 REV J	

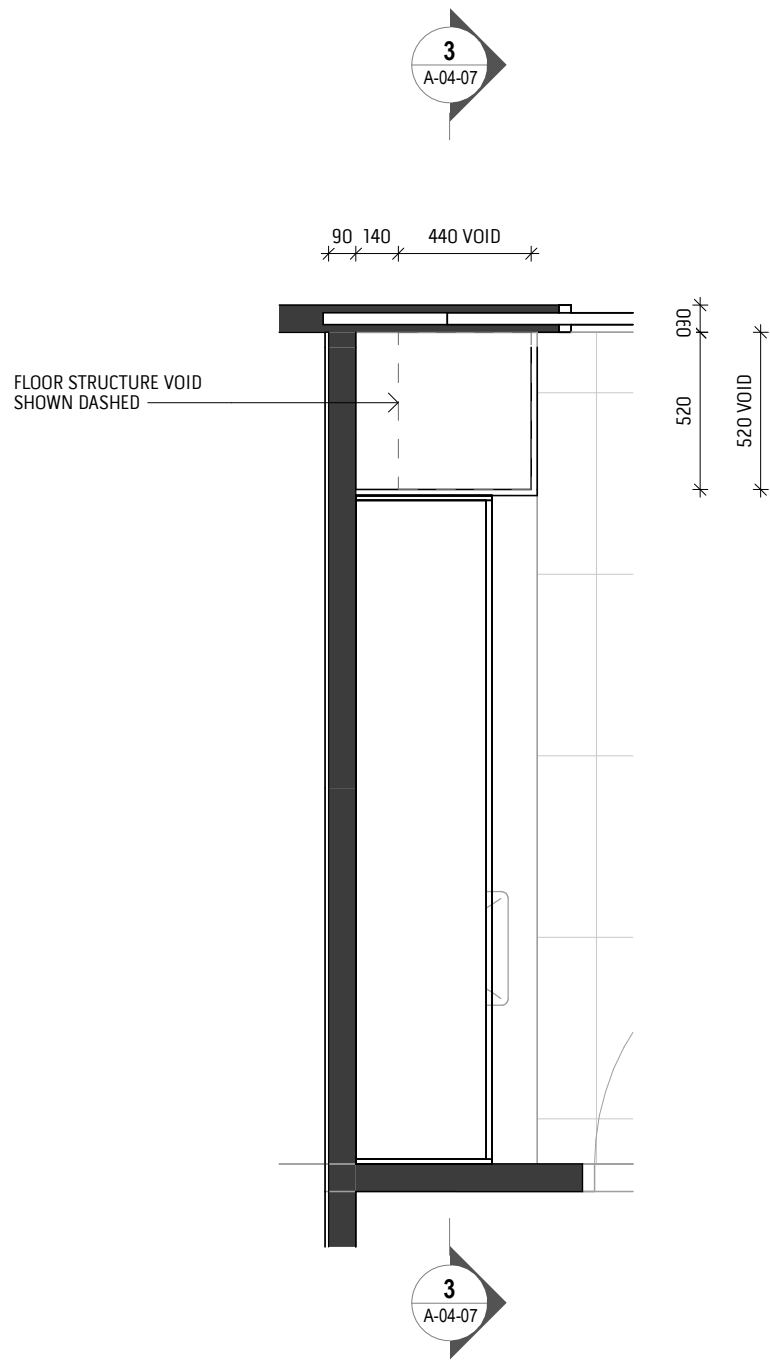

1 / A-03-01 / LAUNDRY CHUTE GROUND SCALE 1 : 25

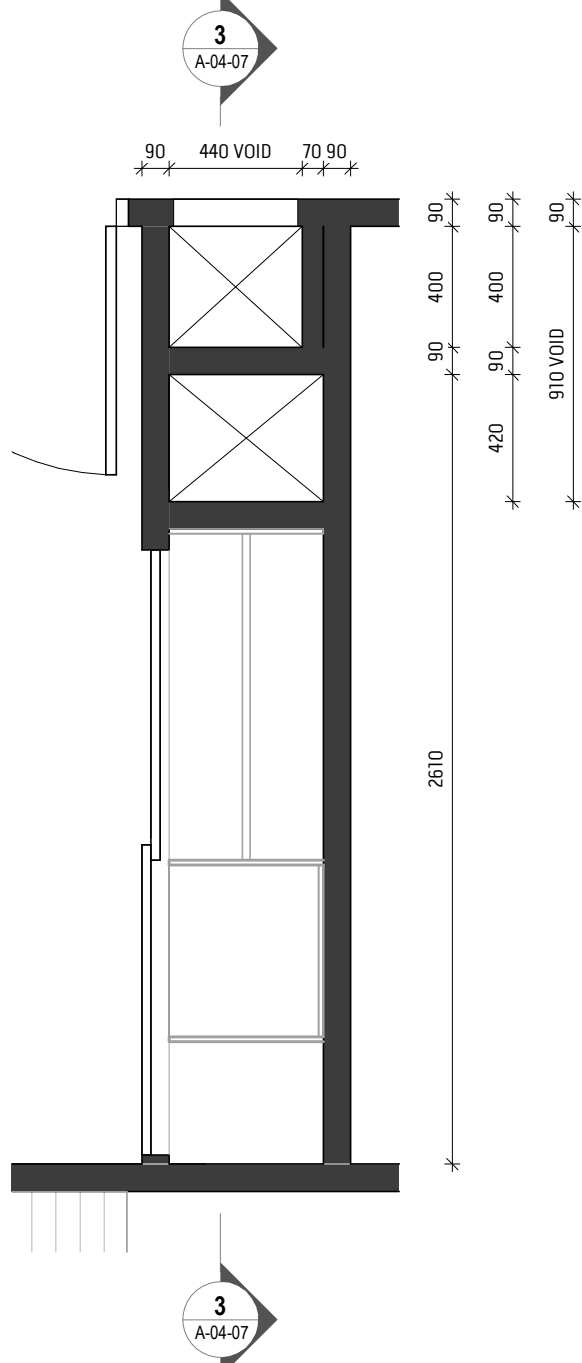

2 / A-03-01 / LAUNDRY CHUTE LEVEL 1 SCALE 1 : 25

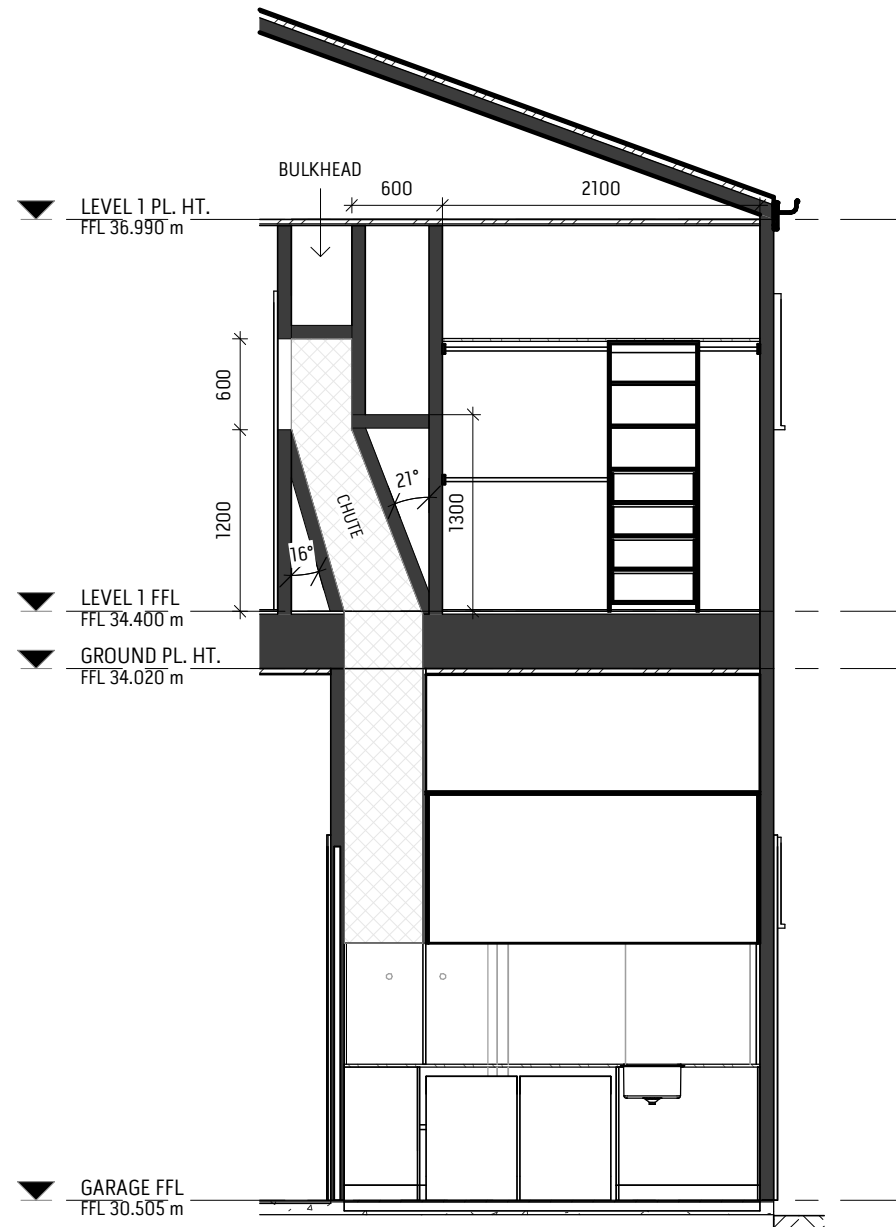

3 / A-04-07 / LAUNDRY CHUTE - SECTION SCALE 1 : 50

DATE		DESCRIPTION	REV. NO.	DRAWING TITLE :		SCALE :	
03-02-2026		TECHNICAL UPDATES	H	LAUNDRY CHUTE		As indicated	
10-02-2026		TECHNICAL UPDATES	I				
18-02-2026		CONSTRUCTION REVIEW	J				
PILGRIM retains copyright in all documents and drawings and in any works executed from those documents and drawings. The PILGRIM reserves all present and future moral rights in all intellectual property in the designs, the documents, drawings and any works executed or to be executed from them. PILGRIM by agreement grants the client a license to use the documents and drawings to produce the project, for which they were intended, conditional upon the following: - the license applies only to the site or that part of the site to which the design relates, - PILGRIM has completed the particular stage or stages of architectural service for which PILGRIM has been commissioned, - fees properly due to the designer have been paid in full. Do not scale from drawings, verify all dimensions prior to commencement of construction or fabrication, notify the designer of any discrepancies.				MADELEINE & NICHOLAS CHILDS		PILGRIM®	
				106 HAROLD STREET, HOLLAND PARK			
				DRAWN : TH		CHECK BY : CA	
						DRAWING NO: A-04-07	
				DATE 18-02-2026		REV	J

1. GENERAL

- ALL SITE DIMENSIONS TO BE CHECKED PRIOR TO PREPARATION OF SHOP DRAWINGS AND MANUFACTURE
- ALL WORKS TO COMPLY WITH THE NCC, CONTROLLING AUTHORITIES' REQUIREMENTS, AND MANUFACTURE'S FIXING DETAILS AND REQUIREMENTS WHERE NOT COVERED BY REGULATIONS
- CONTRACTOR TO REFER TO MANUFACTURER'S SPECIFICATIONS OF ALL EQUIPMENT, FIXTURES AND FITTINGS PRIOR TO PREPARATION OF SHOP DRAWINGS AND MANUFACTURE. ALL INSTALLATION SHALL BE TO MANUFACTURER'S INSTRUCTION TO ENSURE ALL EQUIPMENT, FIXTURES AND FITTING WARRANTIES
- ALL APPLIANCES TO ACHIEVE MANUFACTURER'S VENTILATION REQUIREMENTS
- PROVIDE TYPICAL 20mm RECESSED SHADOWLINE TO ALL JOINERY ADJACENT TO CEILINGS, BULKHEADS AND WALLS
- CONFIRM HEIGHT CLEARANCE BETWEEN COOKTOP AND EXHAUST FANS MEET GAS AUTHORITIES' REQUIREMENTS, AUSTRALIAN STANDARDS AND MANUFACTURER'S RECOMMENDATIONS. APPLY WHICHEVER DIMENSION IS GREATEST
- CONFIRM ALL CUT-OUT DIMENSIONS FOR JOINERY UNITS WITH CLIENT PRIOR TO CONSTRUCTION
- GAS BURNERS TO BE MIN. 200mm SPLASHBACK
- PROVIDE NOGGINGS WITHIN WALL CAVITY FOR TOWEL RAIL AND OTHER ACCESSORY FIXINGS
- CONTRACTOR TO BE ADVISE OF ANY DISCREPANCY OR VARIATION IN NOMINATED DIMENSIONS ON DRAWINGS

2. DOORS, DRAWER FRONTS & EXTERNAL PANELS

- WHERE NOMINATED, TO BE LAMINATED BOARD SHALL BE CONSTRUCTED FROM 16mm PARTICLEBOARD WITH MATCHING EDGE STRIPS
- WHERE NOMINATED, AS 2 PACK PAINT FINISH SHALL BE CONSTRUCTED FROM 16mm MDF BOARD

3. INTERNAL CARCASS

- SHALL BE CONSTRUCTED FROM WHITE 16mm MELAMINE HMR PARTICLE BOARD WITH MATCHING SQUARE SELF EDGE STRIPPING UNLESS NOMINATED OTHERWISE

4. DRAWER CARCASS

- SHALL BE CONSTRUCTED OF 16mm WHITE MELAMINE BOARD OR PROPRIETY POWDERCOATED METAL, WHITE POWDERCOAT FINISH UNLESS NOMINATED OTHERWISE

5. SHELVES

- SHALL BE CONSTRUCTED OF 16mm MELAMINE WITH MATCHING SQUARE SELF EDGE STRIPPING MAX SPAN 900mm

6.HARDWARE

- ALLOW FOR 2NO. HINGES PER DOOR FOR UNDER BENCH AND OVERHEAD DOORS
- ALLOW FOR 4NO. HINGES PER DOOR TO PANTRY AND CUPBOARDS
- HINGES SHALL BE BLUM SOFT CLOSING, ALL METAL, FULL CONCEALED HINGES
- HINGES SHALL BE GENERALLY 180° OPENING, EXCEPT WHERE 180° OPENING NOT POSSIBLE
- PROVIDE WHITE POWDERCOAT METAL FULL EXTENSION DRAWER RUNNERS WITH BLUM SOFT CLOSING
- PROVIDE CUTLERY TRAY INSERT TO DRAWER NOMINATED 'CUTLERY'
- ALL INTERNAL ADJUSTABLE SHELVES TO BE SUPPORTED ON WHITE OR CLEAR PLASTIC FERRULS

7. TILING

- ALL GROUT LINES TO BE MAX. 3mm

8. BENCHTOPS

- SHALL BE CONSTRUCTED OF 20mm STONE BENCHTOP ON 18MM HMR SUBSTRATE UNLESS NOMINATED AS WATERFALL, REFER CONSTRUCTION SPECIFICATION SCHEDULE FOR STONE SELECTION

9. WATER PROOFING

- WATER PROOFING TO WALLS AND FLOORS TO WET AREAS TO BE PROVIDED WHERE REQUIRED BY CLAUSE F1.7 IN ACCORDANCE WITH AS3740

FINISHES LEGEND

REFER TO CONSTRUCTION SPECIFICATION SCHEDULE FOR DETAILED DESCRIPTION OF FINISHES AND FIXTURES (NUMBER ADDED TO SYMBOL TO DIFFERENTIATE SELECTION)

L	LAMINATE
S	STONE
IP	INTERIOR PAINT
T	TILE
2P	2PAC
TF	TIMBER FLOOR
C	CARPET
PC	POWDER COAT
CW	CARCASS WHITE MELAMINE

DW	DISHWASHER
CT	COOKTOP
RG	RANGEHOOD
OV	OVEN

FIXTURES & FITTINGS

BN	BIN
MX	MIXER
SK	SINK
BA	BASIN
BT	BATH
MR	MIRROR
SR	SHOWER RAIL
TW	TOWEL RAIL
HT	HAND TOWEL RAIL/HOOK
RH	ROBE HOOK
TP	TOILET PAN
TR	TOILET ROLL HOLDER
WA	WALL ANGLE TRIM
FW	FLOOR WASTE
WO	WASHING MACHINE STOPS

H	HANDLE
---	--------

DATE	DESCRIPTION	REV. NO.	DRAWING TITLE : FIXED JOINERY NOTES 106 HAROLD STREET, HOLLAND PARK		MADELEINE & NICHOLAS CHILDS		PILGRIM [®]		SCALE :	
03-02-2026	TECHNICAL UPDATES	H								
10-02-2026	TECHNICAL UPDATES	I								
18-02-2026	CONSTRUCTION REVIEW	J								
PILGRIM retains copyright in all documents and drawings and in any works executed from those documents and drawings. The PILGRIM reserves all present and future moral rights in all intellectual property in the designs, the documents, drawings and any works executed or to be executed from them. PILGRIM by agreement grants the client a license to use the documents and drawings to produce the project, for which they were intended, conditional upon the following: - the license applies only to the site or that part of the site to which the design relates, - PILGRIM has completed the particular stage or stages of architectural service for which PILGRIM has been commissioned, - fees properly due to the designer have been paid in full. Do not scale from drawings, verify all dimensions prior to commencement of construction or fabrication, notify the designer of any discrepancies.									DRAWN : TH CHECK BY : CA	
									DRAWING NO: A-05-00	
									DATE 18-02-2026	REV J



PILGRIM retains copyright in all documents and drawings and in any works executed from those documents and drawings. The PILGRIM reserves all present and future moral rights in all intellectual property in the designs, the documents, drawings and any works executed or to be executed from them.

PILGRIM by agreement grants the client a license to use the documents and drawings to produce the project, for which they were intended, conditional upon the following:




- the license applies only to the site or that part of the site to which the design relates
- PILGRIM has completed the particular stage or stages of architectural service for which PILGRIM has been commissioned
- fees payable to the designer have been paid in full.

Do not scale from drawings, verify all dimensions prior to commencement of construction or fabrication, notify the designer of any discrepancies.

106 HAROLD STREET, HOLLAND PARK

PILGRIM®

SCALE :	1:50		
DRAWN :	TH	CHECK BY :	CA
DRAWING NO:	A-05-01		
DATE	18-02-2026	REV	J

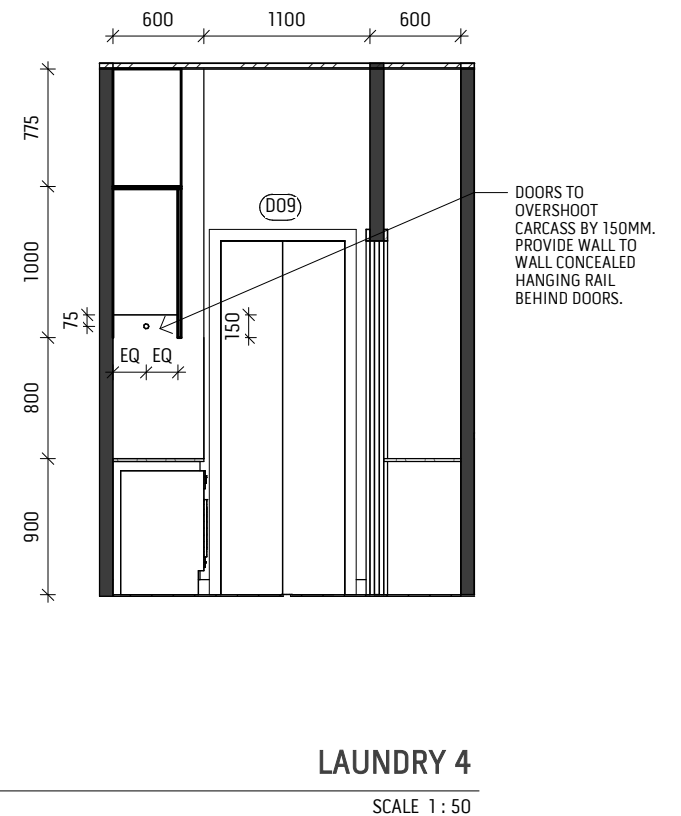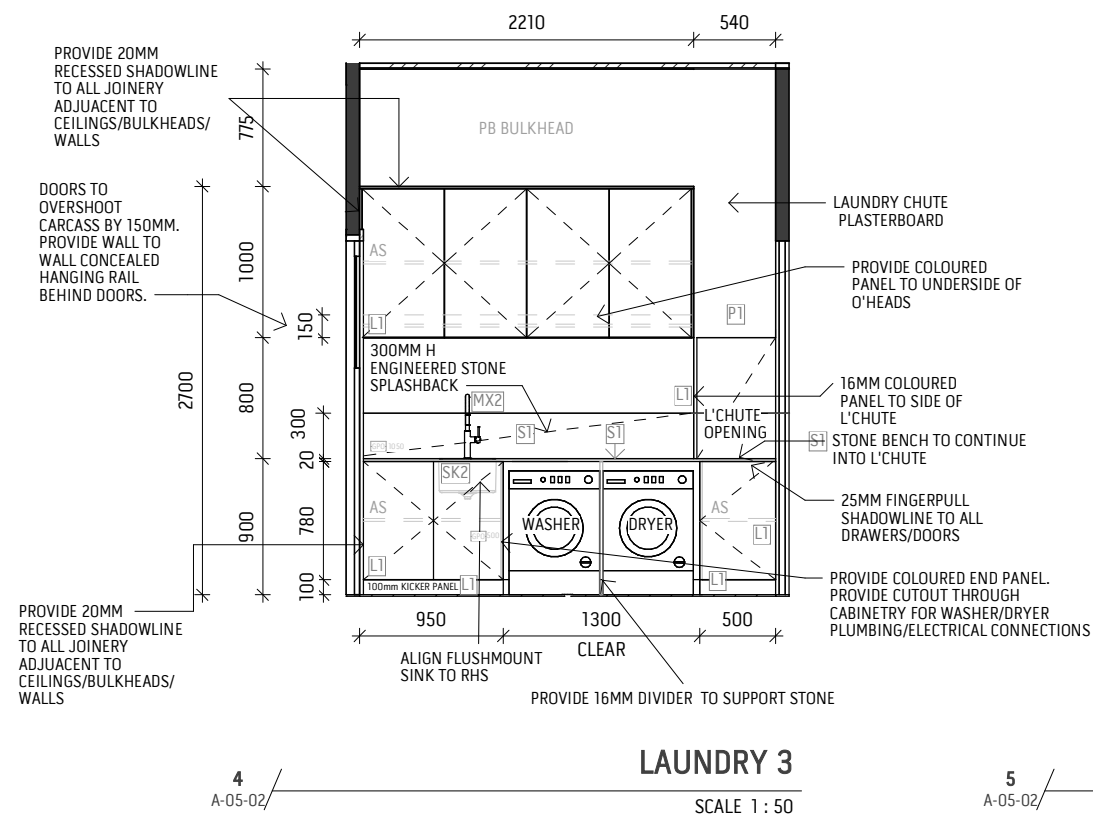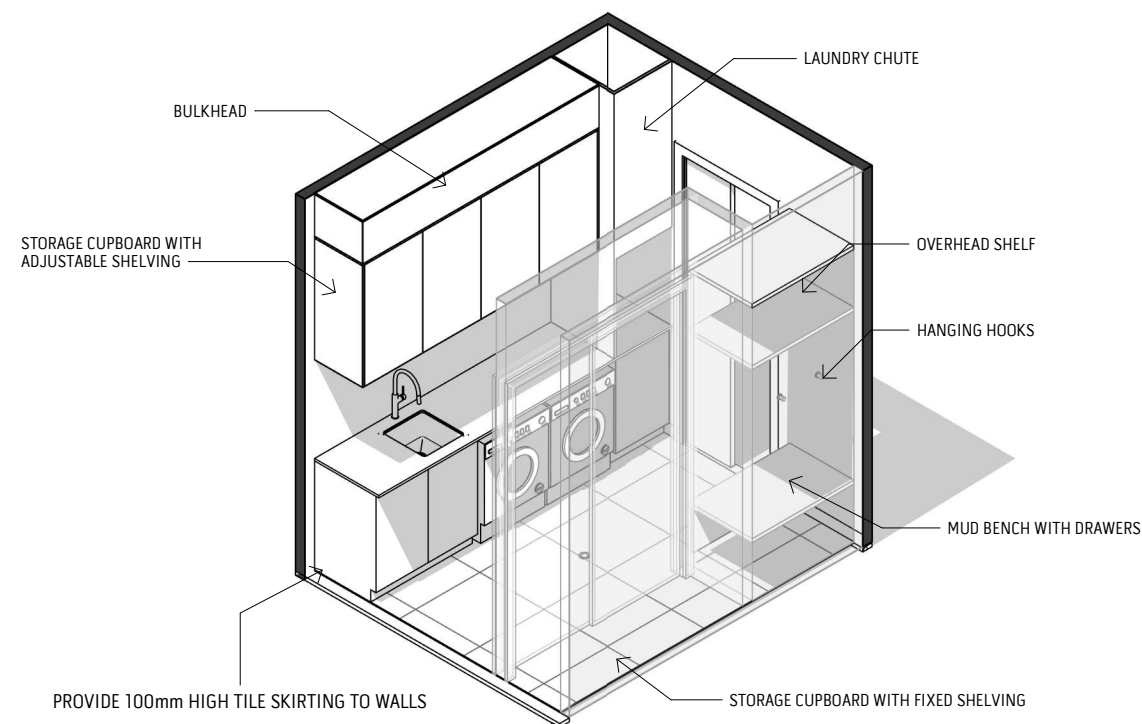

DATE	DESCRIPTION	REV. NO.
03-02-2026	TECHNICAL UPDATES	H
10-02-2026	TECHNICAL UPDATES	I
18-02-2026	CONSTRUCTION REVIEW	J

PILGRIM retains copyright in all documents and drawings and in any works executed from those documents and drawings. The PILGRIM reserves all present and future moral rights in all intellectual property in the designs, the documents, drawings and any works executed or to be executed from them.

PILGRIM by agreement grants the client a license to use the documents and drawings to produce the project, for which they were intended, conditional upon the following:

- the license applies only to the site or that part of the site to which the design relates.
- PILGRIM has completed the particular stage or stages of architectural service for which PILGRIM has been commissioned.
- the client pays the design fees to PILGRIM in full.

Do not scale from drawings, verify all dimensions prior to commencement of construction or fabrication, notify the designer of any discrepancies.

DRAWING TITLE :

INTERNALS - LAUNDRY

MADELEINE & NICHOLAS CHILDS

106 HAROLD STREET, HOLLAND PARK

PILGRIM[®]







SCALE: 1:50

DRAWN: TH CHECK BY: CA

DRAWING NO: A-05-02







DATE 18-02-2026

	1
--	---

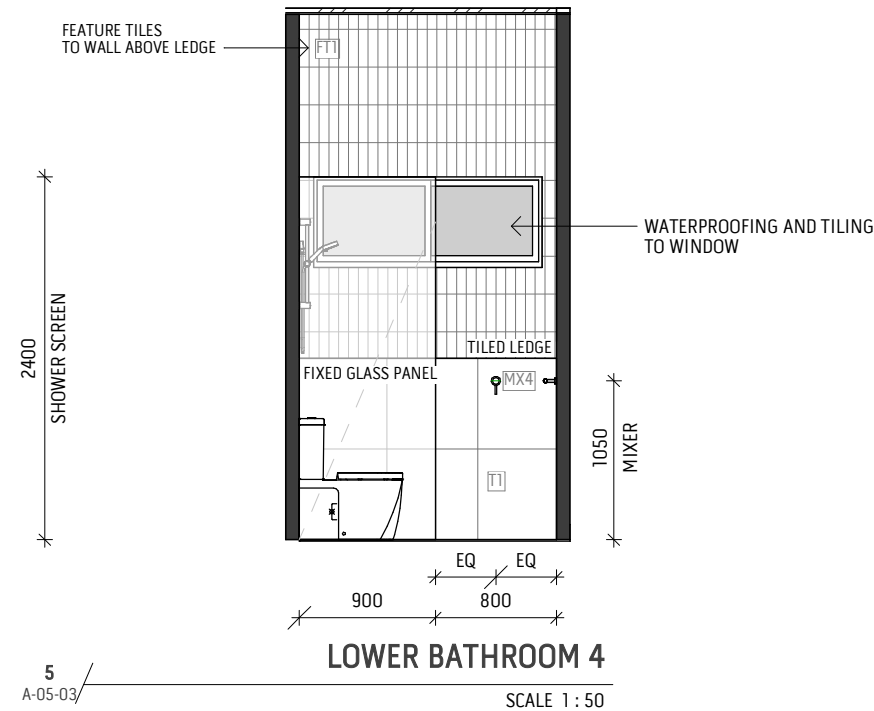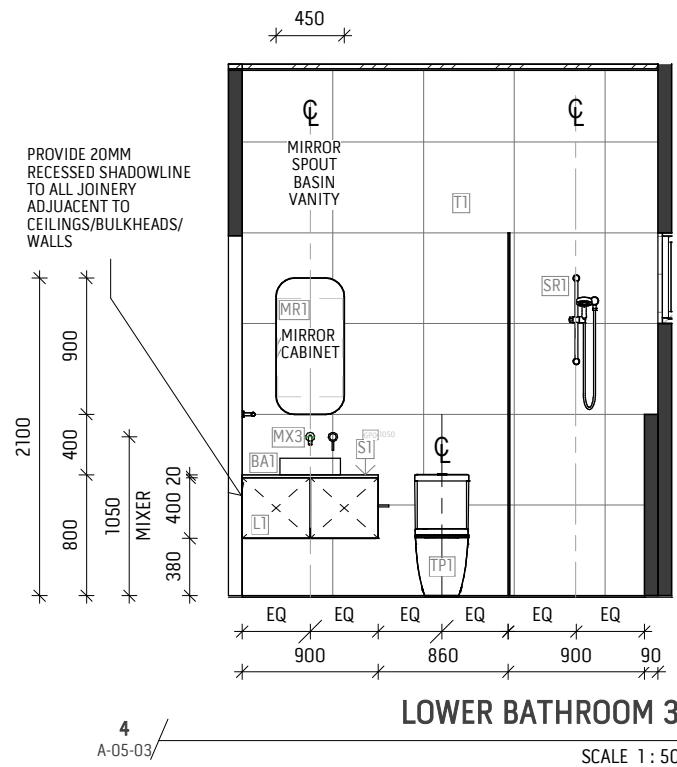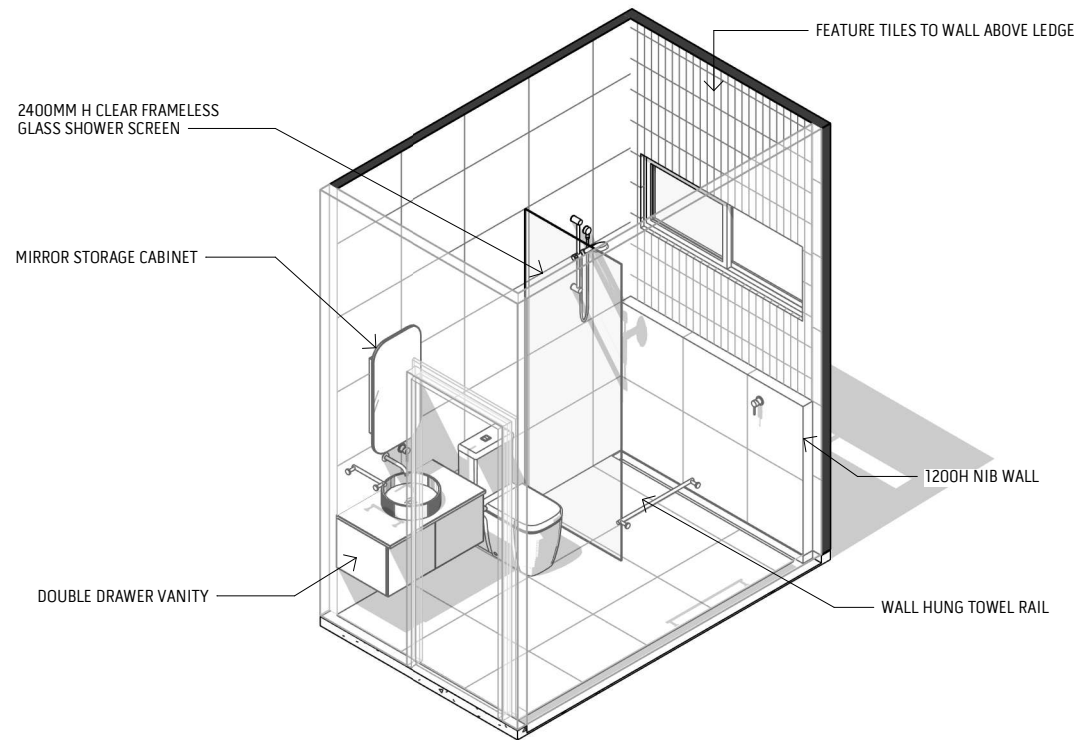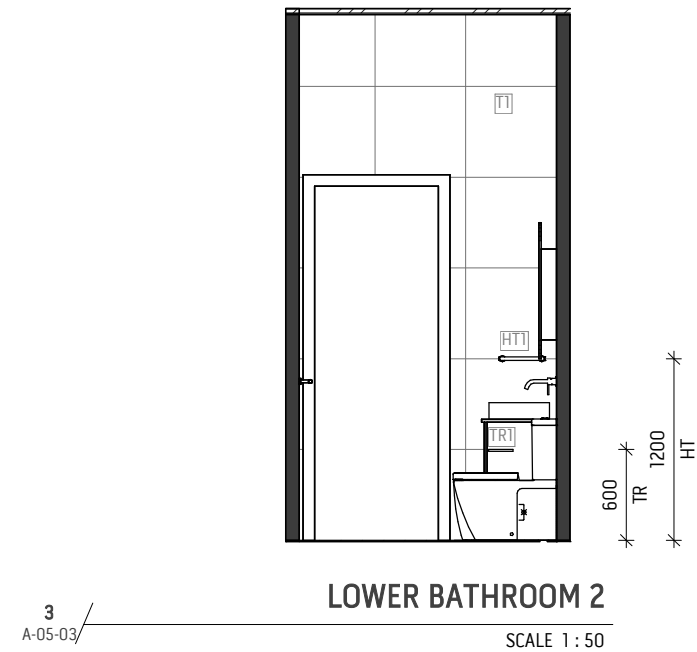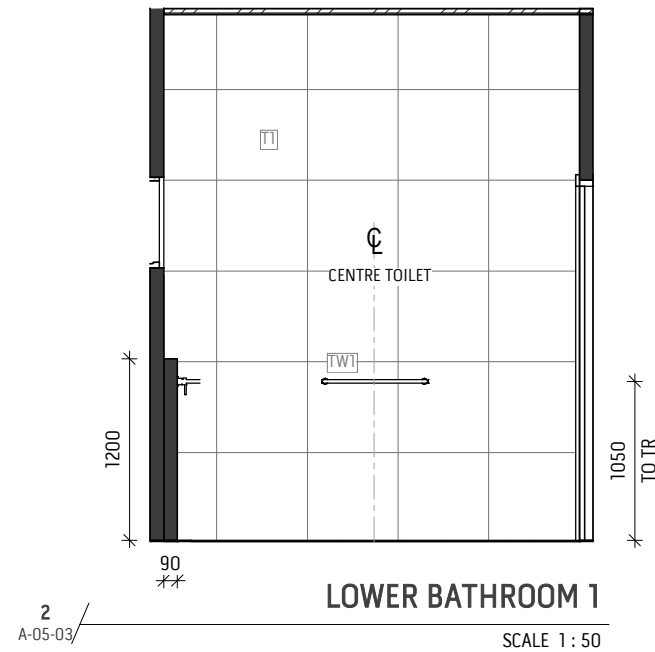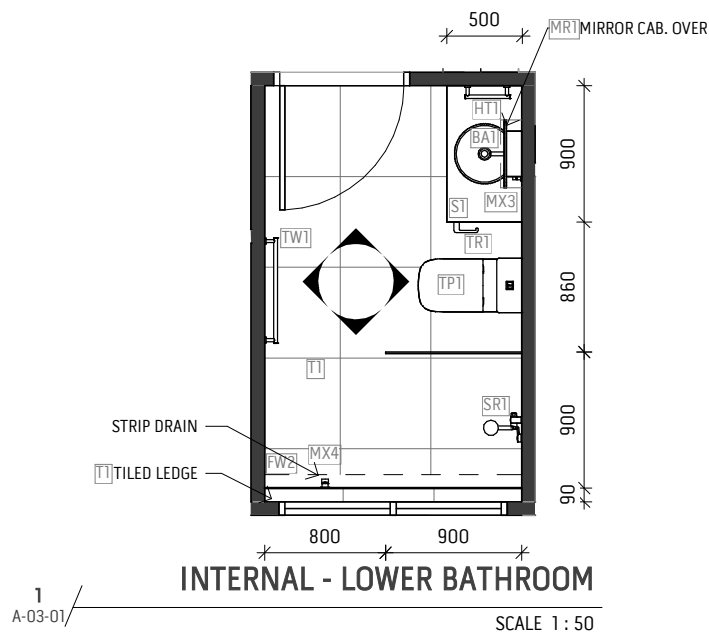

DATE	DESCRIPTION	REV. NO.	DRAWING TITLE :		SCALE :					
03-02-2026	TECHNICAL UPDATES	H	INTERNALS - LOWER BATHROOM		1:50					
10-02-2026	TECHNICAL UPDATES	I								
18-02-2026	CONSTRUCTION REVIEW	J								
PILGRIM retains copyright in all documents and drawings and in any works executed from those documents and drawings. The PILGRIM reserves all present and future moral rights in all intellectual property in the designs, the documents, drawings and any works executed or to be executed from them. PILGRIM by agreement grants the client a license to use the documents and drawings to produce the project, for which they were intended, conditional upon the following: - the license applies only to the site or that part of the site to which the design relates. - PILGRIM has completed the particular stage or stages of architectural service for which PILGRIM has been commissioned. - fees properly due to the designer have been paid in full. Do not scale from drawings, verify all dimensions prior to commencement of construction or fabrication, notify the designer of any discrepancies.			DRAWING NO: A-05-03		DATE	18-02-2026	REV	J		
			106 HAROLD STREET, HOLLAND PARK		DRAWN : TH		CHECK BY : CA			
			MADELEINE & NICHOLAS CHILDS							

PILGRIM®

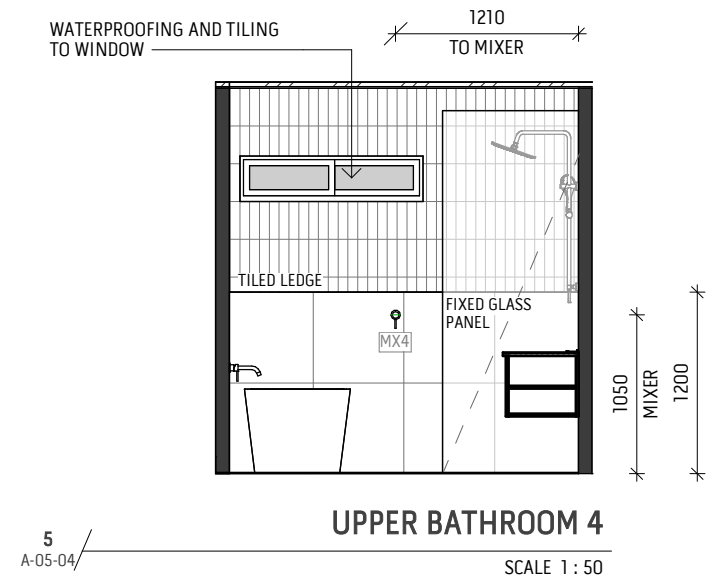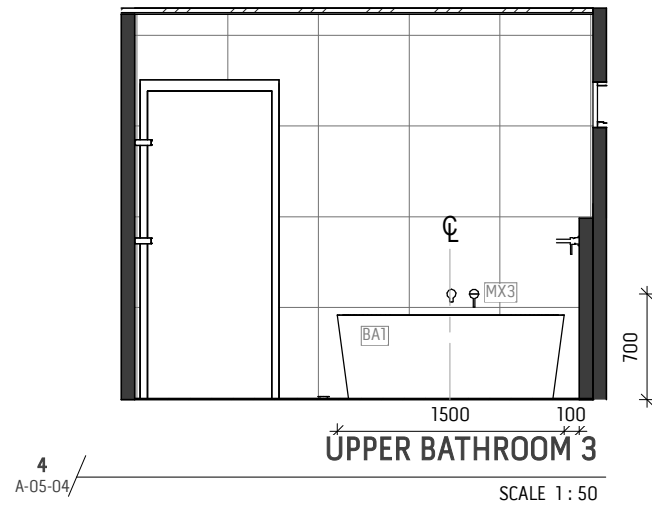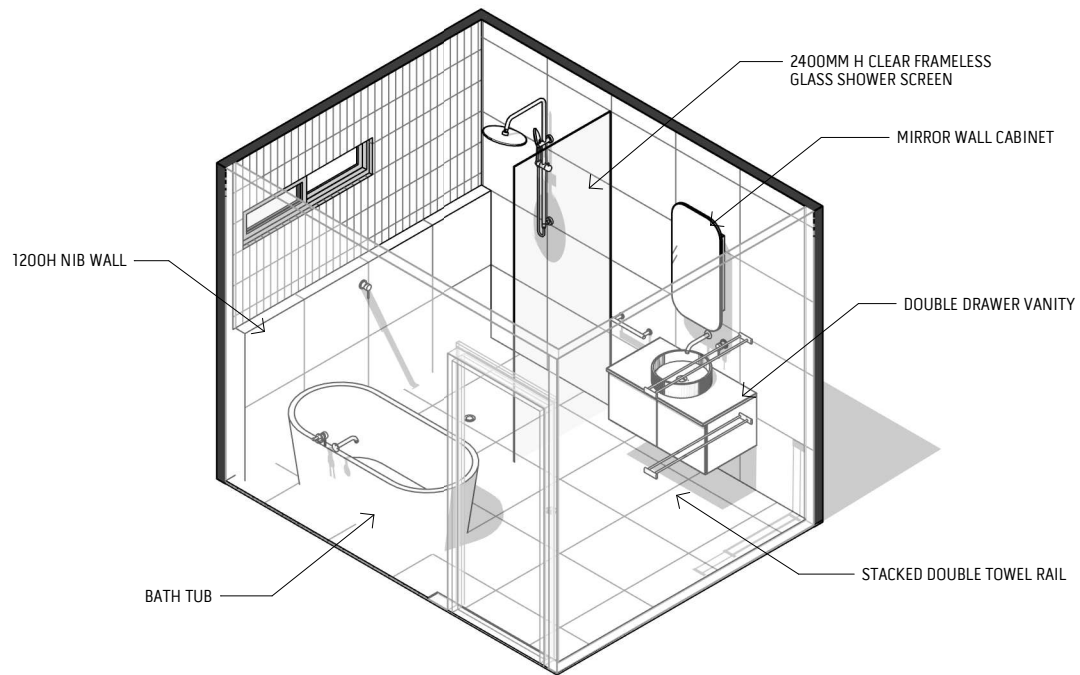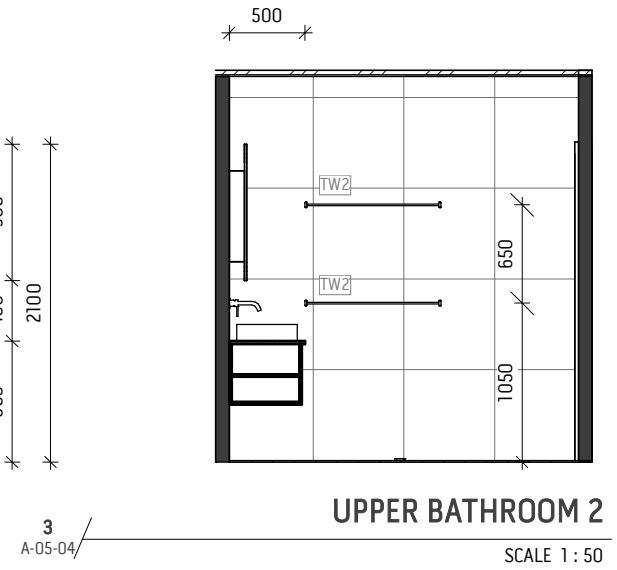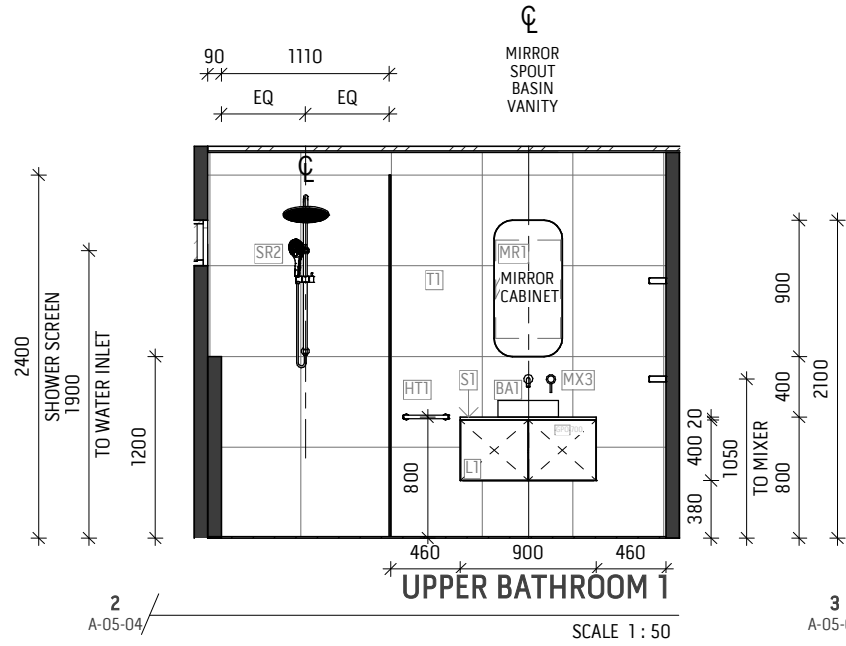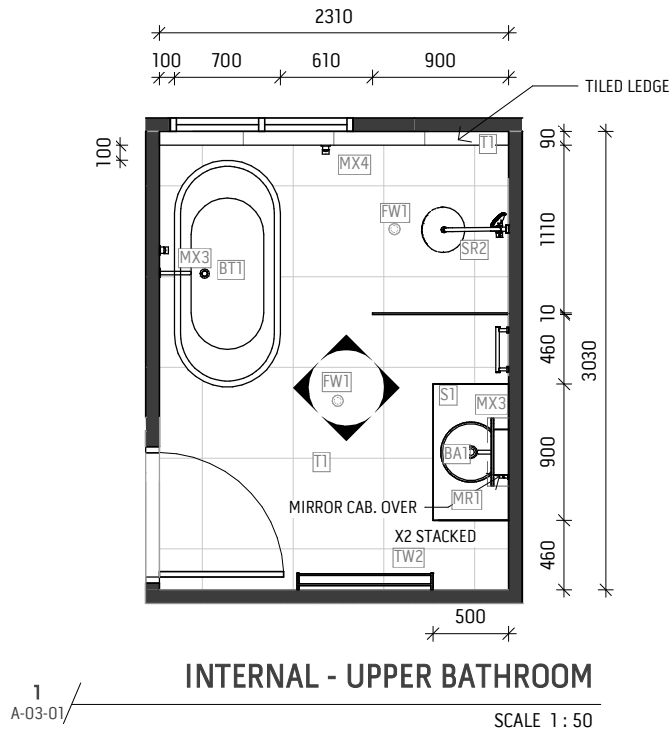


DATE	DESCRIPTION	REV. NO.	DRAWING TITLE :		SCALE :	
03-02-2026	TECHNICAL UPDATES	H	INTERNALS - UPPER BATHROOM		1 : 50	
10-02-2026	TECHNICAL UPDATES	I				
18-02-2026	CONSTRUCTION REVIEW	J				
PILGRIM retains copyright in all documents and drawings and in any works executed from those documents and drawings. The PILGRIM reserves all present and future moral rights in all intellectual property in the designs, the documents, drawings and any works executed or to be executed from them. PILGRIM by agreement grants the client a license to use the documents and drawings to produce the project, for which they were intended, conditional upon the following: - the license applies only to the site or that part of the site to which the design relates, - PILGRIM has completed the particular stage or stages of architectural service for which PILGRIM has been commissioned, - fees properly due to the designer have been paid in full. Do not scale from drawings, verify all dimensions prior to commencement of construction or fabrication, notify the designer of any discrepancies.			DRAWING NO: A-05-04		DATE	18-02-2026
			REV		J	


MADELEINE & NICHOLAS CHILDS

106 HAROLD STREET, HOLLAND PARK


PILGRIM[®]

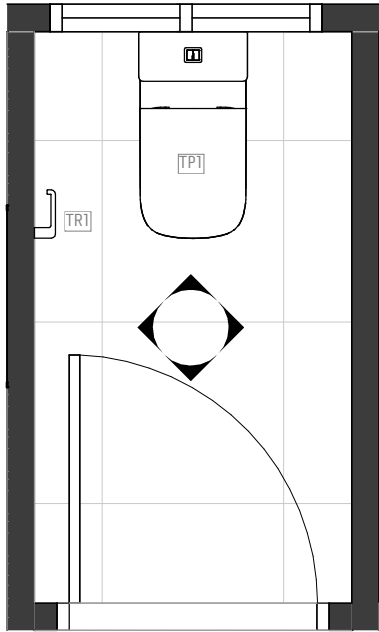


1
A-03-01/ INTERNAL - UPPER TOILET
SCALE 1 : 25

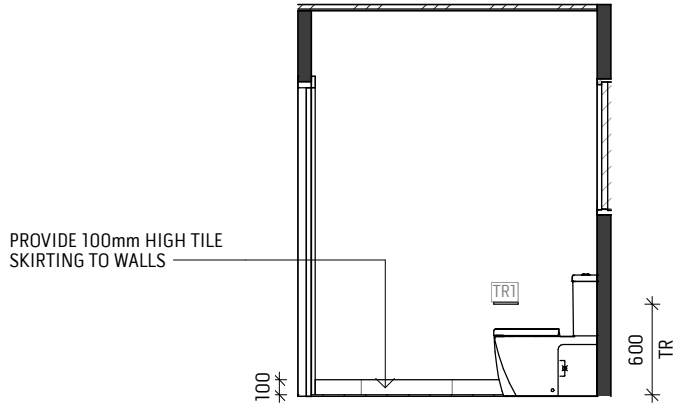


2
A-05-05/ UPPER TOILET 1
SCALE 1 : 50

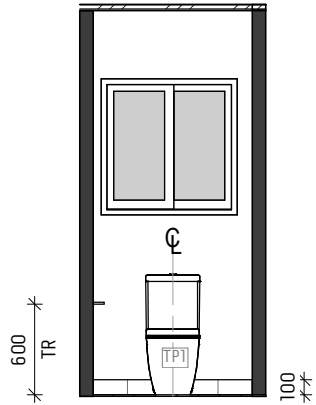


3
A-05-05/ UPPER TOILET 2
SCALE 1 : 50

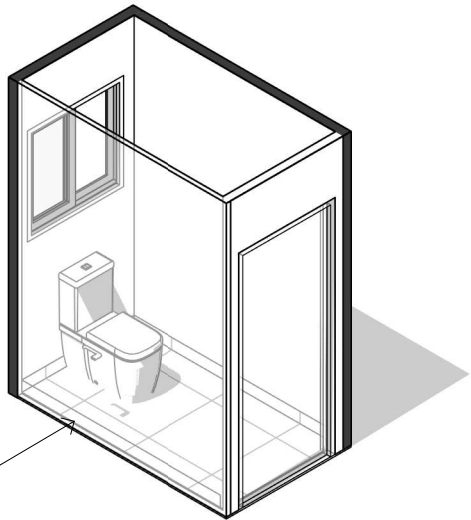

PROVIDE 100mm HIGH TILE SKIRTING TO WALLS






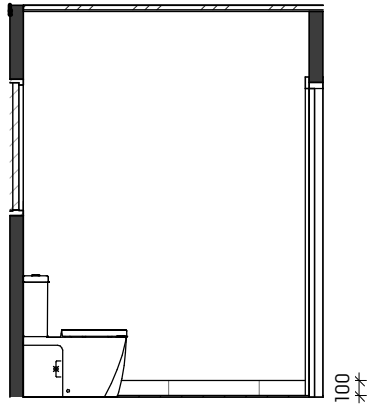


4
A-05-05/ UPPER TOILET 3
SCALE 1 : 50






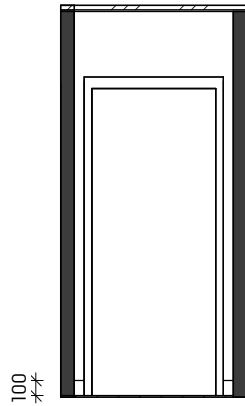


5
A-05-05/ UPPER TOILET 4
SCALE 1 : 50


DATE		DESCRIPTION	REV. NO.	DRAWING TITLE :		PILGRIM [®]	SCALE : As indicated	
03-02-2026		TECHNICAL UPDATES	H	INTERNALS - UPPER TOILET				
10-02-2026		TECHNICAL UPDATES	I					
18-02-2026		CONSTRUCTION REVIEW	J					
PILGRIM retains copyright in all documents and drawings and in any works executed from those documents and drawings. The PILGRIM reserves all present and future moral rights in all intellectual property in the designs, the documents, drawings and any works executed or to be executed from them. PILGRIM by agreement grants the client a license to use the documents and drawings to produce the project, for which they were intended, conditional upon the following: - the license applies only to the site or that part of the site to which the design relates, - PILGRIM has completed the particular stage or stages of architectural service for which PILGRIM has been commissioned, - fees properly due to the designer have been paid in full. Do not scale from drawings, verify all dimensions prior to commencement of construction or fabrication, notify the designer of any discrepancies.				106 HAROLD STREET, HOLLAND PARK			MADELEINE & NICHOLAS CHILDS	
						DRAWN : TH CHECK BY : CA		
						DRAWING NO: A-05-05		
DATE		18-02-2026		REV		J		

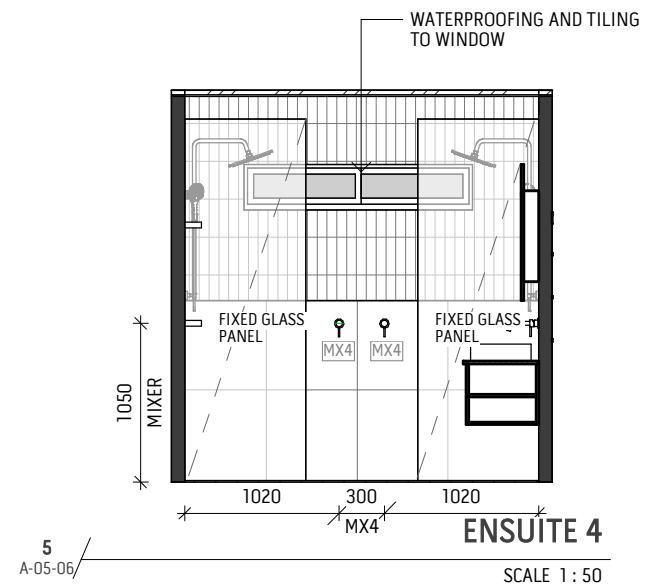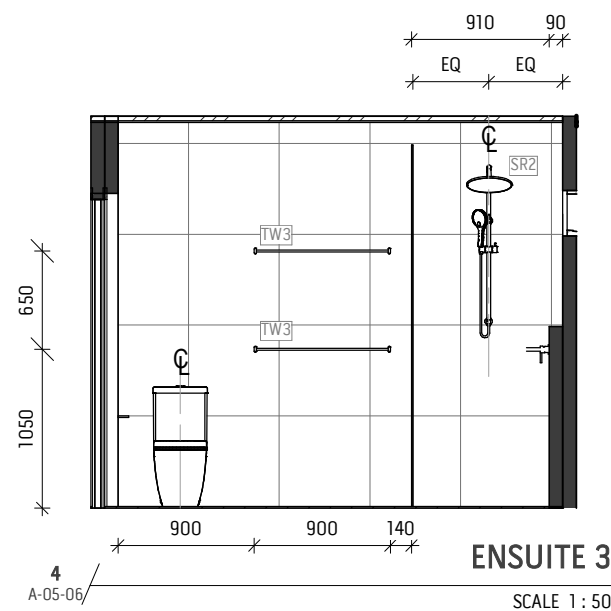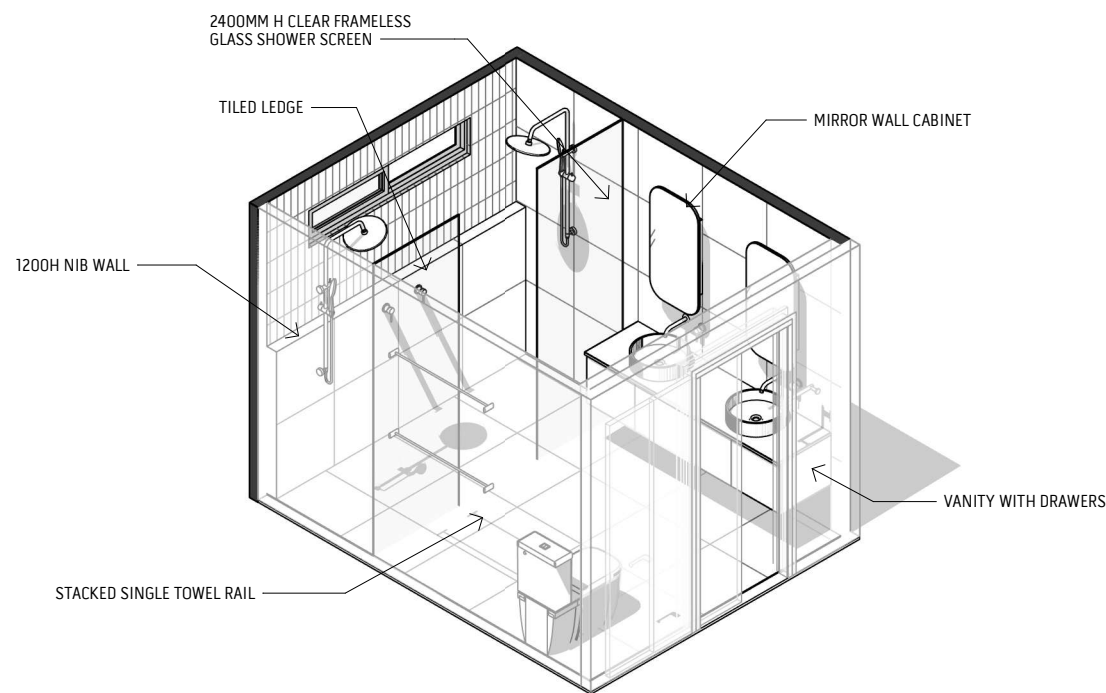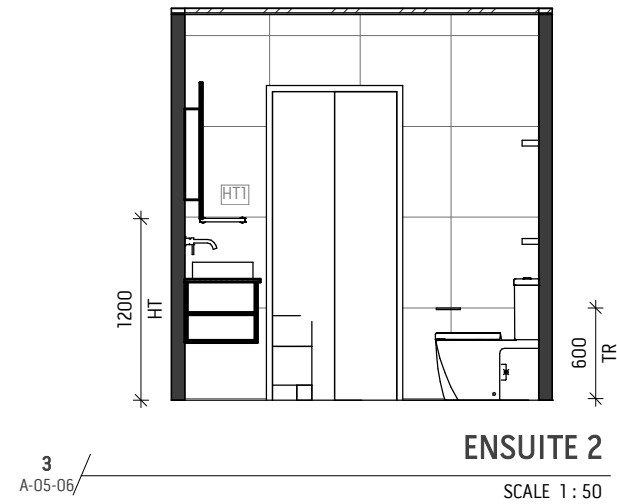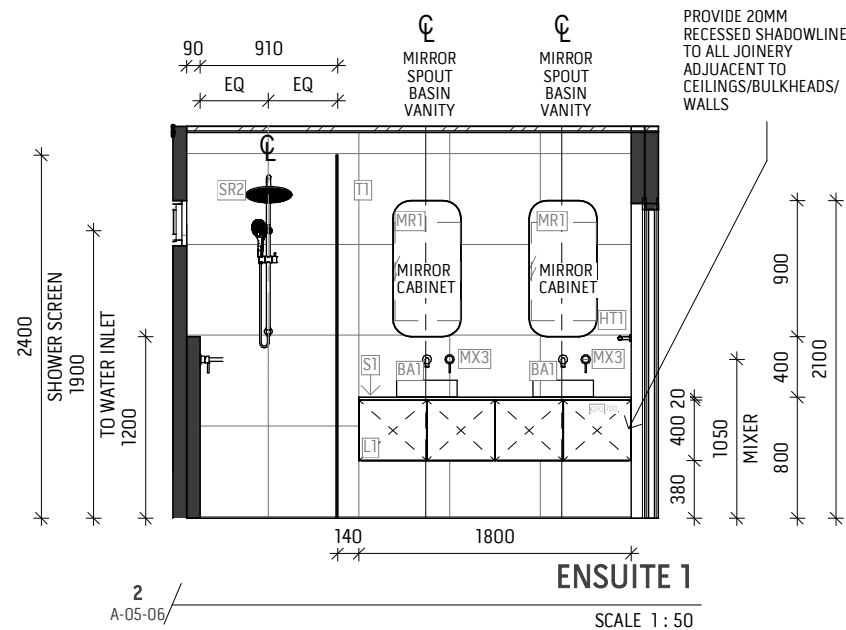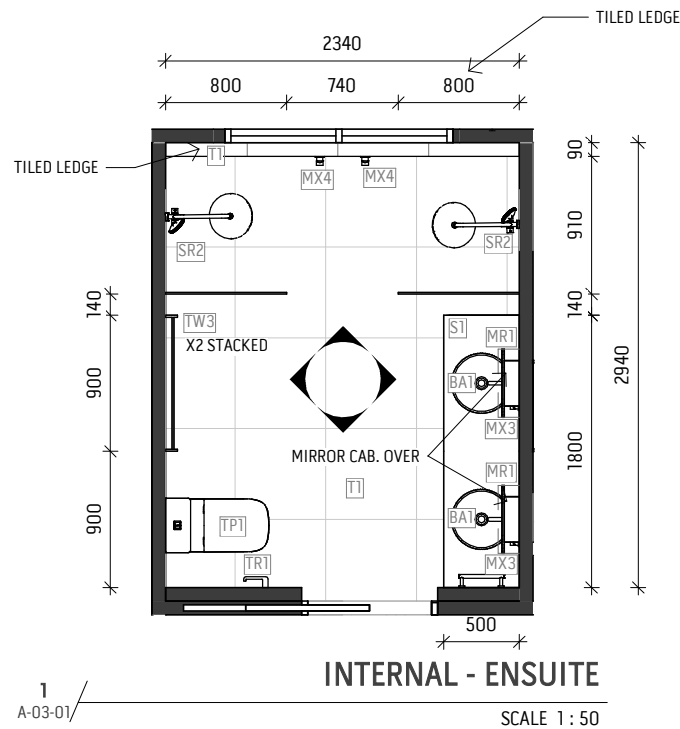




DATE	DESCRIPTION	REV. NO.	DRAWING TITLE : INTERNALS - ENSUITE MADELEINE & NICHOLAS CHILDS 106 HAROLD STREET, HOLLAND PARK	PILGRIM [®]	SCALE : 1 : 50		
03-02-2026	TECHNICAL UPDATES	H					
10-02-2026	TECHNICAL UPDATES	I					
18-02-2026	CONSTRUCTION REVIEW	J					
PILGRIM retains copyright in all documents and drawings and in any works executed from those documents and drawings. The PILGRIM reserves all present and future moral rights in all intellectual property in the designs, documents, drawings and any works executed or to be executed from them.					DRAWN : TH CHECK BY : CA		
PILGRIM by agreement grants the client a license to use the documents and drawings to produce the project, for which they were intended, conditional upon the following: - the license applies only to the site or that part of the site to which the design relates. - PILGRIM has completed the particular stage or stages of architectural service for which PILGRIM has been commissioned. - fees properly due to the designer have been paid in full. Do not scale from drawings, verify all dimensions prior to commencement of construction or fabrication, notify the designer of any discrepancies.					DRAWING NO: A-05-06		
					DATE 18-02-2026	REV	J

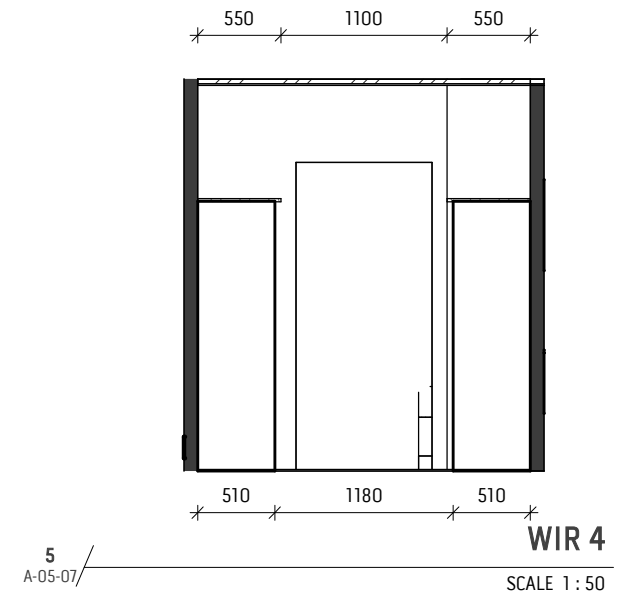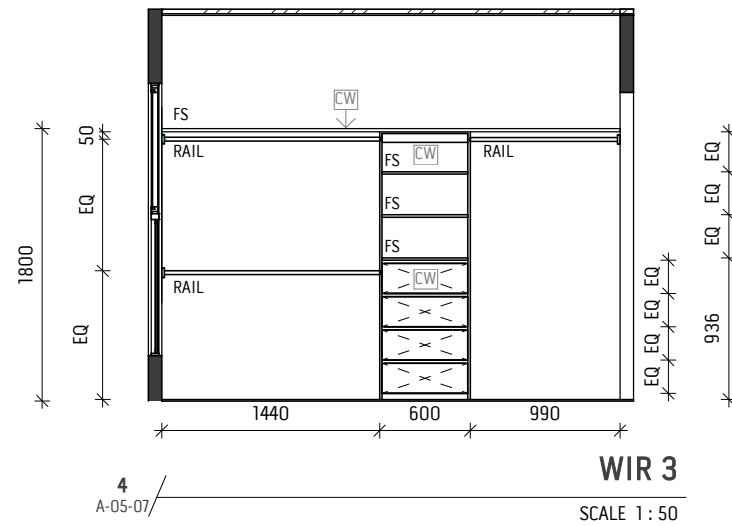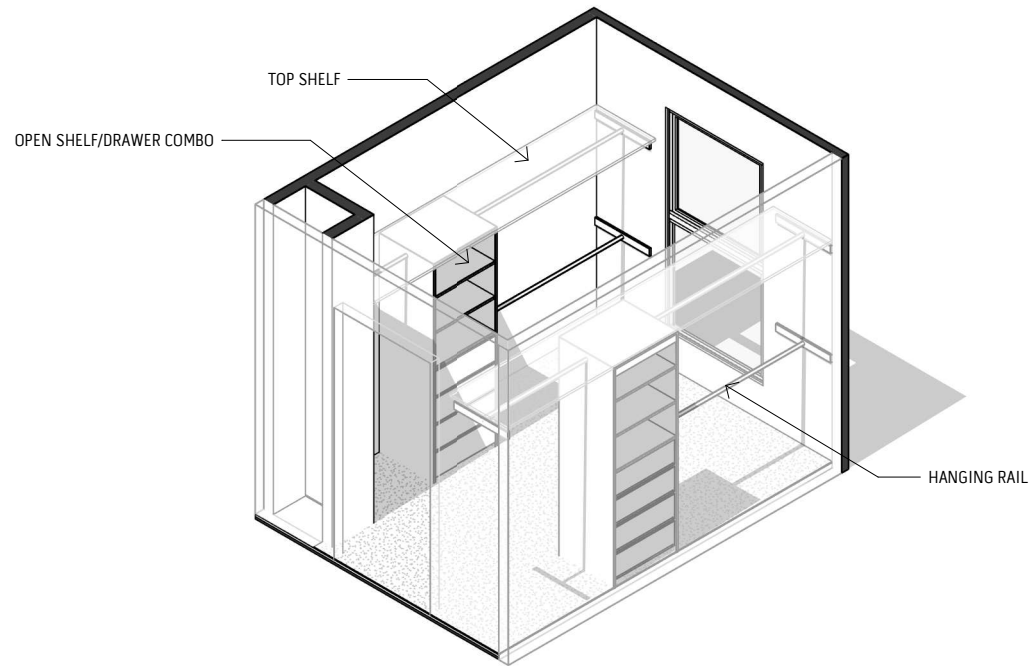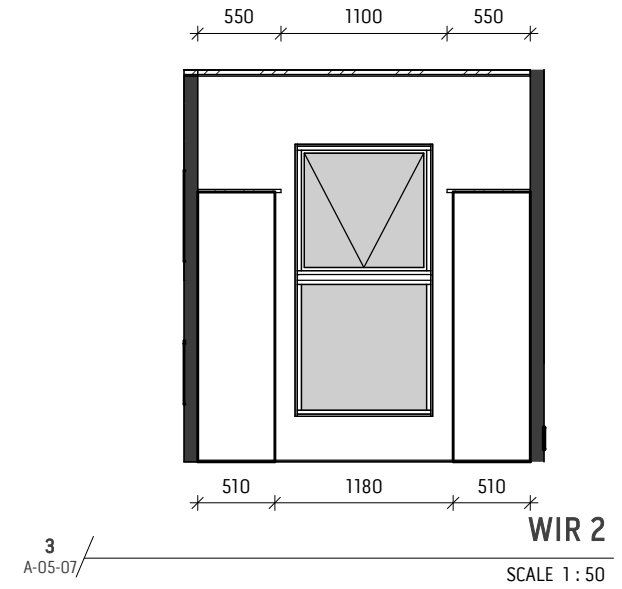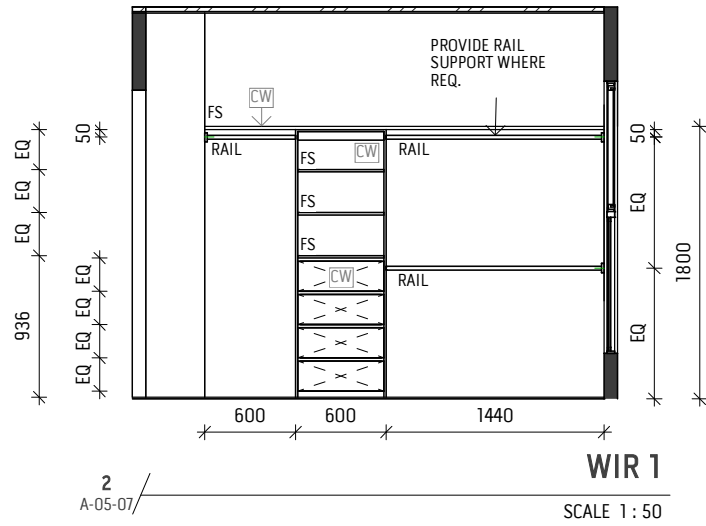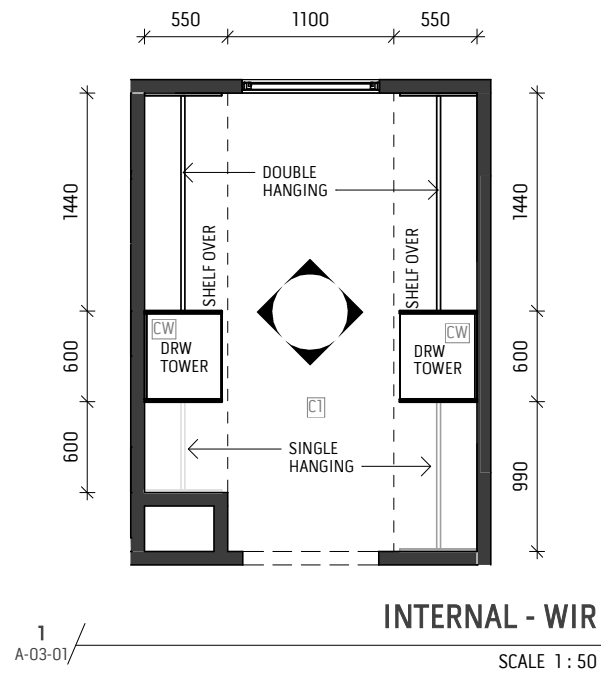

DATE	DESCRIPTION	REV. NO.	DRAWING TITLE : INTERNALS - WIR MADELEINE & NICHOLAS CHILDS 106 HAROLD STREET, HOLLAND PARK		PILGRIM [®]			SCALE : 1 : 50			
03-02-2026	TECHNICAL UPDATES	H									
10-02-2026	TECHNICAL UPDATES	I									
18-02-2026	CONSTRUCTION REVIEW	J									
PILGRIM retains copyright in all documents and drawings and in any works executed from those documents and drawings The PILGRIM reserves all present and future moral rights in all intellectual property in the designs, the documents, drawings and any works executed or to be executed from them. PILGRIM by agreement grants the client a license to use the documents and drawings to produce the project, for which they were intended, conditional upon the following: - the license applies only to the site or that part of the site to which the design relates, - PILGRIM has completed the particular stage or stages of architectural service for which PILGRIM has been commissioned, - fees properly due to the designer have been paid in full. Do not scale from drawings, verify all dimensions prior to commencement of construction or fabrication, notify the designer of any discrepancies.											
									DRAWN : TH CHECK BY : CA		
									DRAWING NO: A-05-07		
									DATE 18-02-2026		REV J

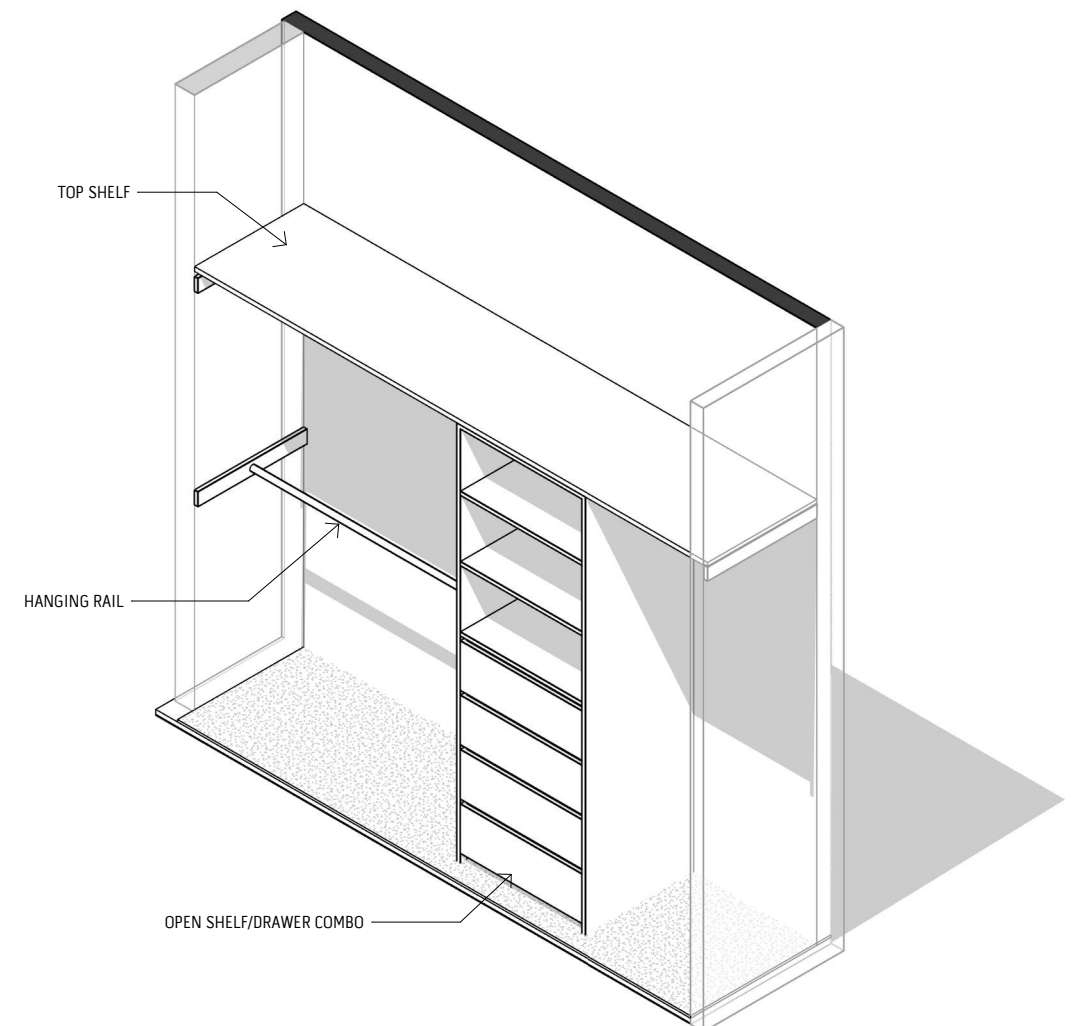


DATE	DESCRIPTION	REV. NO.	DRAWING TITLE : INTERNALS - WARDROBES MADELEINE & NICHOLAS CHILDS 106 HAROLD STREET, HOLLAND PARK		SCALE : 1 : 50	
03-02-2026	TECHNICAL UPDATES	H				
10-02-2026	TECHNICAL UPDATES	I			DRAWN : TH CHECK BY : CA	
18-02-2026	CONSTRUCTION REVIEW	J			DRAWING NO: A-05-08	
PILGRIM retains copyright in all documents and drawings and in any works executed from those documents and drawings The PILGRIM reserves all present and future moral rights in all intellectual property in the designs, the documents, drawings and any works executed or to be executed from them. PILGRIM by agreement grants the client a license to use the documents and drawings to produce the project, for which they were intended, conditional upon the following: - license applies only to the site or that part of the site to which the design relates. - PILGRIM has completed the particular stage or stages of architectural service for which PILGRIM has been commissioned, - fees properly due to the designer have been paid in full. Do not scale from drawings, verify all dimensions prior to commencement of construction or fabrication, notify the designer of any discrepancies.			DATE 18-02-2026 REV J			

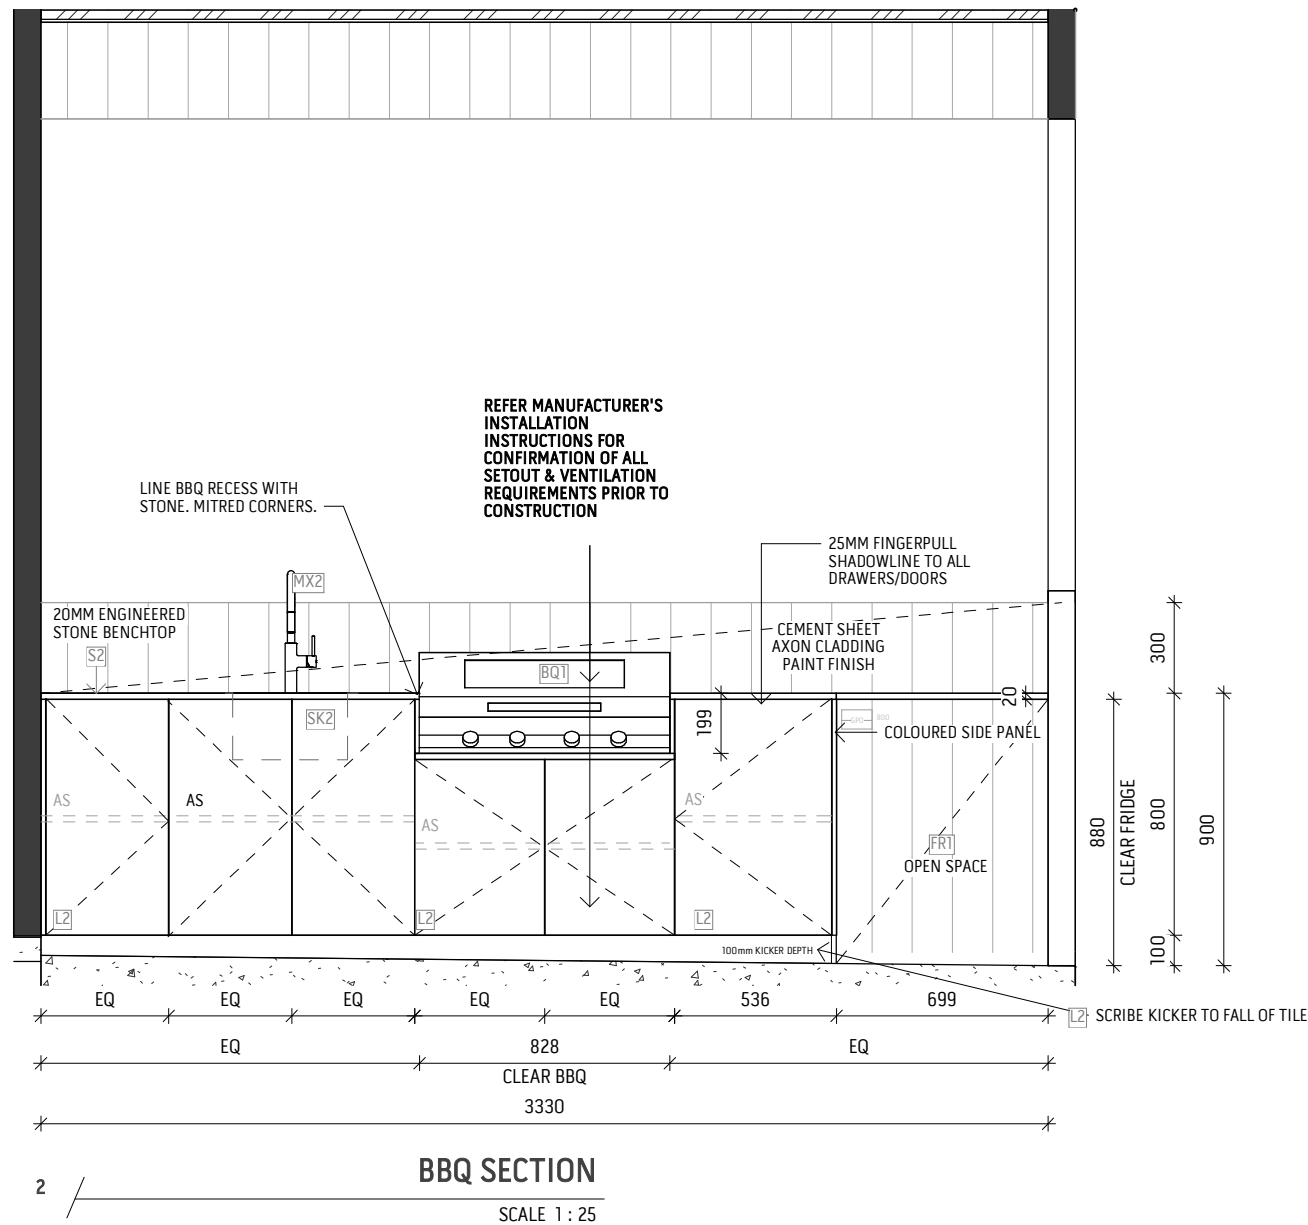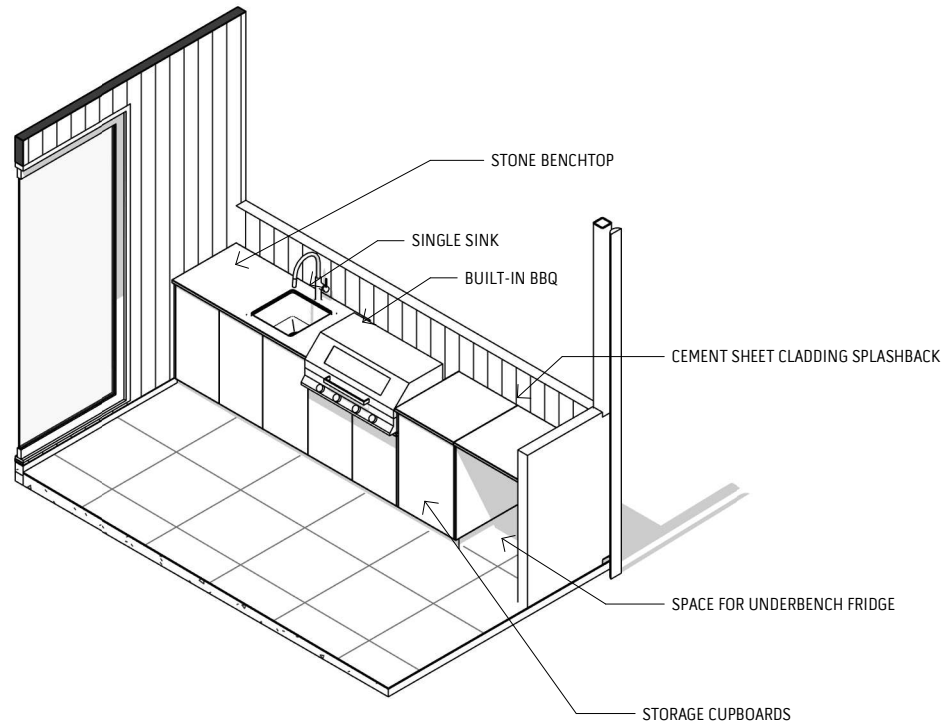
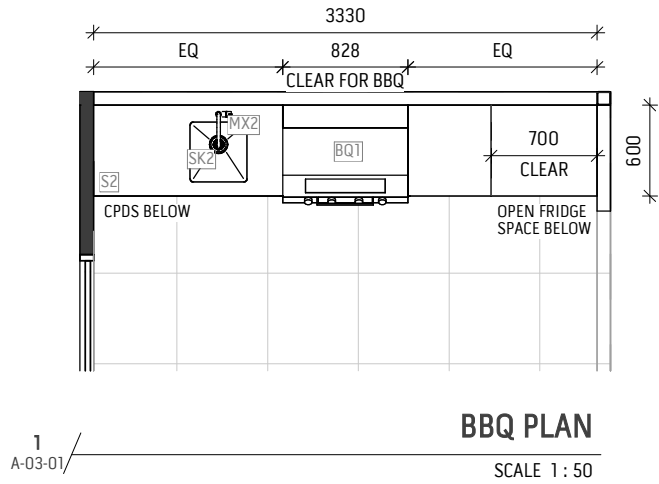


REFER MANUFACTURER'S INSTALLATION INSTRUCTIONS FOR CONFIRMATION OF ALL SETOUT & VENTILATION REQUIREMENTS PRIOR TO CONSTRUCTION

DATE	DESCRIPTION	REV. NO.	DRAWING TITLE :	SCALE :
03-02-2026	TECHNICAL UPDATES	H	INTERNALS - BBQ AREA	As indicated
10-02-2026	TECHNICAL UPDATES	I	MADELEINE & NICHOLAS CHILDS	
18-02-2026	CONSTRUCTION REVIEW	J	106 HAROLD STREET, HOLLAND PARK	
PILGRIM retains copyright in all documents and drawings and in any works executed from those documents and drawings. The PILGRIM reserves all present and future moral rights in all intellectual property in the designs, the documents, drawings and any works executed or to be executed from them.			PILGRIM by agreement grants the client a license to use the documents and drawings to produce the project, for which they were intended, conditional upon the following:	
			- the license applies only to the site or that part of the site to which the design relates.	
			- PILGRIM has completed the particular stage or stages of architectural service for which PILGRIM has been commissioned.	
			- fees properly due to the designer have been paid in full.	
			Do not scale from drawings, verify all dimensions prior to commencement of construction or fabrication, notify the designer of any discrepancies.	
			DRAWING NO: A-05-09	
			DATE	18-02-2026
			REV	J

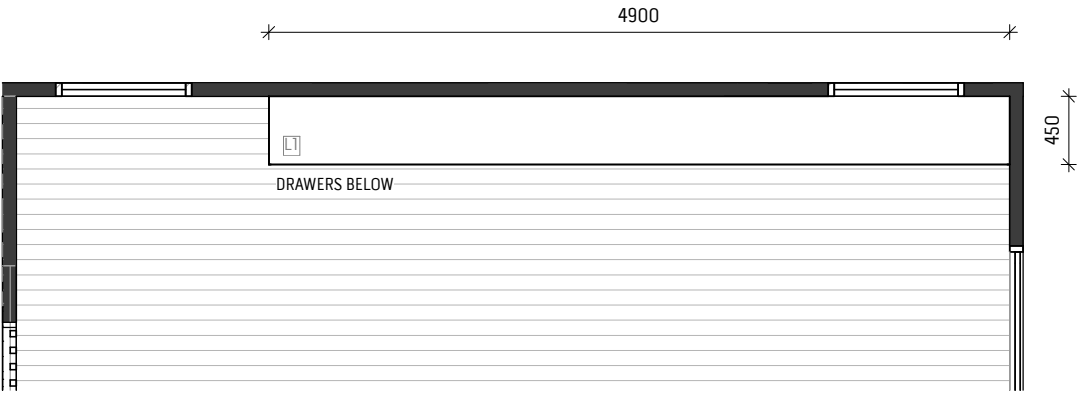

1
A-03-01/ INTERNALS - TV CABINET
SCALE 1 : 50

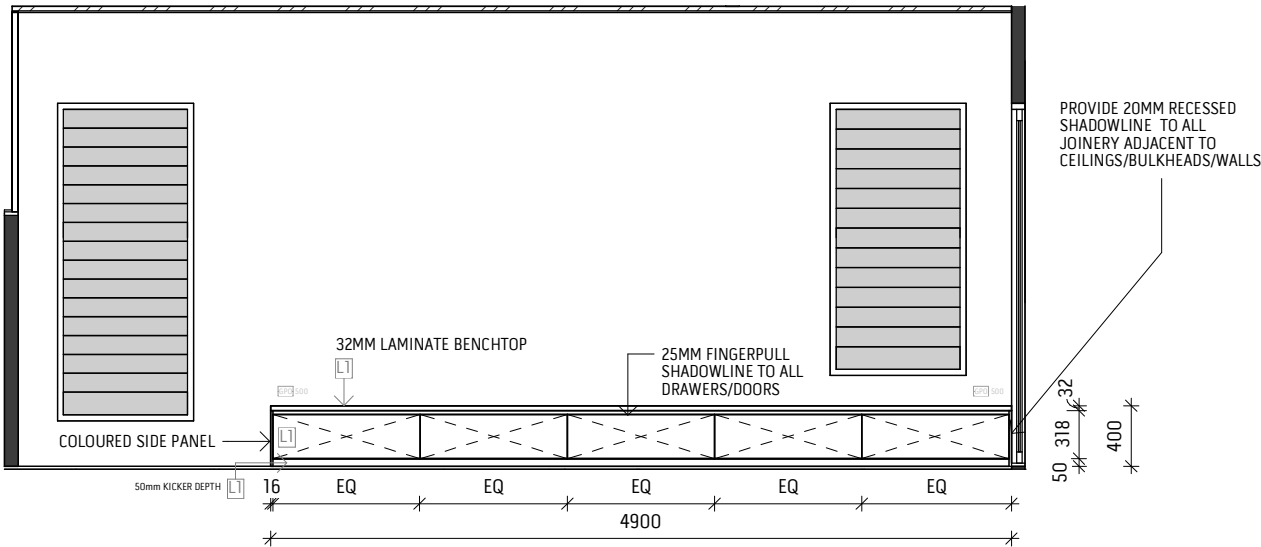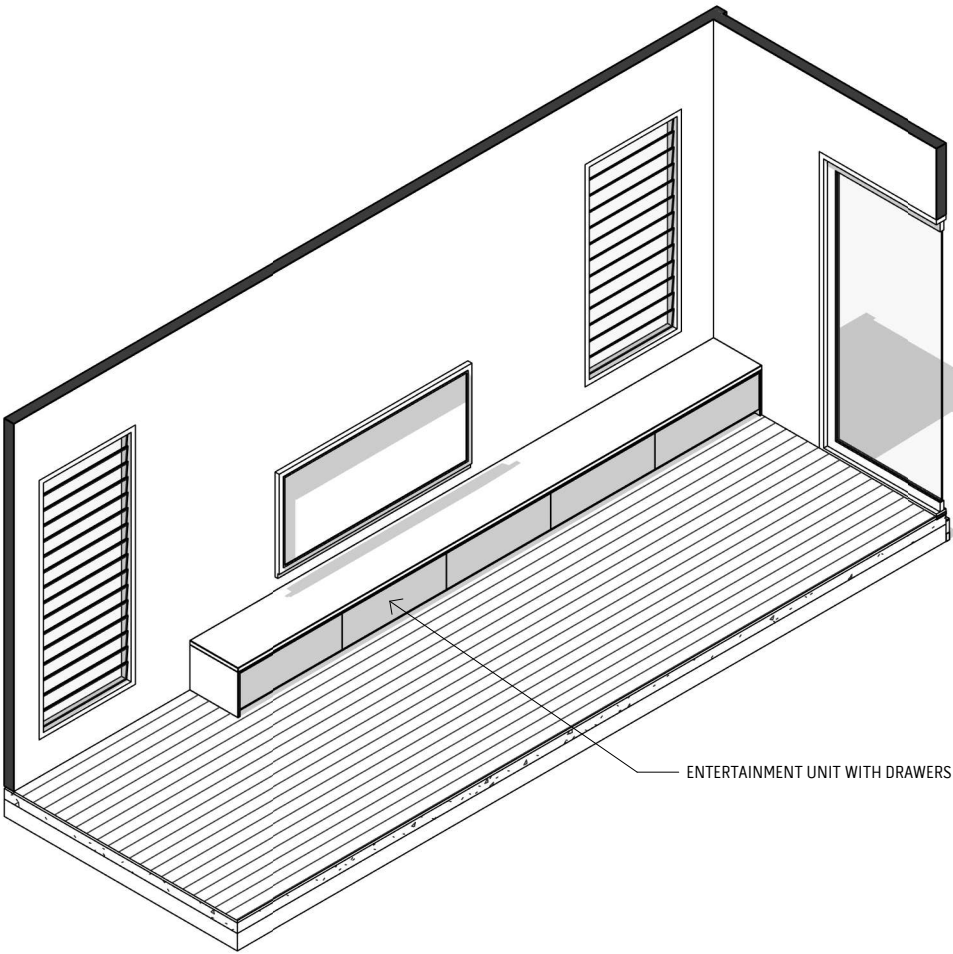


2
TV CABINET SECTION
SCALE 1 : 50

DATE	DESCRIPTION	REV. NO.	DRAWING TITLE :		SCALE :	
03-02-2026	TECHNICAL UPDATES	H	INTERNALS - TV CABINET		1 : 50	
10-02-2026	TECHNICAL UPDATES	I				
18-02-2026	CONSTRUCTION REVIEW	J				
PILGRIM retains copyright in all documents and drawings and in any works executed from those documents and drawings. The PILGRIM reserves all present and future moral rights in all intellectual property in the designs, the documents, drawings and any works executed or to be executed from them. PILGRIM by agreement grants the client a license to use the documents and drawings to produce the project, for which they were intended, conditional upon the following: - the license applies only to the site or that part of the site to which the design relates, - PILGRIM has completed the particular stage or stages of architectural service for which PILGRIM has been commissioned, - fees properly due to the designer have been paid in full. Do not scale from drawings, verify all dimensions prior to commencement of construction or fabrication, notify the designer of any discrepancies.			DRAWING NO: A-05-10		DATE 18-02-2026	
			REV J		CHECK BY: CA	

MADELEINE & NICHOLAS CHILDS

106 HAROLD STREET, HOLLAND PARK

PILGRIM[®]

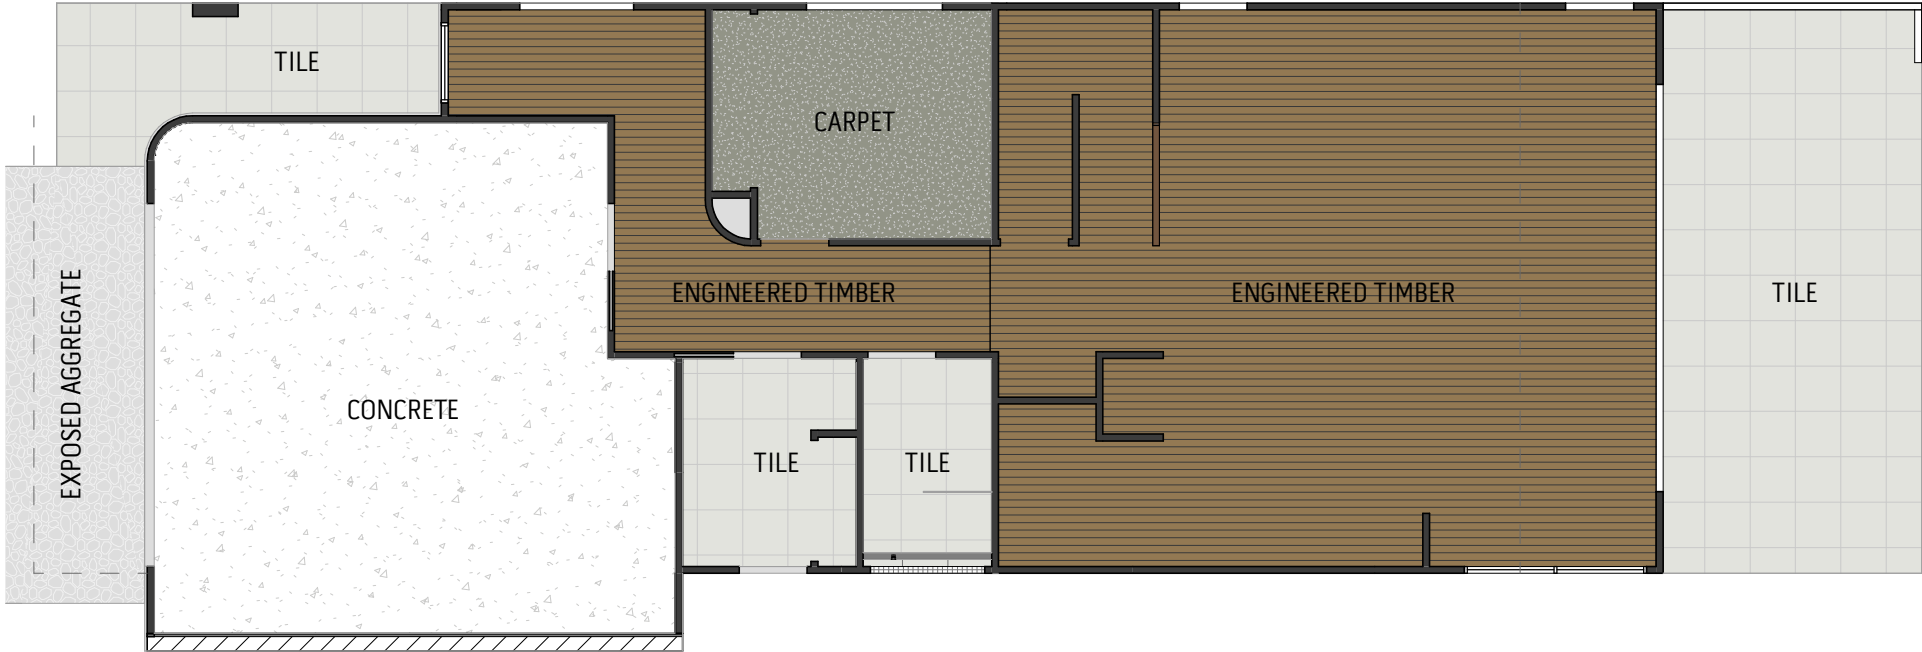

1
A-03-01

GROUND FLOOR FINISHES PLAN

SCALE 1 : 100

- FINISHES PLAN NOTES:
- FINISHES TO BE REFERENCED FROM INTERIOR SELECTIONS/SHOP DRAWINGS
 - ALL FINISHES TO BE INSTALLED PER MANUFACTURER GUIDELINES
 - TILE SETDOWNS TO BE CONFIRMED PRIOR TO SLAB POUR
 - FLOOR TRANSITIONS TO BE COORDINATED WITH FLOORING CONTRACTOR
 - WET AREA TILES TO WALLS TO BE FLOOR TO CEILING UNLESS OTHERWISE NOTED

DATE	DESCRIPTION	REV. NO.	DRAWING TITLE :		SCALE :			
03-02-2026	TECHNICAL UPDATES	H	GROUND FLOOR FINISHES PLAN	MADELEINE & NICHOLAS CHILDS	1 : 100			
10-02-2026	TECHNICAL UPDATES	I			ABN: 89 639 943 187			
18-02-2026	CONSTRUCTION REVIEW	J			QBCC: 1523 8743			
PILGRIM retains copyright in all documents and drawings and in any works executed from those documents and drawings. The PILGRIM reserves all present and future moral rights in all intellectual property in the designs, the documents, drawings and any works executed or to be executed from them. PILGRIM by agreement grants the client a license to use the documents and drawings to produce the project, for which they were intended, conditional upon the following: - the license applies only to the site or that part of the site to which the design relates. - PILGRIM has completed the particular stage or stages of design service for which PILGRIM has been commissioned. - fees properly due to the designer have been paid in full. Do not scale from drawings, verify all dimensions prior to commencement of construction or fabrication, notify the designer of any discrepancies.			106 HAROLD STREET, HOLLAND PARK		DRAWING NO: A-06-01		DRAWN : TH CHECK BY : CA	
			DATE 18-02-2026		REV	J		



1


A-03-01

LEVEL 1 FINISHES PLAN

SCALE 1 : 100

- FINISHES PLAN NOTES:
- FINISHES TO BE REFERENCED FROM INTERIOR SELECTIONS/SHOP DRAWINGS
 - ALL FINISHES TO BE INSTALLED PER MANUFACTURER GUIDELINES
 - TILE SETDOWNS TO BE CONFIRMED PRIOR TO SLAB POUR
 - FLOOR TRANSITIONS TO BE COORDINATED WITH FLOORING CONTRACTOR
 - WET AREA TILES TO WALLS TO BE FLOOR TO CEILING UNLESS OTHERWISE NOTED

DATE	DESCRIPTION	REV. NO.	DRAWING TITLE :		SCALE :	
03-02-2026	TECHNICAL UPDATES	H	LEVEL 1 FINISHES PLAN		1 : 100	
10-02-2026	TECHNICAL UPDATES	I	MADELEINE & NICHOLAS CHILDS		ABN: 89 639 943 187	
18-02-2026	CONSTRUCTION REVIEW	J	106 HAROLD STREET, HOLLAND PARK		QBCL: 1523 8743	
PILGRIM retains copyright in all documents and drawings and in any works executed from those documents and drawings. The PILGRIM reserves all present and future moral rights in all intellectual property in the designs, the documents, drawings and any works executed or to be executed from them. PILGRIM by agreement grants the client a license to use the documents and drawings to produce the project, for which they were intended, conditional upon the following: - the license applies only to the site or that part of the site to which the design relates. - PILGRIM has completed the particular stage or stages of design service for which PILGRIM has been commissioned. - fees properly due to the designer have been paid in full. Do not scale from drawings, verify all dimensions prior to commencement of construction or fabrication, notify the designer of any discrepancies.			DRAWING NO: A-06-02		DRAWN : TH	
			CHECK BY : CA		DATE 18-02-2026	
					REV	J

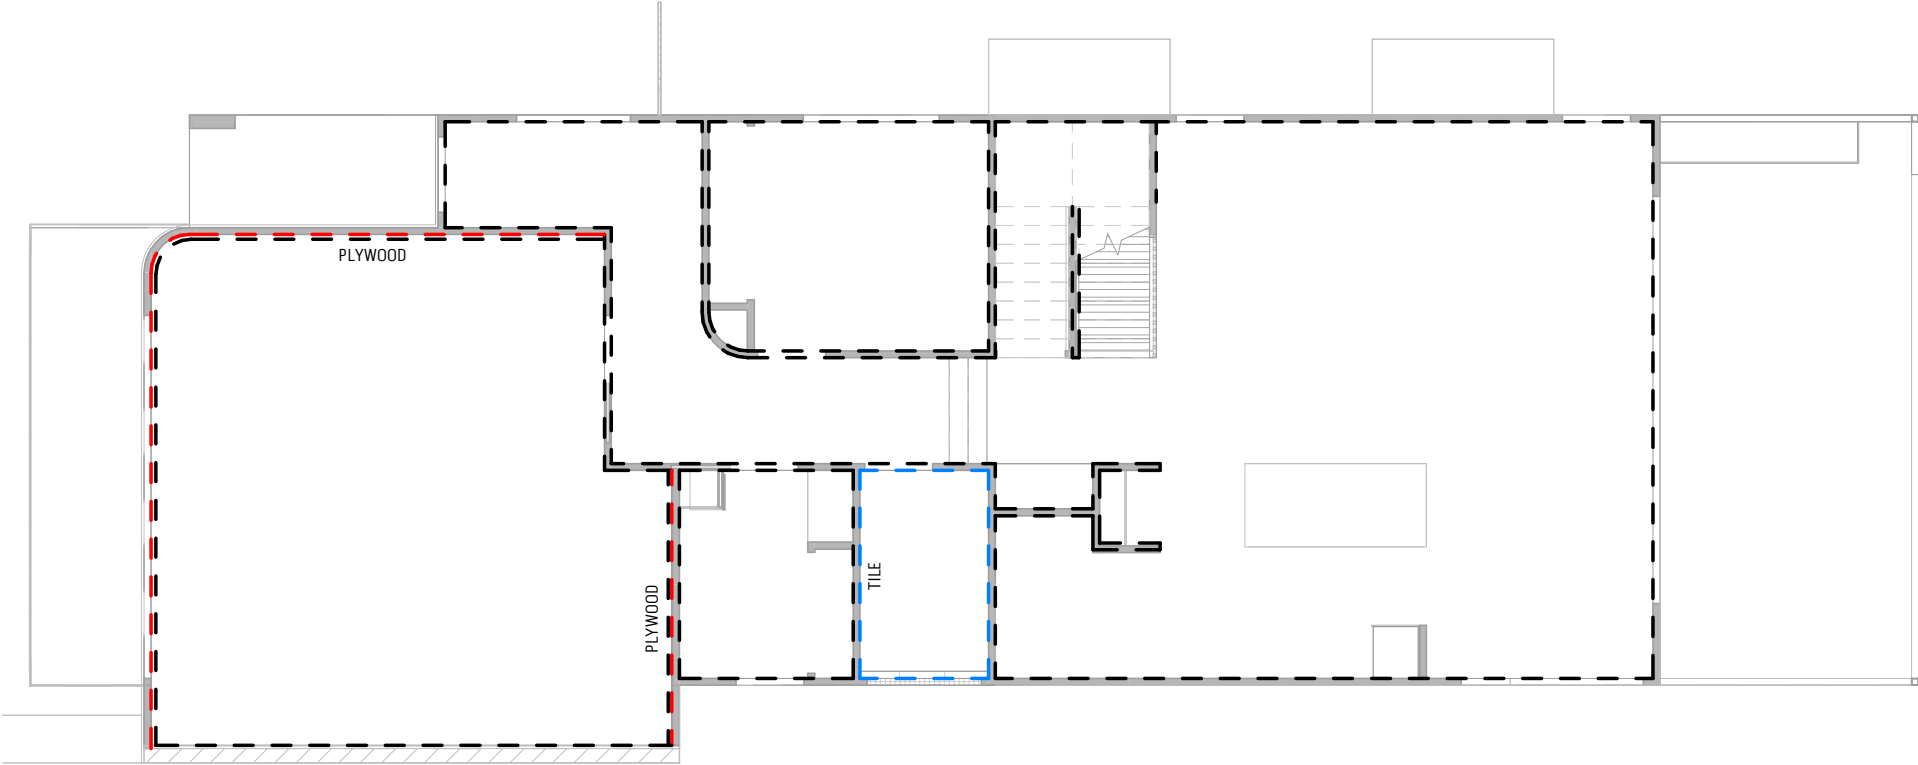


- — — — PLASTERBOARD
- — — — WALL TILE
- — — — 12mm PLYWOOD

1
A-03-01/ **GROUND FLOOR - INTERNAL CLADDING**
SCALE 1 : 100

DATE	DESCRIPTION	REV. NO.	DRAWING TITLE :		SCALE :	
03-02-2026	TECHNICAL UPDATES	H	GROUND FLOOR CLADDING DIAGRAM	MADELEINE & NICHOLAS CHILDS	As indicated	
10-02-2026	TECHNICAL UPDATES	I			ABN: 89 639 943 187	
18-02-2026	CONSTRUCTION REVIEW	J			QBCC: 1523 8743	
PILGRIM retains copyright in all documents and drawings and in any works executed from those documents and drawings. The PILGRIM reserves all present and future moral rights in all intellectual property in the designs, the documents, drawings and any works executed or to be executed from them. PILGRIM by agreement grants the client a license to use the documents and drawings to produce the project, for which they were intended, conditional upon the following: - the license applies only to the site or that part of the site to which the design relates. - PILGRIM has completed the particular stage or stages of design service for which PILGRIM has been commissioned. - fees properly due to the designer have been paid in full. Do not scale from drawings, verify all dimensions prior to commencement of construction or fabrication, notify the designer of any discrepancies.			106 HAROLD STREET, HOLLAND PARK		DRAWN : TH	
					CHECK BY : CA	
					DRAWING NO: A-06-03	
					DATE	18-02-2026

- PLASTERBOARD
- WALL TILE
- 12mm PLYWOOD

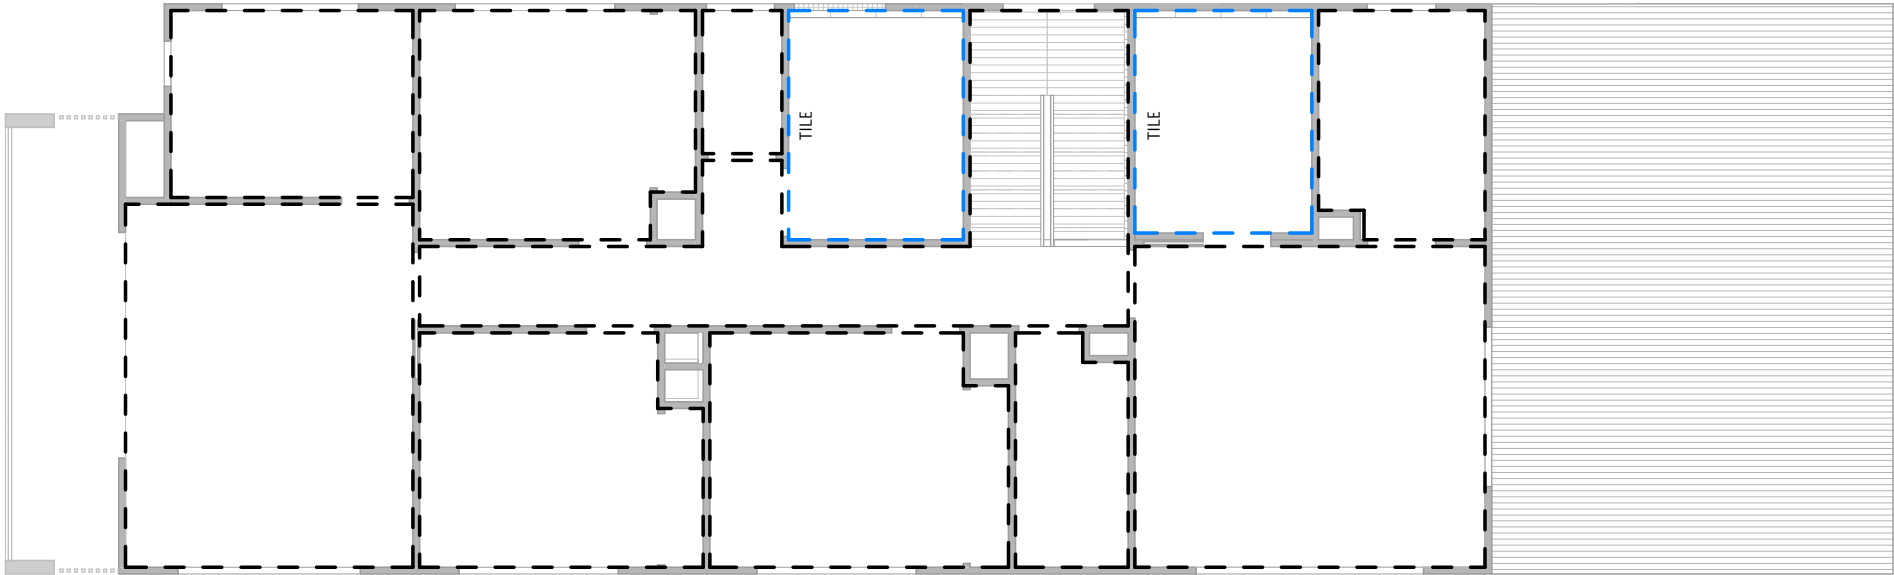

1

A-03-01/

LEVEL 1 - INTERNAL CLADDING

SCALE 1 : 100

DATE	DESCRIPTION	REV. NO.	DRAWING TITLE :		SCALE :	
03-02-2026	TECHNICAL UPDATES	H	LEVEL 1 CLADDING DIAGRAM		As indicated	
10-02-2026	TECHNICAL UPDATES	I	MADELEINE & NICHOLAS CHILDS		ABN: 89 639 943 187	
18-02-2026	CONSTRUCTION REVIEW	J	106 HAROLD STREET, HOLLAND PARK		QBCL: 1523 8743	
PILGRIM retains copyright in all documents and drawings and in any works executed from those documents and drawings. The PILGRIM reserves all present and future moral rights in all intellectual property in the designs, the documents, drawings and any works executed or to be executed from them. PILGRIM by agreement grants the client a license to use the documents and drawings to produce the project, for which they were intended, conditional upon the following: - the license applies only to the site or that part of the site to which the design relates. - PILGRIM has completed the particular stage or stages of design service for which PILGRIM has been commissioned. - fees properly due to the designer have been paid in full. Do not scale from drawings, verify all dimensions prior to commencement of construction or fabrication, notify the designer of any discrepancies.			DRAWN : TH		CHECK BY : CA	
			DRAWING NO: A-06-04		DATE 18-02-2026	
					REV	J

ELECTRICAL NOTES

LIGHT SWITCHES TO BE MOUNTED AT 1200H ABOVE FINISHED FLOOR

ALL SMOKE DETECTORS TO BE INTERCONNECTED

GPOs IN BATHROOMS TO BE LOCATED INSIDE VANITY

ELECTRICAL LAYOUT SUPPLIED FOR GUIDE ONLY - ELECTRICAL LAYOUT TO BE CONFIRMED IN WRITING BY CLIENT / CONSULTANT / BUILDER, PRIOR TO ORDER + FITOFF


PROVIDE ISOLATION SWITCH TO ELECTRIC HOT PLATES WHERE REQUIRED

ELECTRICAL CONTRACTOR TO CONFIRM ELECTRICAL LOADS FOR EACH APPLIANCE/PLANT AND ALLOW FOR SUITABLE POWER OUTLET

ALL ELECTRICAL POINTS TO BE INSTALLED BY LICENSED ELECTRICIAN - TO COMPLY WITH ALL ELECTRICAL CODES & AUSTRALIAN STANDARDS

LEGEND

- PENDANT LIGHT
- CEILING MOUNTED LIGHT POINT
- WALL MOUNTED FEATURE LIGHT POINT
- EXTERNAL WALL MOUNTED SPOTLIGHT
- SMOKE DETECTOR - HARD WIRED - REFER TO GENERAL NOTES FOR MORE INFORMATION
- SINGLE POWER OUTLET (SGPO)
- DOUBLE POWER OUTLET (DGPO)
- EXTERNAL POWER OUTLET (DGPO)
- TELEPHONE POINT
- DATA / NETWORK / ETHERNET POINT
- TV ANTENNA CO-AX POINT
- MOTION SENSOR ACTIVATED FLOODLIGHT
- MOTION SENSOR ACTIVATED LIGHT POINT
- METER BOX + NBN CONNECTION
- 1 X 600 FLUORESCENT LIGHT
- 2 x 1200 FLUORESCENT LIGHT
- CEILING FAN
- EXHAUST FAN
- LIGHT SWITCH LINE
- DIMMER SWITCH LINE
- SWITCH
- LED STRIP LIGHTING

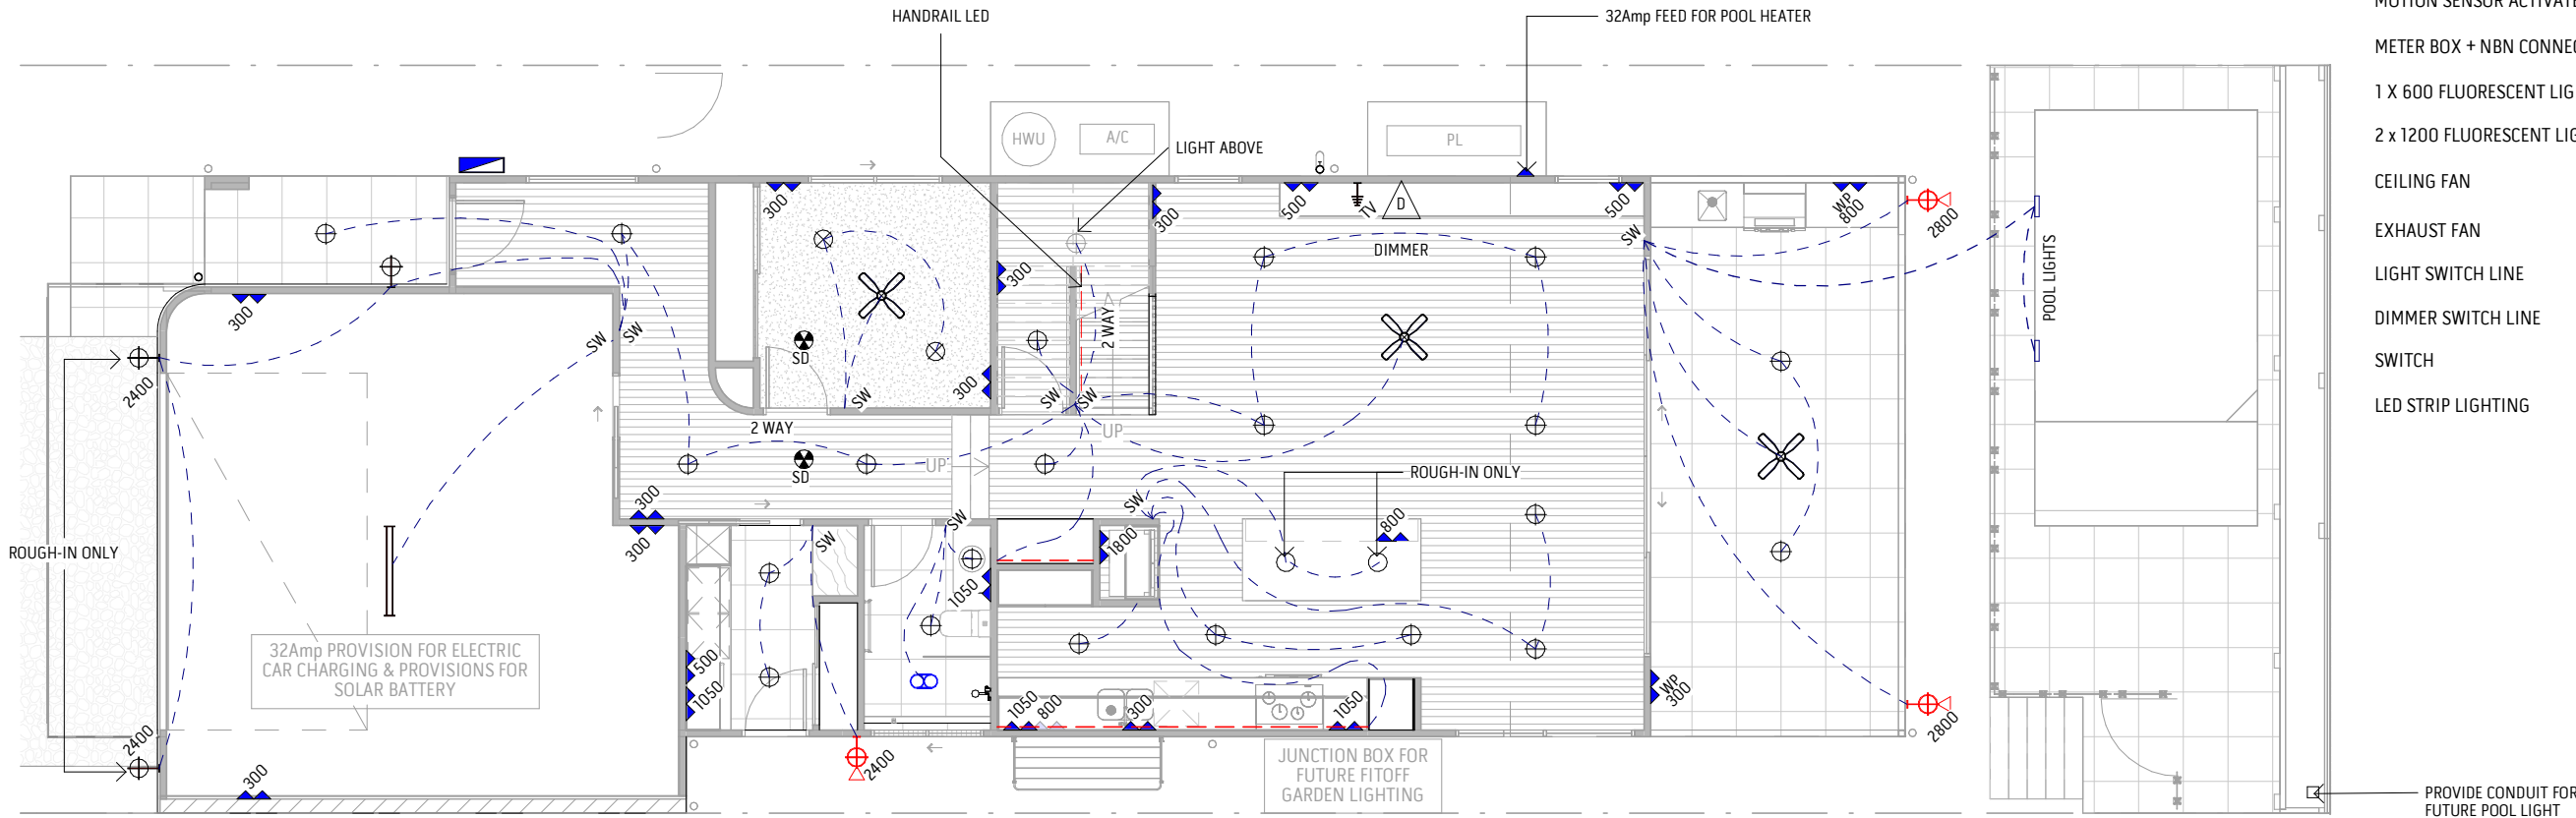

1
A-03-01

GROUND FLOOR ELECTRICAL PLAN

SCALE 1 : 100

DATE	DESCRIPTION	REV. NO.	DRAWING TITLE :		SCALE :	
03-02-2026	TECHNICAL UPDATES	H	GROUND ELECTRICAL PLAN	MADELEINE & NICHOLAS CHILDS	1 : 100	
10-02-2026	TECHNICAL UPDATES	I			ABN: 89 639 943 187 QBCC: 1523 8743	
18-02-2026	CONSTRUCTION REVIEW	J			DRAWN : TH CHECK BY: CA	
PILGRIM retains copyright in all documents and drawings and in any works executed from those documents and drawings. The PILGRIM reserves all present and future moral rights in all intellectual property in the designs, the documents, drawings and any works executed or to be executed from them. PILGRIM by agreement grants the client a license to use the documents and drawings to produce the project, for which they were intended, conditional upon the following: - the license applies only to the site or that part of the site to which the design relates. - PILGRIM has completed the particular stage or stages of design service for which PILGRIM has been commissioned. - fees properly due to the designer have been paid in full. Do not scale from drawings, verify all dimensions prior to commencement of construction or fabrication, notify the designer of any discrepancies.			DRAWING NO: A-06-05			
			DATE 18-02-2026			
			REV	J		

ELECTRICAL NOTES

LIGHT SWITCHES TO BE MOUNTED AT 1200H ABOVE FINISHED FLOOR

ALL SMOKE DETECTORS TO BE INTERCONNECTED

GPOs IN BATHROOMS TO BE LOCATED INSIDE VANITY

ELECTRICAL LAYOUT SUPPLIED FOR GUIDE ONLY - ELECTRICAL LAYOUT TO BE
CONFIRMED IN WRITING BY CLIENT / CONSULTANT / BUILDER, PRIOR TO
ORDER + FITOFF

PROVIDE ISOLATION SWITCH TO ELECTRIC HOT PLATES WHERE REQUIRED

ELECTRICAL CONTRACTOR TO CONFIRM ELECTRICAL LOADS FOR EACH APPLIANCE/PLANT AND ALLOW FOR SUITABLE POWER OUTLET

ALL ELECTRICAL POINTS TO BE INSTALLED BY LICENSED ELECTRICIAN - TO COMPLY WITH ALL ELECTRICAL CODES & AUSTRALIAN STANDARDS

LEGEND

PENDANT LIGHT

CEILING MOUNTED LIGHT POINT

WALL MOUNTED FEATURE LIGHT POINT

EXTERNAL WALL MOUNTED SPOTLIGHT

SMOKE DETECTOR - HARD WIRED - REFER TO GENERAL
NOTES FOR MORE INFORMATION

SINGLE POWER OUTLET (SGPO)

DOUBLE POWER OUTLET (DGPO)

EXTERNAL POWER OUTLET (DGPO)

TELEPHONE POINT

DATA / NETWORK / ETHERNET POINT

TV ANTENNA CO-AX POINT

MOTION SENSOR ACTIVATED FLOODLIGHT

MOTION SENSOR ACTIVATED LIGHT POINT

METER BOX + NBN CONNECTION

1 X 600 FLUORESCENT LIGHT

2 x 1200 FLUORESCENT LIGHT

CEILING FAN


EXHAUST FAN

LIGHT SWITCH LINE

DIMMER SWITCH LINE

SWITCH

LED STRIP LIGHTING

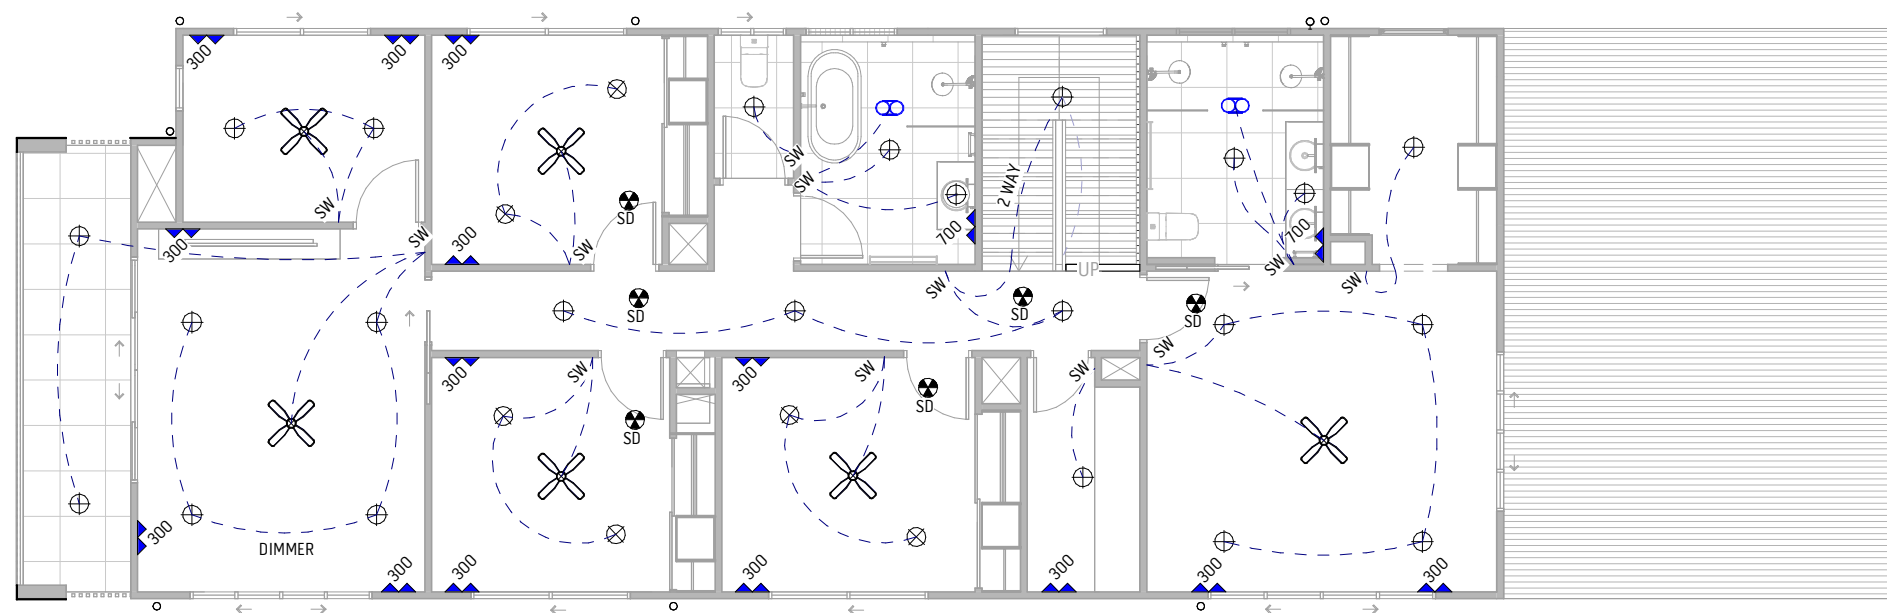

LEVEL 1 ELECTRICAL PLAN

SCALE 1 : 100

DATE	DESCRIPTION	REV. NO.
03-02-2026	TECHNICAL UPDATES	H
10-02-2026	TECHNICAL UPDATES	I
18-02-2026	CONSTRUCTION REVIEW	J

PILGRIM retains copyright in all documents and drawings and in any works executed from those documents and drawings. PILGRIM reserves all present and future moral rights in all intellectual property in the designs, the documents, drawings and any works executed or to be executed from them.

PILGRIM by agreement grants the client a license to use the documents and drawings to produce the project, for which they were intended, conditional upon the following:

- the license applies only to the site or that part of the site to which the design relates;
- PILGRIM has completed the particular stage or stages of design service for which PILGRIM has been commissioned;
- any copyright due to the designer have been paid in full.

Do not scale from drawings, verify all dimensions prior to commencement of construction or fabrication, notify the designer of any discrepancies.

DRAWING TITLE :

LEVEL 1 ELECTRICAL PLAN

MADELEINE & NICHOLAS CHILDS

106 HAROLD STREET, HOLLAND PARK

SCALE : 1 : 100

ABN: 89 639 943 187
QBCC: 1523 8743

DRAWN : TH CHECK BY : CA




DRAWING NO: A-06-06




DATE 18-02-2026

Y	J
---	---



REFER TO SIZING SCHEDULE FOR ALL SIZES

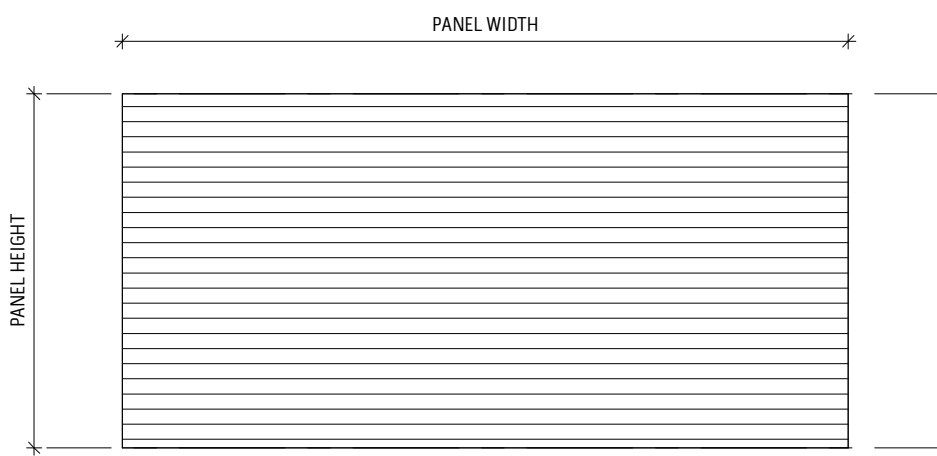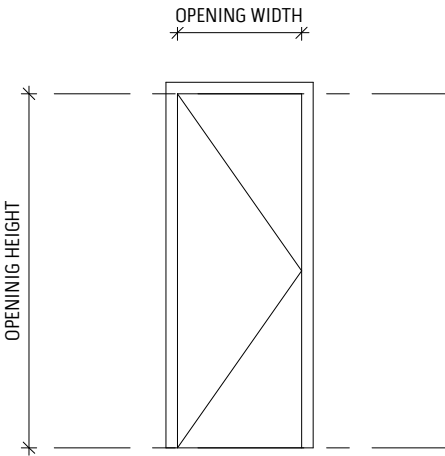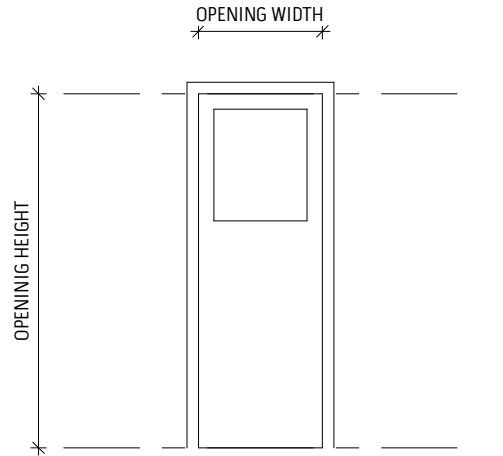		
GARAGE DOOR - SECTIONAL	HOLLOW CORE SINGLE SWING DOOR	SOLID CORE SINGLE SWING W/ LITE WINDOW
ALUMINIUM FRAME	TIMBER FRAME	TIMBER FRAME
D01	D05, D06, D07, D15, D16, D17, D18, D19, D20, D21, D22	D04

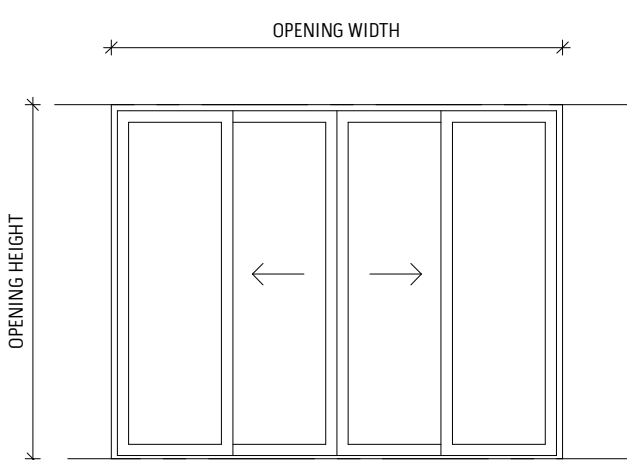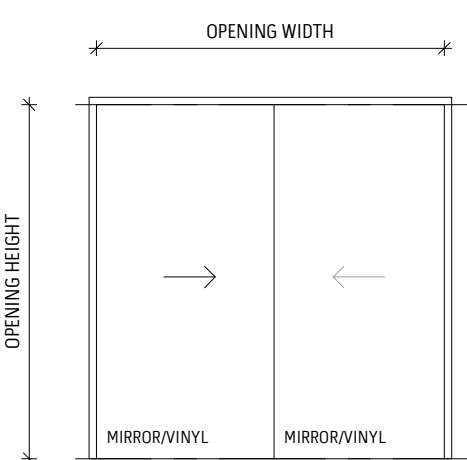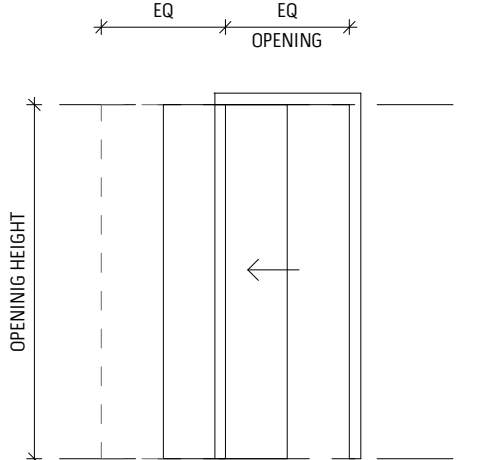
		
GLASS PANEL SLIDING DOOR - FSSF	MIRROR/VINYL PANEL SLIDING DOOR	HOLLOW CORE CAVITY SLIDING DOOR
ALUMINIUM FRAME	TIMBER FRAME	TIMBER FRAME
D03, D12	D10, D11, D23, D24, D25	D08, D09, D13, D14

DOOR TYPE	COUNT
GLASS PANEL SLIDING DOOR - FSSF	2
HOLLOW CORE SINGLE CAVITY SLIDING DOOR	4
HOLLOW CORE SINGLE SWING DOOR	11
MIRROR PANEL SLIDING DOOR	4
SECTIONAL PANEL MOTORISED GARAGE DOOR	1
SOLID CORE SINGLE SWING FEATURE DOOR	1
SOLID CORE SINGLE SWING W/ LITE WINDOW	1
VINYL PANEL SLIDING DOOR	1

1. ALL DIMENSIONS GIVEN ARE TO STRUCTURAL OPENING SIZE & ARE TO BE VERIFIED ON SITE BEFORE COMMENCING FABRICATION.
2. DIMENSIONS DO NOT ACCOUNT FOR ANY SLAB REBATES. SLAB REBATES SHALL BE CONFIRMED WITH WINDOW AND DOOR MANUFACTURER.
3. ALL WINDOWS, LOUVRES & DOORS ARE VIEWED EXTERNALLY UNLESS NOTED OTHERWISE. REFER FLOOR PLANS FOR SWING/SLIDING DIRECTION.
4. ALL ALUMINIUM FRAMES TO BE FINISHED IN POWDERCOAT
5. ALL WINDOWS & DOORS TO BE FLASHED, CAULKED AND PROVIDED WITH WEATHERPROOF / DRAUGHT PROOF SEALS IN ACCORDANCE WITH MANUFACTURERS PUBLISHED RECOMMENDATIONS AND CODE REQUIREMENTS.
6. ALL SUB-SILLS TO HAVE ENDCAPS SEALED WATERTIGHT
7. ALL GLASS TO BE DESIGNED AND INSTALLED IN ACCORDANCE WITH AS 2047, AS 1170, AS 1288 AND ALL OTHER RELEVANT CODES AND STANDARDS.
8. ALL EXTERNAL GLASS FRAME TYPES TO BE IN ACCORDANCE WITH THE ENERGY RATERS REPORT.
9. ALL EXTERNAL WINDOW/DOOR GLAZING U & SHGC VALUES TO COMPLY WITH ENERGY RATERS REPORT.
10. SAFETY GLAZING TO BE USED IN THE FOLLOWING CASES:
 - ALL ROOMS (WITHIN 500mm VERTICAL FROM FINISHED FLOOR LEVEL)
 - BATHROOMS (WITHIN 1500mm VERTICAL FROM FINISHED FLOOR LEVEL)
 - LAUNDRY ((WITHIN 1200mm VERTICAL FROM FINISHED FLOOR LEVEL/AND OR WITHIN 300mm HORIZONTAL FROM DOORS)
 - DOORWAY (WITHIN 300mm HORIZONTAL FROM ALL DOORS)
 - SHOWER SCREENS TO BE GRADE 'A' SAFETY GLASS IN ACCORDANCE WITH AS 1288.
11. ALL OPENABLE WINDOWS & SLIDING DOORS TO BE LOCKABLE.
12. ALL OPENABLE WINDOWS ABOVE THE GROUND FLOOR LEVEL THAT DO NOT OPEN TO A BALCONY TO BE RESTRICTED TO 125mm MAX. OPENING.
13. ALL DOOR HANDLES TO BE MOUNTED 1000mm AFFL (HANDLE CENTRELINE).
14. KEYED LOCKS TO ALL OPENING WINDOWS AND SLIDING DOORS
15. INSECT SCREENS TO ALL WINDOWS AND SLIDING DOORS

DATE	DESCRIPTION	REV. NO.	DRAWING TITLE : DOOR SCHEDULE 106 HAROLD STREET, HOLLAND PARK	MADELEINE & NICHOLAS CHILDS	PILGRIM [®]																								
03-02-2026	TECHNICAL UPDATES	H																											
10-02-2026	TECHNICAL UPDATES	I																											
18-02-2026	CONSTRUCTION REVIEW	J																											
PILGRIM retains copyright in all documents and drawings and in any works executed from those documents and drawings. The PILGRIM reserves all present and future moral rights in all intellectual property in the designs, the documents, drawings and any works executed or to be executed from them. PILGRIM by agreement grants the client a license to use the documents and drawings to produce the project, for which they were intended, conditional upon the following: - the license applies only to the site or that part of the site to which the design relates. - PILGRIM has completed the particular stage or stages of design service for which PILGRIM has been commissioned. - fees properly due to the designer have been paid in full. Do not scale from drawings, verify all dimensions prior to commencement of construction or fabrication, notify the designer of any discrepancies.			<table><tr><td colspan="2">SCALE :</td><td colspan="2">1 : 50</td></tr><tr><td>ABN:</td><td colspan="3">89 639 943 187</td></tr><tr><td>QBLCL:</td><td colspan="3">1523 8743</td></tr><tr><td>DRAWN :</td><td>TH</td><td>CHECK BY :</td><td>CA</td></tr><tr><td colspan="4">DRAWING NO: A-07-01</td></tr><tr><td>DATE</td><td>18-02-2026</td><td>REV</td><td>J</td></tr></table>			SCALE :		1 : 50		ABN:	89 639 943 187			QBLCL:	1523 8743			DRAWN :	TH	CHECK BY :	CA	DRAWING NO: A-07-01				DATE	18-02-2026	REV	J
SCALE :		1 : 50																											
ABN:	89 639 943 187																												
QBLCL:	1523 8743																												
DRAWN :	TH	CHECK BY :	CA																										
DRAWING NO: A-07-01																													
DATE	18-02-2026	REV	J																										


REFER TO SIZING SCHEDULE FOR ALL SIZES

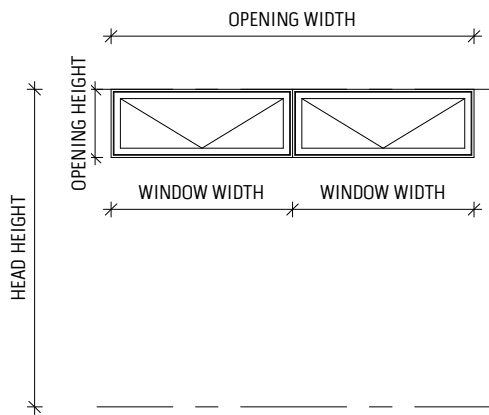

AWNING - AA

ALUMINIUM FRAME


W07, W08

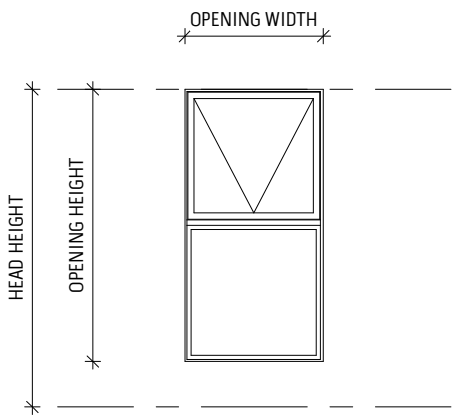

AWNING-FIXED - AF

ALUMINIUM FRAME


W21

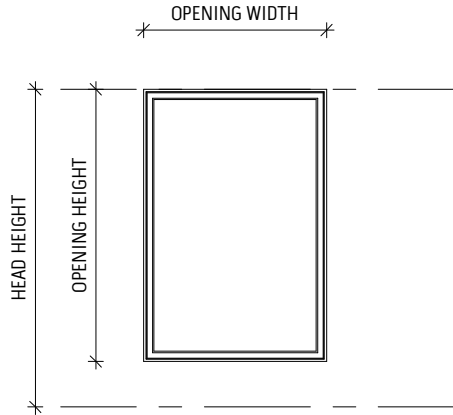

FIXED - FX

ALUMINIUM FRAME


W01, W02, W09, W10

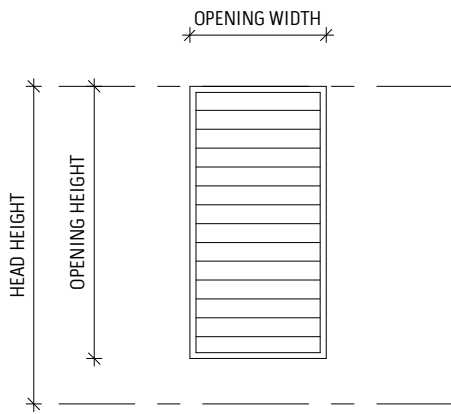

LOUVRE - L

ALUMINIUM FRAME


W05, W06

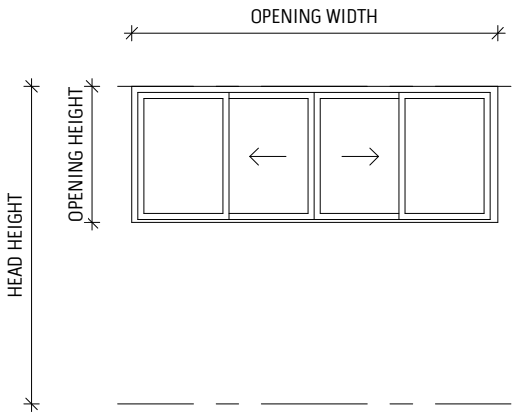

SLIDING (4 PANEL) - FSSF

ALUMINIUM FRAME

W18, W19, W20

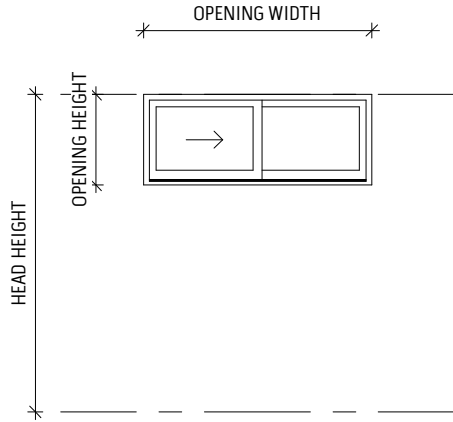

SLIDING (2 PANEL) - SF

ALUMINIUM FRAME

W03, W04, W10, W11, W12, W13, W14, W15, W16, W17

WINDOW TYPE	COUNT
AWNING - AA	2
AWNING-FIXED - AF	1
FIXED - FX	4
LOUVRE - L	2
SLIDING (2 PANEL) - SF	6
SLIDING (2 PANEL) TILE - SF	3
SLIDING (4 PANEL) - FSSF	3

1. ALL DIMENSIONS GIVEN ARE TO STRUCTURAL OPENING SIZE & ARE TO BE VERIFIED ON SITE BEFORE COMMENCING FABRICATION.

2. DIMENSIONS DO NOT ACCOUNT FOR ANY SLAB REBATES. SLAB REBATES SHALL BE CONFIRMED WITH WINDOW AND DOOR MANUFACTURER.

3. ALL WINDOWS, LOUVRES & DOORS ARE VIEWED EXTERNALLY UNLESS NOTED OTHERWISE. REFER FLOOR PLANS FOR SWING/SLIDING DIRECTION.

4. ALL ALUMINIUM FRAMES TO BE FINISHED IN POWDERCOAT

5. ALL WINDOWS & DOORS TO BE FLASHED, CAULKED AND PROVIDED WITH WEATHERPROOF / DRAUGHT PROOF SEALS IN ACCORDANCE WITH MANUFACTURERS PUBLISHED RECOMMENDATIONS AND CODE REQUIREMENTS.

6. ALL SUB-SILLS TO HAVE ENDCAPS SEALED WATERTIGHT

7. ALL GLASS TO BE DESIGNED AND INSTALLED IN ACCORDANCE WITH AS 2047, AS 1170, AS 1288 AND ALL OTHER RELEVANT CODES AND STANDARDS.

8. ALL EXTERNAL GLASS FRAME TYPES TO BE IN ACCORDANCE WITH THE ENERGY RATERS REPORT.

9. ALL EXTERNAL WINDOW/DOOR GLAZING U & SHGC VALUES TO COMPLY WITH ENERGY RATERS REPORT.

10. SAFETY GLAZING TO BE USED IN THE FOLLOWING CASES:
-ALL ROOMS (WITHIN 500mm VERTICAL FROM FINISHED FLOOR LEVEL)
-BATHROOMS (WITHIN 1500mm VERTICAL FROM FINISHED FLOOR LEVEL)
-LAUNDRY ((WITHIN 1200mm VERTICAL FROM FINISHED FLOOR LEVEL/AND OR WITHIN 300mm HORIZONTAL FROM DOORS)
-DOORWAY (WITHIN 300mm HORIZONTAL FROM ALL DOORS)
-SHOWER SCREENS TO BE GRADE 'A' SAFETY GLASS IN ACCORDANCE WITH AS 1288.

11. ALL OPENABLE WINDOWS & SLIDING DOORS TO BE LOCKABLE.

12. ALL OPENABLE WINDOWS ABOVE THE GROUND FLOOR LEVEL THAT DO NOT OPEN TO A BALCONY TO BE RESTRICTED TO 125mm MAX. OPENING.

13. ALL DOOR HANDLES TO BE MOUNTED 1000mm AFFL (HANDLE CENTRELINE).

14. KEYED LOCKS TO ALL OPENING WINDOWS AND SLIDING DOORS

15. INSECT SCREENS TO ALL WINDOWS AND SLIDING DOORS

DATE	DESCRIPTION	REV. NO.
03-02-2026	TECHNICAL UPDATES	H
10-02-2026	TECHNICAL UPDATES	I
18-02-2026	CONSTRUCTION REVIEW	J

PILGRIM retains copyright in all documents and drawings and in any works executed from those documents and drawings.
The PILGRIM reserves all present and future moral rights in all intellectual property in the designs, the documents, drawings and any works executed or to be executed from them.

PILGRIM by agreement grants the client a license to use the documents and drawings to produce the project, for which they were intended, conditional upon the following:

- the license applies only to the site or that part of the site to which the design relates.
- PILGRIM has completed the particular stage or stages of design service for which PILGRIM has been commissioned.
- fees properly due to the designer have been paid in full.

Do not scale from drawings, verify all dimensions prior to commencement of construction or fabrication, notify the designer of any discrepancies.

DRAWING TITLE :

WINDOW SCHEDULE

MADELEINE & NICHOLAS CHILDS

106 HAROLD STREET, HOLLAND PARK

PILGRIM[®]

SCALE :	1 : 50
ABN:	89 639 943 187
QBLCC:	1523 8743
DRAWN :	TH
CHECK BY :	CA
DRAWING NO:	A-07-02
DATE	18-02-2026
REV	J

DOOR SIZES

DOOR NUMBER	TYPE	HEIGHT	WIDTH	FRAME TYPE	LEVEL
GROUND LEVEL					
D01	SECTIONAL PANEL MOTORISED GARAGE DOOR	2340	4800	ALUMINIUM FRAME	GROUND LEVEL
D02	SOLID CORE SINGLE SWING FEATURE DOOR	2340	920	TIMBER FRAME	GROUND LEVEL
D03	GLASS PANEL SLIDING DOOR - FSSF	2400	5384	ALUMINIUM FRAME	GROUND LEVEL
D04	SOLID CORE SINGLE SWING W/ LITE WINDOW	2340	820	TIMBER FRAME	GROUND LEVEL
D05	HOLLOW CORE SINGLE SWING DOOR	2340	820	TIMBER FRAME	GROUND LEVEL
D06	HOLLOW CORE SINGLE SWING DOOR	2340	820	TIMBER FRAME	GROUND LEVEL
D07	HOLLOW CORE SINGLE SWING DOOR	2340	820	TIMBER FRAME	GROUND LEVEL
D08	HOLLOW CORE SINGLE CAVITY SLIDING DOOR	2340	820	TIMBER FRAME	GROUND LEVEL
D09	HOLLOW CORE SINGLE CAVITY SLIDING DOOR	2340	820	TIMBER FRAME	GROUND LEVEL
D10	MIRROR PANEL SLIDING DOOR	2340	2300	TIMBER FRAME	GROUND LEVEL
D11	VINYL PANEL SLIDING DOOR	2340	1600	TIMBER FRAME	GROUND LEVEL

DOOR NUMBER	TYPE	HEIGHT	WIDTH	FRAME TYPE	LEVEL
LEVEL 1					
D12	GLASS PANEL SLIDING DOOR - FSSF	2040	2984	ALUMINIUM FRAME	LEVEL 1
D13	HOLLOW CORE SINGLE CAVITY SLIDING DOOR	2040	820	TIMBER FRAME	LEVEL 1
D14	HOLLOW CORE SINGLE CAVITY SLIDING DOOR	2040	820	TIMBER FRAME	LEVEL 1
D15	HOLLOW CORE SINGLE SWING DOOR	2040	820	TIMBER FRAME	LEVEL 1
D16	HOLLOW CORE SINGLE SWING DOOR	2040	820	TIMBER FRAME	LEVEL 1
D17	HOLLOW CORE SINGLE SWING DOOR	2040	820	TIMBER FRAME	LEVEL 1
D18	HOLLOW CORE SINGLE SWING DOOR	2040	820	TIMBER FRAME	LEVEL 1
D19	HOLLOW CORE SINGLE SWING DOOR	2040	820	TIMBER FRAME	LEVEL 1
D20	HOLLOW CORE SINGLE SWING DOOR	2040	720	TIMBER FRAME	LEVEL 1
D21	HOLLOW CORE SINGLE SWING DOOR	2040	820	TIMBER FRAME	LEVEL 1
D22	HOLLOW CORE SINGLE SWING DOOR	2040	820	TIMBER FRAME	LEVEL 1
D23	MIRROR PANEL SLIDING DOOR	2040	2300	TIMBER FRAME	LEVEL 1
D24	MIRROR PANEL SLIDING DOOR	2040	2000	TIMBER FRAME	LEVEL 1
D25	MIRROR PANEL SLIDING DOOR	2040	2300	TIMBER FRAME	LEVEL 1
D26	SQUARE SET OPENING	2040	900	TIMBER FRAME	LEVEL 1

Grand total: 26

WINDOW SIZES

WINDOW NUMBER	WINDOW TYPE	HEIGHT	WIDTH	HEAD HEIGHT	FRAME TYPE	LEVEL
GROUND LEVEL						
W01	FIXED - FX	300	1060	2750	TIMBER	GROUND LEVEL
W02	FIXED - FX	1500	1510	2400	ALUMINIUM	GROUND LEVEL
W03	SLIDING (2 PANEL) - SF	1200	1800	2400	ALUMINIUM	GROUND LEVEL
W04	SLIDING (2 PANEL) TILE - SF	600	1510	2400	ALUMINIUM	GROUND LEVEL
W05	LOUVRE - L	2100	900	2400	ALUMINIUM	GROUND LEVEL
W06	LOUVRE - L	1800	900	2400	ALUMINIUM	GROUND LEVEL
W07	AWNING - AA	450	2410	1650	ALUMINIUM	GROUND LEVEL
W08	AWNING - AA	450	2410	2400	ALUMINIUM	GROUND LEVEL

WINDOW NUMBER	WINDOW TYPE	HEIGHT	WIDTH	HEAD HEIGHT	FRAME TYPE	LEVEL
LEVEL 1						
W09	FIXED - FX	1800	600	2100	ALUMINIUM	LEVEL 1
W10	FIXED - FX	2100	1210	2100	ALUMINIUM	LEVEL 1
W11	SLIDING (2 PANEL) - SF	600	1810	2100	ALUMINIUM	LEVEL 1
W12	SLIDING (2 PANEL) - SF	900	2110	2100	ALUMINIUM	LEVEL 1
W13	SLIDING (2 PANEL) - SF	900	900	2100	ALUMINIUM	LEVEL 1
W14	SLIDING (2 PANEL) TILE - SF	300	1210	2100	ALUMINIUM	LEVEL 1
W15	SLIDING (2 PANEL) TILE - SF	300	1510	2100	ALUMINIUM	LEVEL 1
W16	SLIDING (2 PANEL) - SF	900	2110	2100	ALUMINIUM	LEVEL 1
W17	SLIDING (2 PANEL) - SF	900	2110	2100	ALUMINIUM	LEVEL 1
W18	SLIDING (4 PANEL) - FSSF	600	3010	2100	ALUMINIUM	LEVEL 1
W19	SLIDING (4 PANEL) - FSSF	900	2110	2100	ALUMINIUM	LEVEL 1
W20	SLIDING (4 PANEL) - FSSF	900	2410	2100	ALUMINIUM	LEVEL 1
W21	AWNING-FIXED - AF	1800	910	2100	ALUMINIUM	LEVEL 1

Grand total: 21

DATE	DESCRIPTION	REV. NO.
03-02-2026	TECHNICAL UPDATES	H
10-02-2026	TECHNICAL UPDATES	I
18-02-2026	CONSTRUCTION REVIEW	J
PILGRIM retains copyright in all documents and drawings and in any works executed from those documents and drawings. The PILGRIM reserves all present and future moral rights in all intellectual property in the designs, the documents, drawings and any works executed or to be executed from them. PILGRIM by agreement grants the client a license to use the documents and drawings to produce the project, for which they were intended, conditional upon the following: - the license applies only to the site or that part of the site to which the design relates. - PILGRIM has completed the particular stage or stages of design service for which PILGRIM has been commissioned. - fees properly due to the designer have been paid in full. Do not scale from drawings; verify all dimensions prior to commencement of construction or fabrication, notify the designer of any discrepancies.		
DRAWING TITLE :		
SIZING SCHEDULE		
MADELEINE & NICHOLAS CHILDS		
106 HAROLD STREET, HOLLAND PARK		
PILGRIM [®]		
SCALE : _____		
ABN: 89 639 943 187 QBCC: 1523 8743		
DRAWN : TH CHECK BY: CA		
DRAWING NO: A-07-09		
DATE	18-02-2026	REV J