


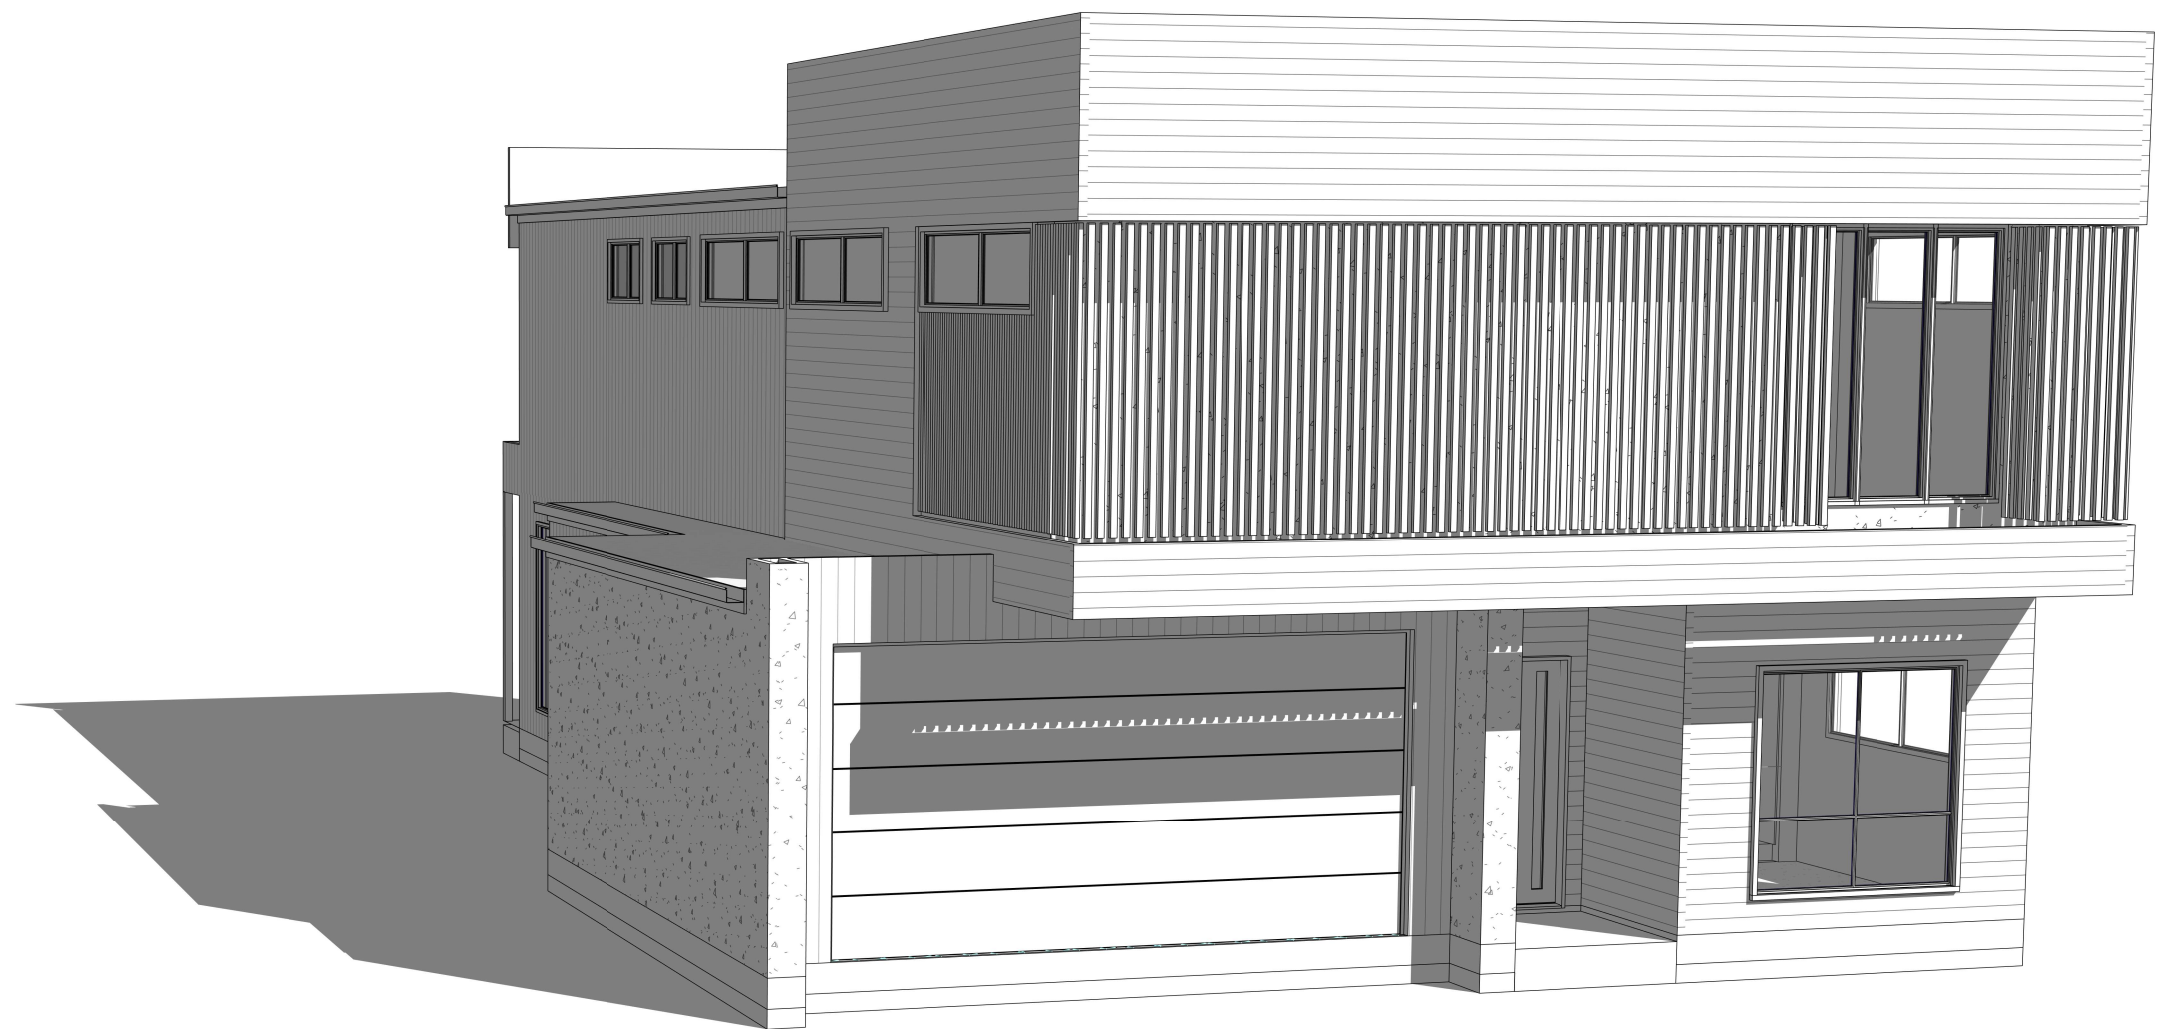

PERSPECTIVE

SHEET NO: 01

A3

CLIENT:
Jared Harder
Pam Harder

PROJECT:
LOT 5 WATEGOS STREET,
TINGALPA, QLD 4173
LOT: 31

SP/DP/PS:
DESIGN: CUSTOM
JOB NO:
SCALE:

REVISIONS:
1
2
3

4
5
DATE: 15/12/2025
ISSUE: CONTRACT DRAWINGS

CLIENT SIGN


MAX SITE COVER:	SITE AREA:	BUILDING AREA:	SITE COVER ACHIEVED:	LOCAL AUTHORITY:	PERMEABILITY:	TERMITE BARRIER:	WIND RATING:	NOISE CAT:	BAL RATING:	SOIL CLASS:	GAS SOURCE:	INTERNET:	POWERLINE	GREYWATER	ROOF MATERIAL	GF CEILING	FF CEILING	BUILD TYPE	CONSTRUCTION TYPE
50%	350m²	165m²	47%	BRISBANE CITY COUNCIL	53%	SMART FILM	N2	N/A	N/A	N/A	N/A	NBN	UNDERGROUND	N/A	COLORBOND	2740	2740	HOUSE	TWO STOREY

NOTES:

Wet areas are to comply with NCC Volume 2 Part H4D2

Exhaust system from bathroom, WC or laundry must be discharged directly or via a shaft or duct to outdoor air, or to a roof space that is ventilated in accordance with H4D7 of the NCC Vol 2 2022

EST FLOOR AREAS - Hip	
Names	Area m2
GF LIVING	104.30
GARAGE	38.81
ALFRESCO	19.43
PORCH	2.13
GF Level	164.67
FF LIVING	118.54
FF Level	118.54
Grand total	283.22

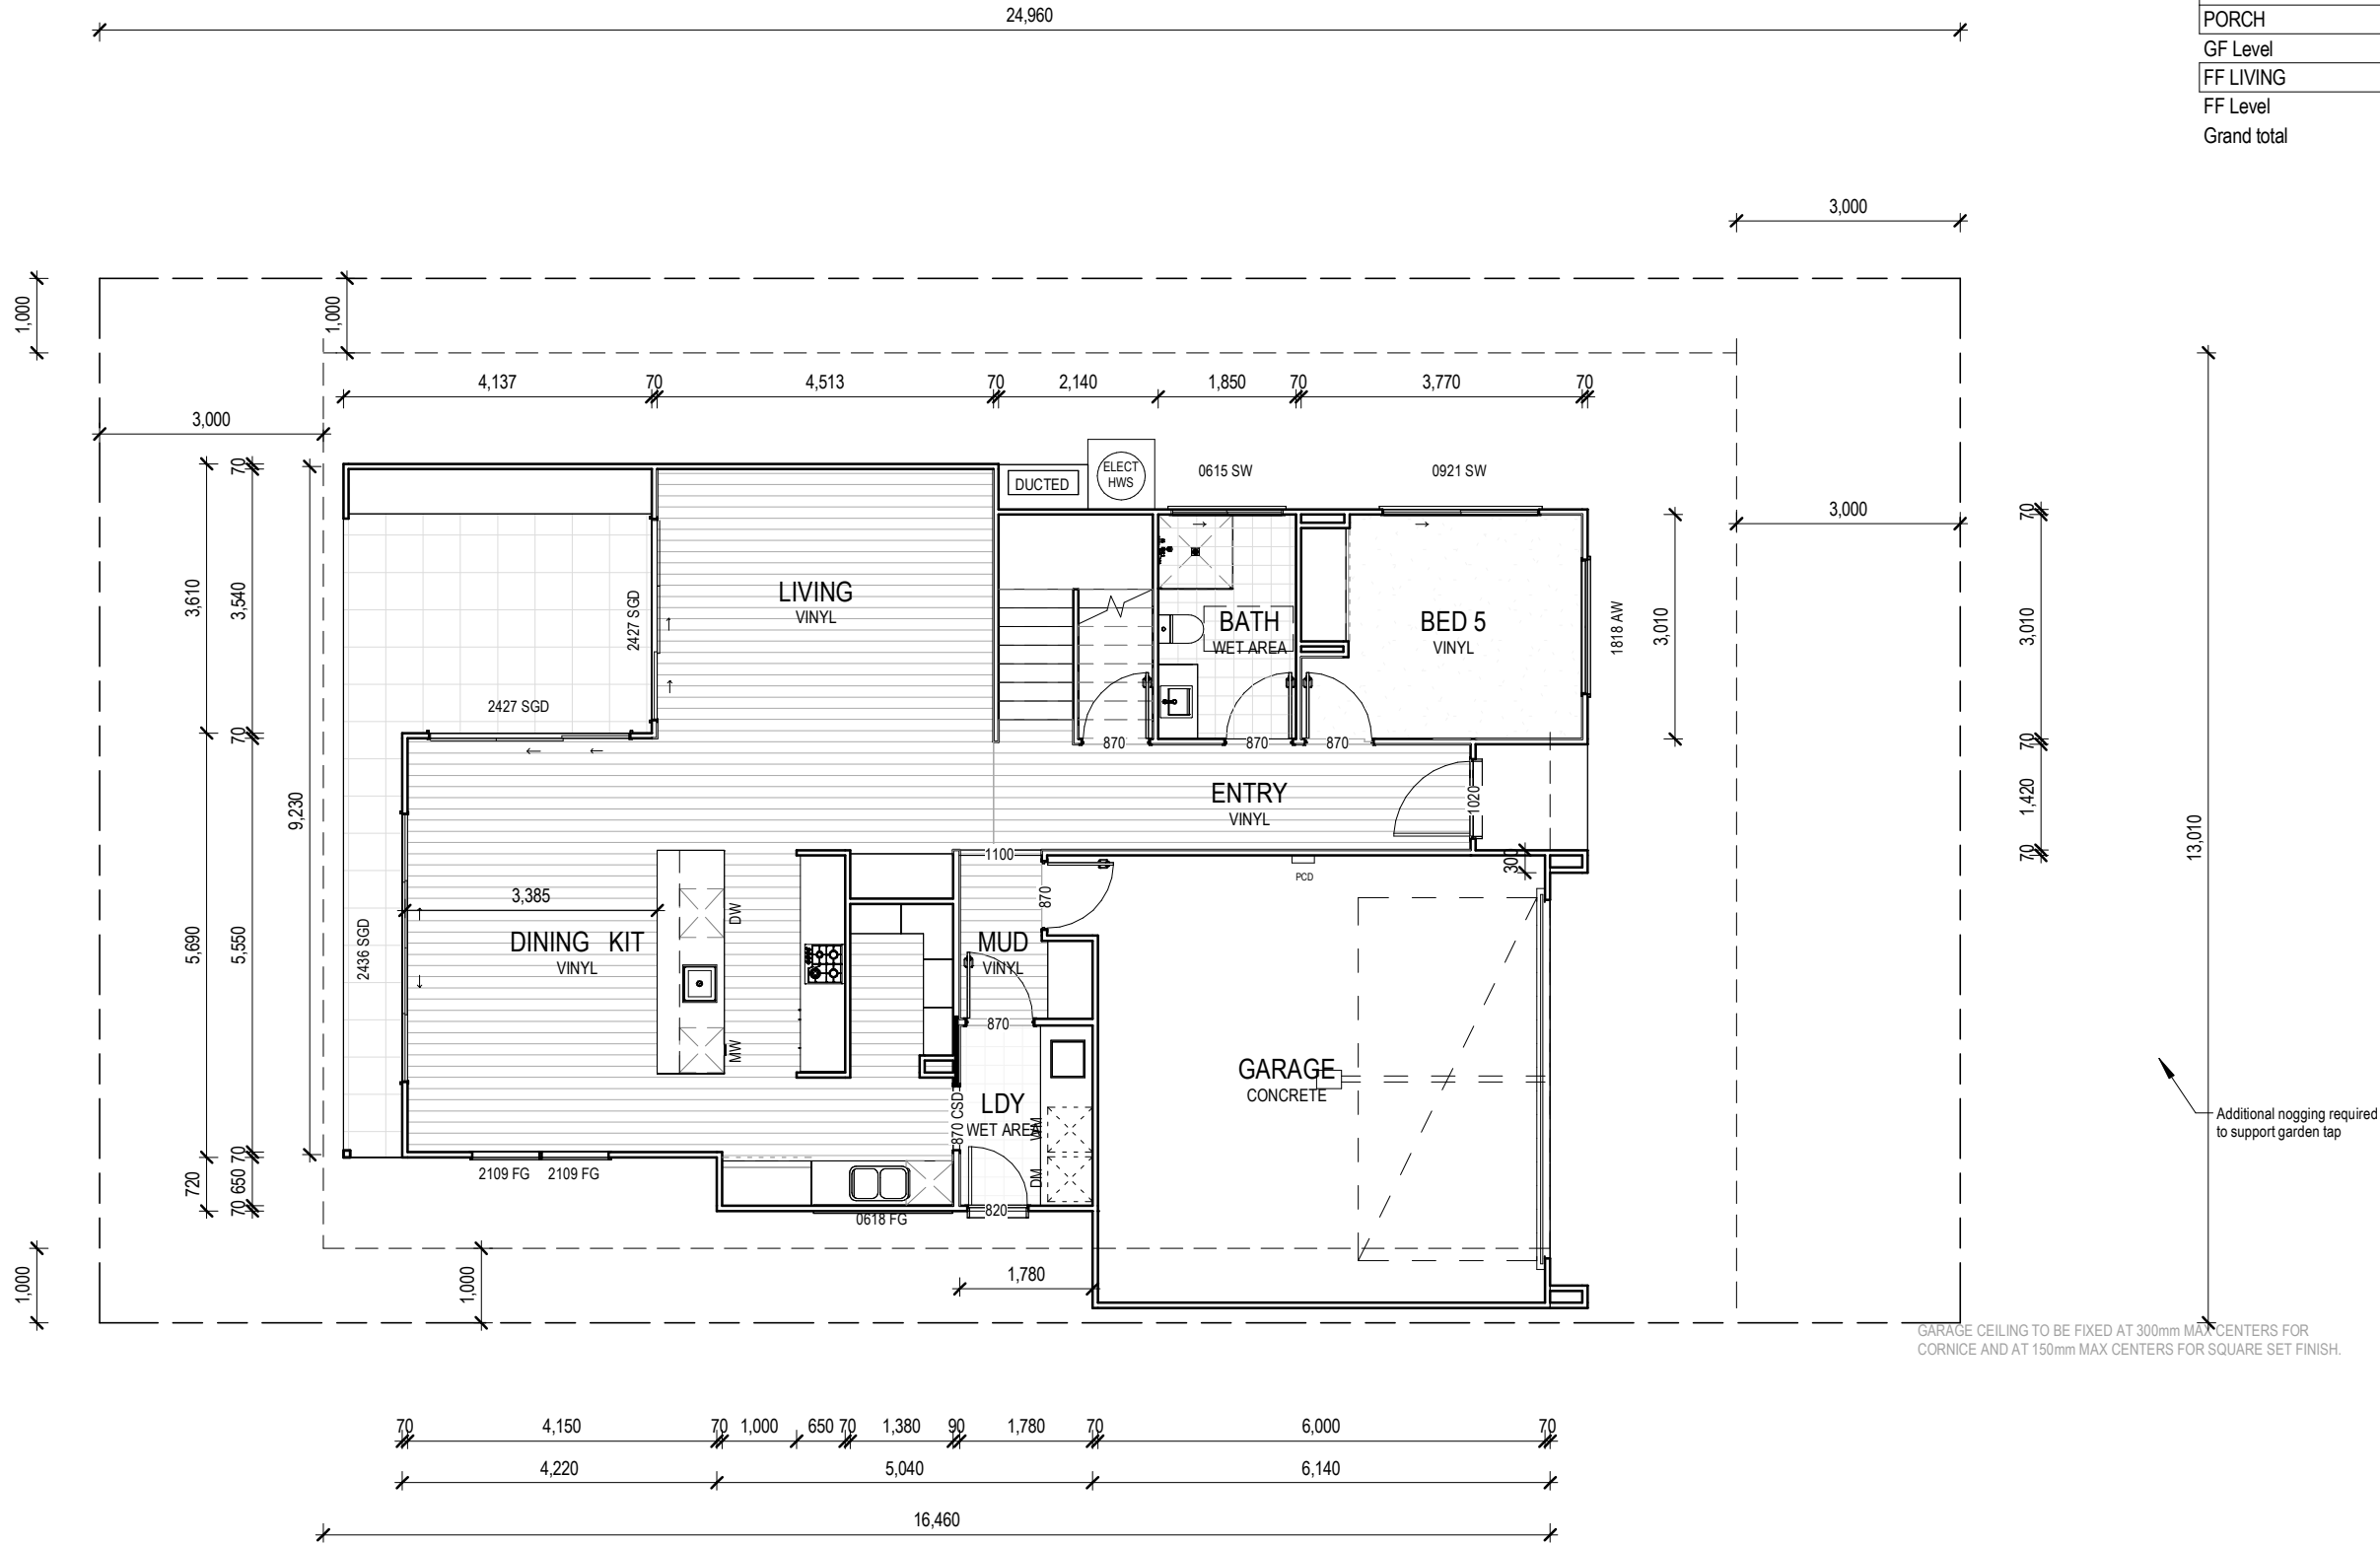

GROUND FLOOR PLAN

SHEET NO: 03

A3

CLIENT:
Jared Harder
Pam Harder

PROJECT:
LOT 5 WATEGOS STREET,
TINGALPA, QLD 4173
LOT: **31**

SP/DP/PS:
DESIGN: **CUSTOM**
JOB NO:
SCALE: **1 : 100**

REVISIONS:
1
2
3

4
5
DATE: **15/12/2025**
ISSUE: **CONTRACT DRAWINGS**

CLIENT SIGN

MAX SITE COVER:	SITE AREA:	BUILDING AREA:	SITE COVER ACHIEVED:	LOCAL AUTHORITY:	PERMEABILITY:	TERMITE BARRIER:	WIND RATING:	NOISE CAT:	BAL RATING:	SOIL CLASS:	GAS SOURCE:	INTERNET:	POWERLINE	GREYWATER	ROOF MATERIAL	GF CEILING	FF CEILING	BUILD TYPE	CONSTRUCTION TYPE
50%	350m²	165m²	47%	BRISBANE CITY COUNCIL	53%	SMART FILM	N2	N/A	N/A	N/A	N/A	NBN	UNDERGROUND	N/A	COLORBOND	2740	2740	HOUSE	TWO STOREY


NOTES:

Wet areas are to comply with NCC Volume 2 2022
PART H4D2

Exhaust system from bathroom, WC or laundry must be
discharged directly or via a shaft or duct to outdoor air,
or to a roof space that is ventilated in accordance with
H4D7 of the NCC Vol 2 2022

Window openings in bedrooms must be provided with
fall protection where the opening is less than 1700mm
above the floor and the finished ground outside the
window is 2m or greater below the bedroom floor, in
accordance with NCC Vol 2 2022

EST FLOOR AREAS - Hip	
Names	Area m2
GF LIVING	104.30
GARAGE	38.81
ALFRESCO	19.43
PORCH	2.13
GF Level	164.67
FF LIVING	118.54
FF Level	118.54
Grand total	283.22

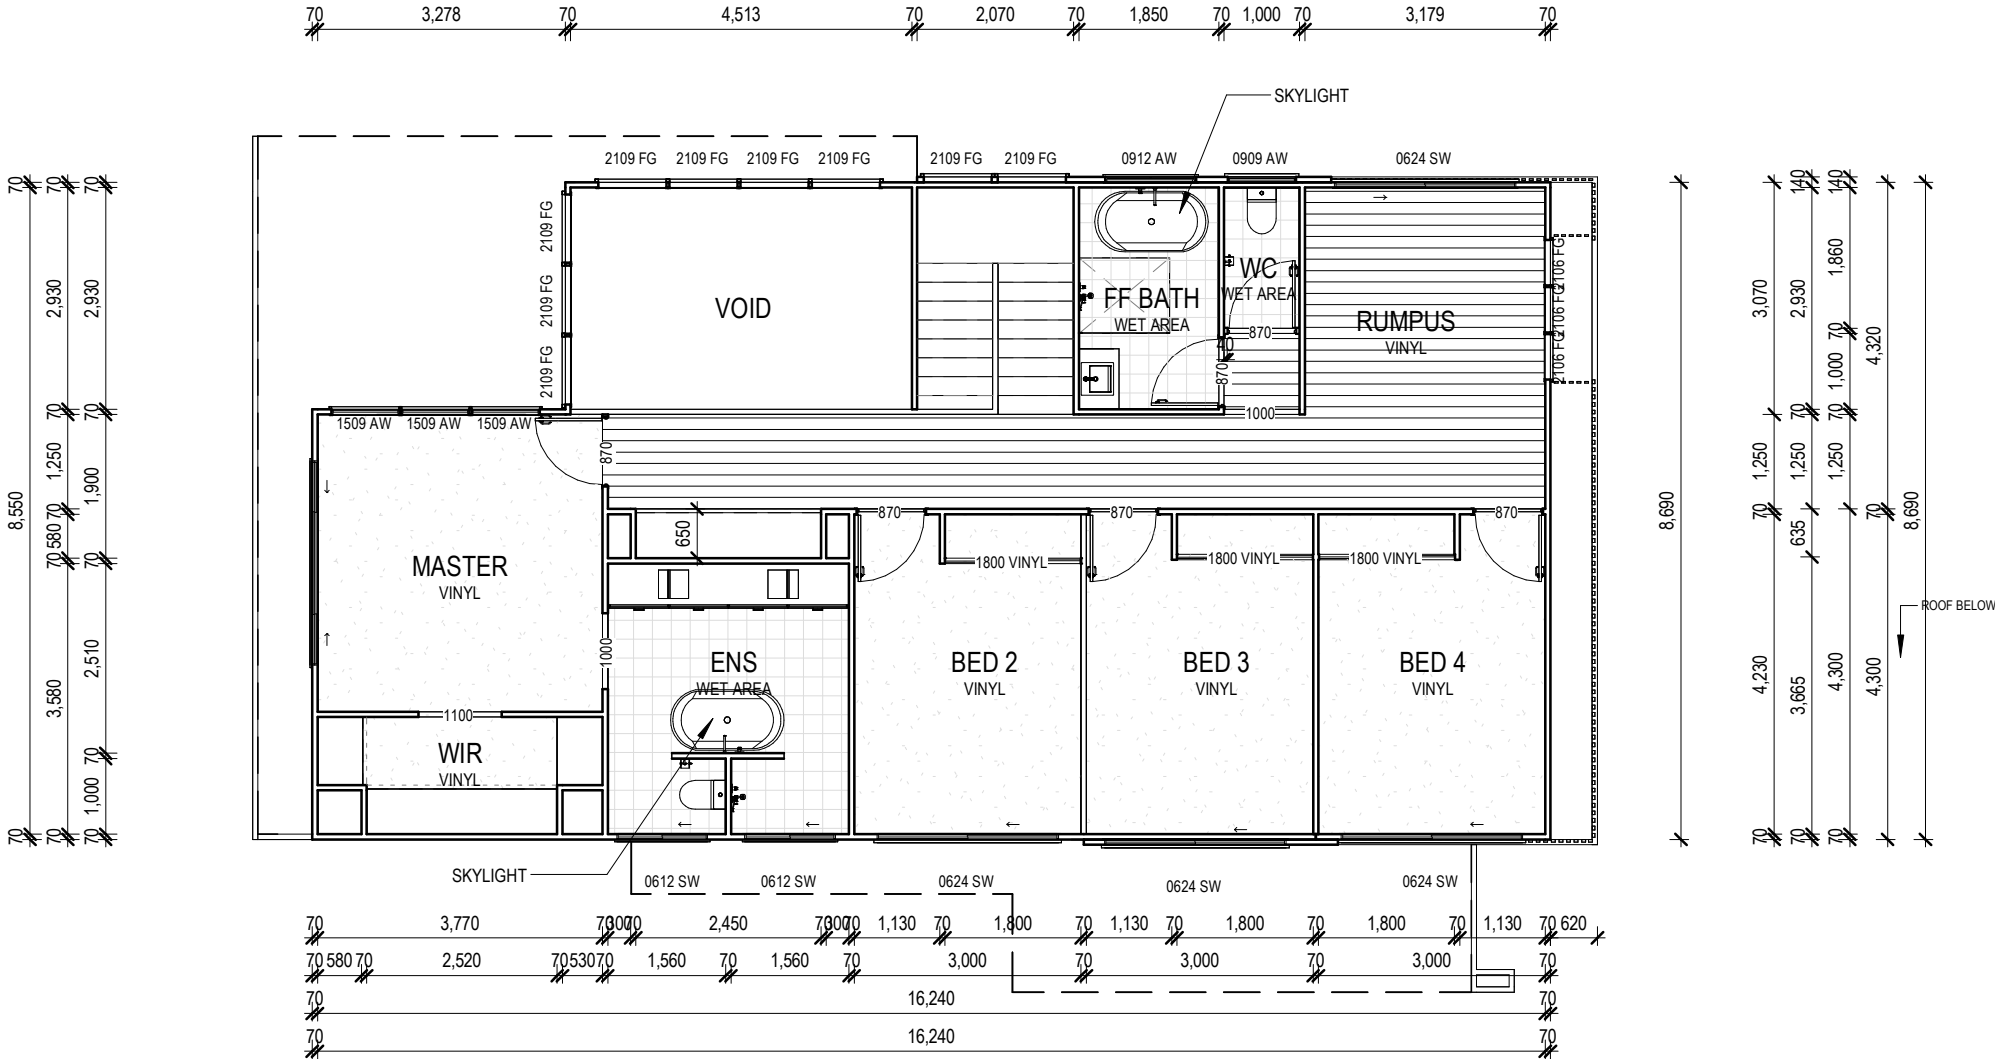

FIRST FLOOR PLAN

SHEET NO: 03a

A3

CLIENT:
Jared Harder
Pam Harder

PROJECT:
LOT 5 WATEGOS STREET,
TINGALPA, QLD 4173
LOT: 31

SP/DP/PS:
DESIGN: CUSTOM
JOB NO:
SCALE: 1 : 100

REVISIONS:
1
2
3

4
5
DATE: 15/12/2025
ISSUE: CONTRACT DRAWINGS

CLIENT SIGN

MAX SITE COVER:	SITE AREA:	BUILDING AREA:	SITE COVER ACHIEVED:	LOCAL AUTHORITY:	PERMEABILITY:	TERMITE BARRIER:	WIND RATING:	NOISE CAT:	BAL RATING:	SOIL CLASS:	GAS SOURCE:	INTERNET:	POWERLINE	GREYWATER	ROOF MATERIAL	GF CEILING	FF CEILING	BUILD TYPE	CONSTRUCTION TYPE
50%	350m²	165m²	47%	BRISBANE CITY COUNCIL	53%	SMART FILM	N2	N/A	N/A	N/A	N/A	NBN	UNDERGROUND	N/A	COLORBOND	2740	2740	HOUSE	TWO STOREY



1

Elevation A

1 : 100



2

Elevation B

1 : 100



ELEVATION 1

SHEET NO: 04

A3

CLIENT:
Jared Harder
Pam Harder

PROJECT:
LOT 5 WATEGOS STREET,
TINGALPA, QLD 4173
LOT: 31

SP/DP/PS:
DESIGN: CUSTOM
JOB NO:
SCALE: 1 : 100

REVISIONS:
1
2
3

4
5
DATE: 15/12/2025
ISSUE: CONTRACT DRAWINGS

CLIENT SIGN

MAX SITE COVER:	SITE AREA:	BUILDING AREA:	SITE COVER ACHIEVED:	LOCAL AUTHORITY:	PERMEABILITY:	TERMITE BARRIER:	WIND RATING:	NOISE CAT:	BAL RATING:	SOIL CLASS:	GAS SOURCE:	INTERNET:	POWERLINE	GREYWATER	ROOF MATERIAL	GF CEILING	FF CEILING	BUILD TYPE	CONSTRUCTION TYPE
50%	350m²	165m²	47%	BRISBANE CITY COUNCIL	53%	SMART FILM	N2	N/A	N/A	N/A	N/A	NBN	UNDERGROUND	N/A	COLORBOND	2740	2740	HOUSE	TWO STOREY



1 Elevation C
1 : 100



2 Elevation D
1 : 100



ELEVATION 2
SHEET NO: 04a

A3

CLIENT:
Jared Harder
Pam Harder

PROJECT:
LOT 5 WATEGOS STREET,
TINGALPA, QLD 4173
LOT: 31

SP/DP/PS:
DESIGN: CUSTOM
JOB NO:
SCALE: 1 : 100

REVISIONS:
1
2
3

4
5
DATE: 15/12/2025
ISSUE: CONTRACT DRAWINGS

CLIENT SIGN

MAX SITE COVER:	SITE AREA:	BUILDING AREA:	SITE COVER ACHIEVED:	LOCAL AUTHORITY:	PERMEABILITY:	TERMITE BARRIER:	WIND RATING:	NOISE CAT:	BAL RATING:	SOIL CLASS:	GAS SOURCE:	INTERNET:	POWERLINE	GREYWATER	ROOF MATERIAL	GF CEILING	FF CEILING	BUILD TYPE	CONSTRUCTION TYPE
50%	350m²	165m²	47%	BRISBANE CITY COUNCIL	53%	SMART FILM	N2	N/A	N/A	N/A	N/A	NBN	UNDERGROUND	N/A	COLORBOND	2740	2740	HOUSE	TWO STOREY

ELECTRICAL LEGEND

SOLAR PANEL

CEILING FAN

CEILING FANLIGHT (FLURO)

EXHAUST 3 IN 1

EXHAUST FAN

SMOKE ALARM

HEAT LAMP

GAS OUTLET

TV POINT

PHONE POINT

DATA POINT

DOWNLIGHT 240V

BATTEN HOLDER

PENDANT

SINGLE GPO

DOUBLE GPO

ROOF SINGLE GPO

WATERPROOF SINGLE GPO

WATERPROOF DOUBE GPO

WALL LIGHT

FLOOD/SPOT LIGHT

FLOOD/SPOT LIGHT

SENSOR


SGL FLURO TUBE 18W

DBL FLURO TUBE 36W


ISOLATION SWITCH

SWITCH

ELECTRICAL POINTS POSITIONS SUBJECT TO CONSTRUCTION CONSTRAINTS

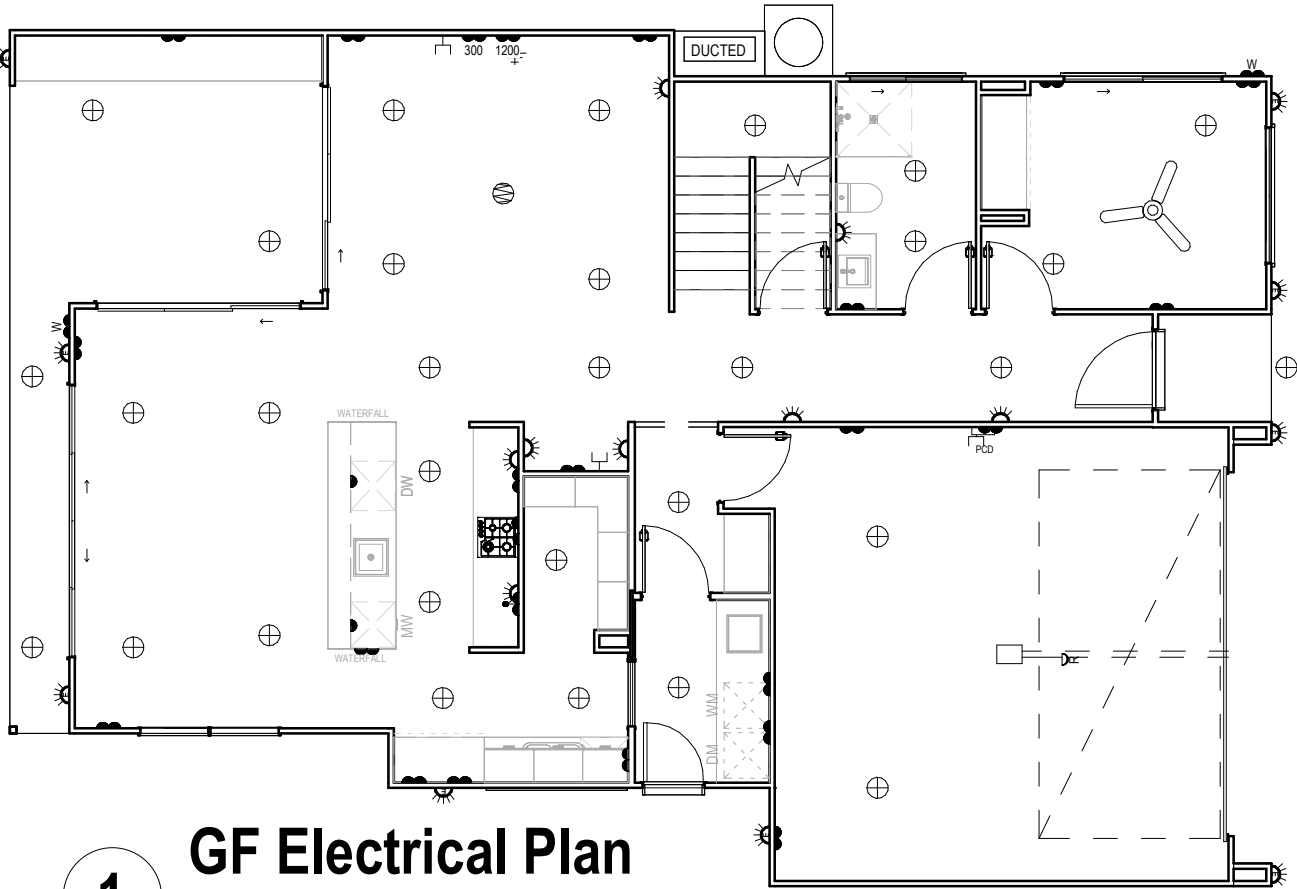

1 GF Electrical Plan
1 : 100

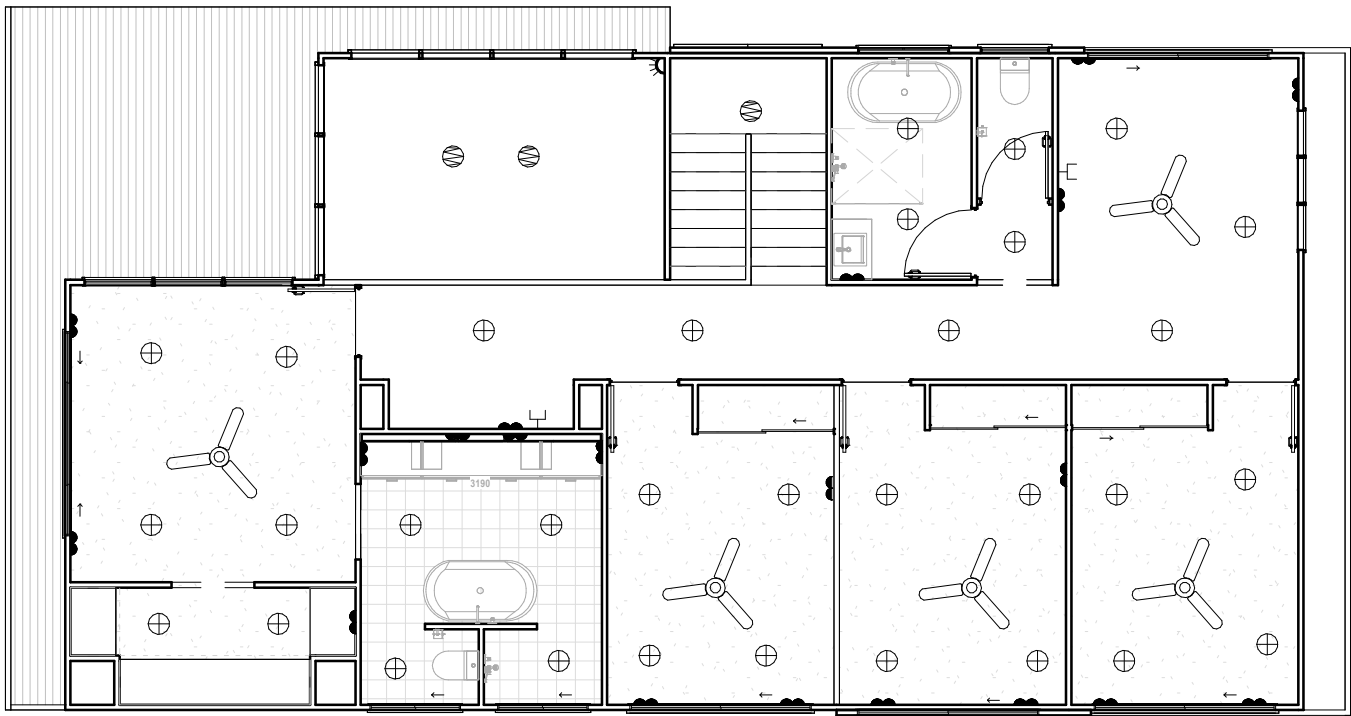

2 FF Electrical Plan
1 : 100

REQUIREMENTS FOR SMOKE ALARMS LEGISLATION
SMOKE ALARMS MUST BE INSTALLED IN A CLASS 1A TO COMPLY WITH H3D6 OF NCC VOL 2 2022 AND AS 3786 - 2014.

- SMOKE ALARMS MUST BE PHOTOELECTRIC TYPE.
- SMOKE ALARMS ARE TO BE HARD-WIRED AND HAVE A BATTERY BACK-UP POWER SUPPLY.
- SMOKE ALARM LOCATION - MUST BE INSTALLED IN ANY STOREY CONTAINING BEDROOMS & IN EVERY BEDROOM, BETWEEN EACH PART OF THE DWELLING CONTAINING BEDROOMS & THE REMAINDER OF THE DWELLING & ON ANY OTHER STOREY NOT CONTAINING BEDROOMS.
- ALL SMOKE ALARMS ARE TO BE INTERCONNECTED.

PROVIDE A FORM 16 BY A LICENSED ELECTRICIAN ON THE FINAL INSPECTION.

REQUIREMENTS FOR SMOKE ALARMS LOCATIONS
WHERE PRACTICABLE SMOKE ALARMS MUST BE PLACED ON THE CEILING. SMOKE ALARMS MUST NOT BE PLACED:

- i) WITHIN 300mm OF A CORNER OF A CEILING AND A WALL;
- ii) WITHIN 300mm OF A LIGHT FITTING;
- iii) WITHIN 400mm OF AN AIR-CONDITIONING VENT;
- iv) WITHIN 400mm OF THE BLADES OF A CEILING FAN.

ENERGY EFFICIENCY REPORT
REQUIREMENTS OF ENERGY EFFICIENCY REPORT FOR THIS DEVELOPMENT MUST BE CARRIED OUT AS PART OF THE PROPOSED DEVELOPMENT TO COMPLY WITH THE QDC 4.1 AND THE NCC, PART H6. A FORM 16 - ASPECT CERTIFICATE TO CONFIRM COMPLIANCE WITH THE ENERGY REQUIREMENTS IS TO BE PROVIDED AT FINAL INSPECTION. REFER TO THE APPROVED ENERGY REPORT.

NBN ESTATE
NBN ESTATE - NATIONAL BROADBAND NETWORK. PLEASE THE JOB SUPERVISOR TO ENSURE THE CORRECT METHOD OF INSTALLATION IS IMPLEMENTED.

EST ELECTRICAL FIXTURES	
Type	Count
Ceiling Fan	6
Data Point	5
dGPO	31
dGPO - AB	5
dGPO - LS	1
dGPO Bath	5
dGPO-Fridge	2
dGPO-Waterproof	2
Downlight	63
External Wall Light	9
Internal	10
Pendant	4
sGPO	4
sGPO-Roof	1
TV Point	1

149




- CARPET
- CONCRETE
- COVERCRETE
- TILES - EXTERNAL
- TILES - INTERNAL
- TILES - WET AREA
- VINYL

EST ROOM AREA, PERIMETER & CEILING FINISHES			
Room Name	Floor/Ceiling Area m2	Room Perimeter m	Ceiling & Cornice Finish
BATH	5.57	9.720 m	
BED 5	11.10	14.830 m	
DINING KIT	43.13	40.622 m	
ENTRY	15.25	27.960 m	
GARAGE	36.73	25.360 m	
LDY	4.30	8.396 m	
LIVING	16.29	16.165 m	
MUD	3.12	7.944 m	
BED 2	11.47	14.460 m	
BED 3	11.57	14.460 m	
BED 4	11.57	14.460 m	
ENS	11.25	18.500 m	
FF BATH	5.42	9.560 m	
MASTER	14.82	15.400 m	
RUMPUS	32.63	46.598 m	
VOID	13.22	14.886 m	
WC	1.86	5.720 m	
WIR	5.03	10.640 m	
	254.33	315.681 m	
Grand total	254.33	315.681 m	

1 GF Room Area
1 : 100

EST FLOOR COVERINGS			
Level	Finish	Mark	Area
GF Level	Carpet	GUEST BED	10.17 m²
FF Level	Carpet		55.52 m²
			65.69 m²
GF Level	External Tiles		16.91 m²
			16.91 m²
GF Level	Vinyl	ENTRY	12.00 m²
GF Level	Vinyl	MAIN LIVING	58.38 m²
FF Level	Vinyl		26.49 m²
			96.87 m²
GF Level	Wet Area	GF BATH	5.60 m²
GF Level	Wet Area	LDY MUD	2.80 m²
FF Level	Wet Area	FF BATH	5.42 m²
FF Level	Wet Area	FF WC	1.86 m²
FF Level	Wet Area	MASTER ENS	10.78 m²
			26.46 m²

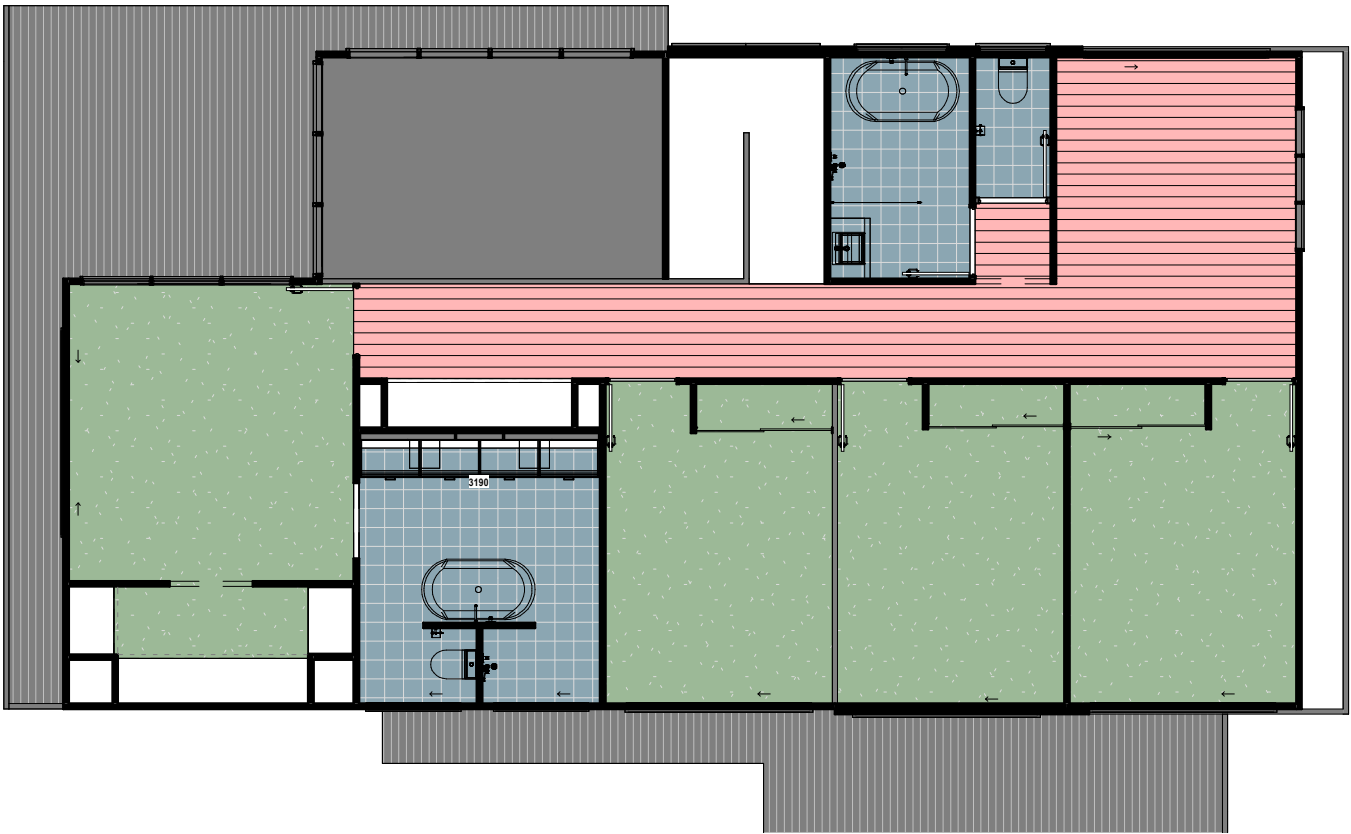

2 FF Room Area
1 : 100



ROOM AREAS

SHEET NO: 10

A3

CLIENT:
Jared Harder
Pam Harder


PROJECT:
LOT 5 WATEGOS STREET,
TINGALPA, QLD 4173
LOT: 31

SP/DP/PS:
DESIGN: CUSTOM
JOB NO:
SCALE: 1 : 100


REVISIONS:
1
2
3

4
5
DATE: 15/12/2025
ISSUE: CONTRACT DRAWINGS


CLIENT SIGN

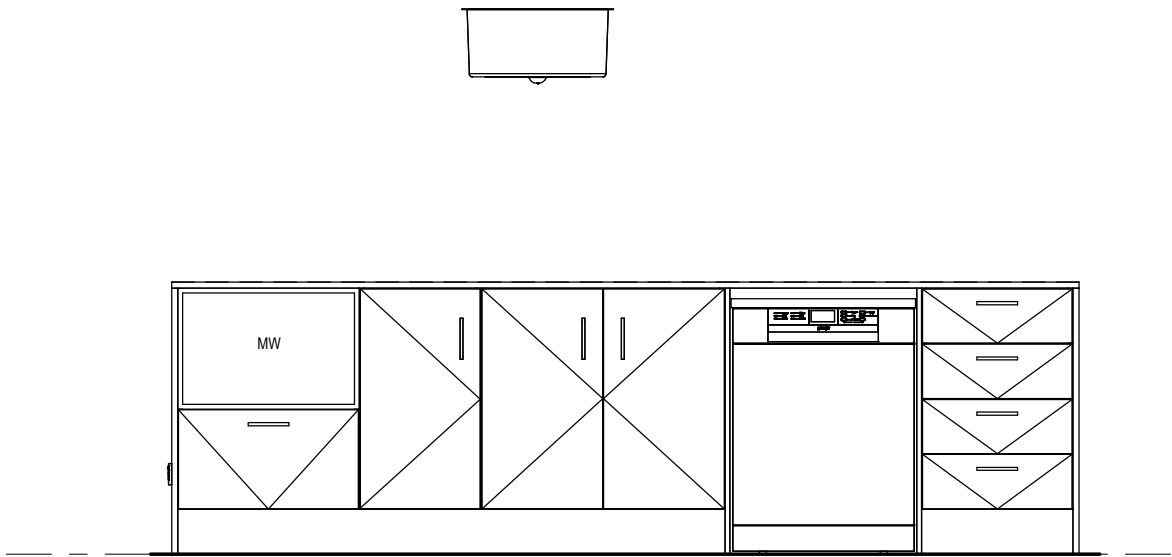


KIT A
1 : 25

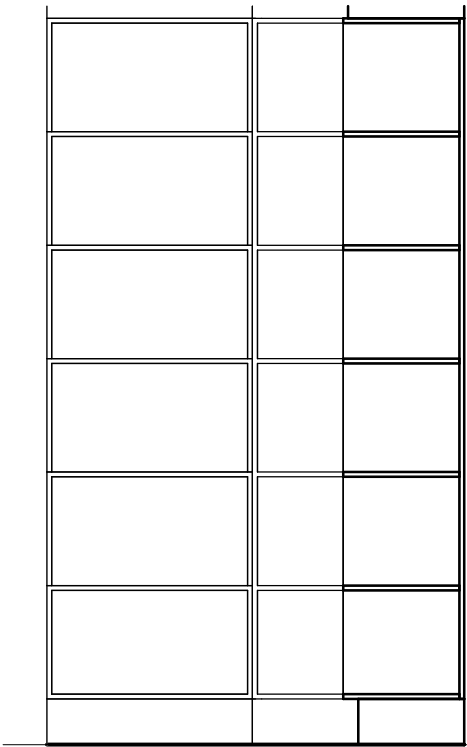


KIT B
1 : 25

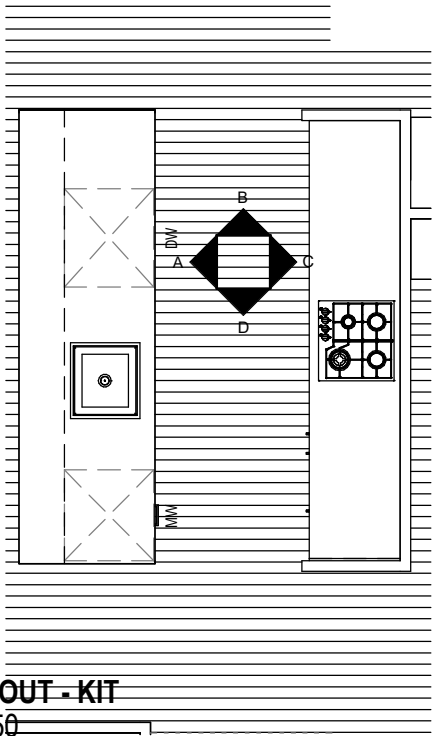

LAYOUT - KIT
1 : 50

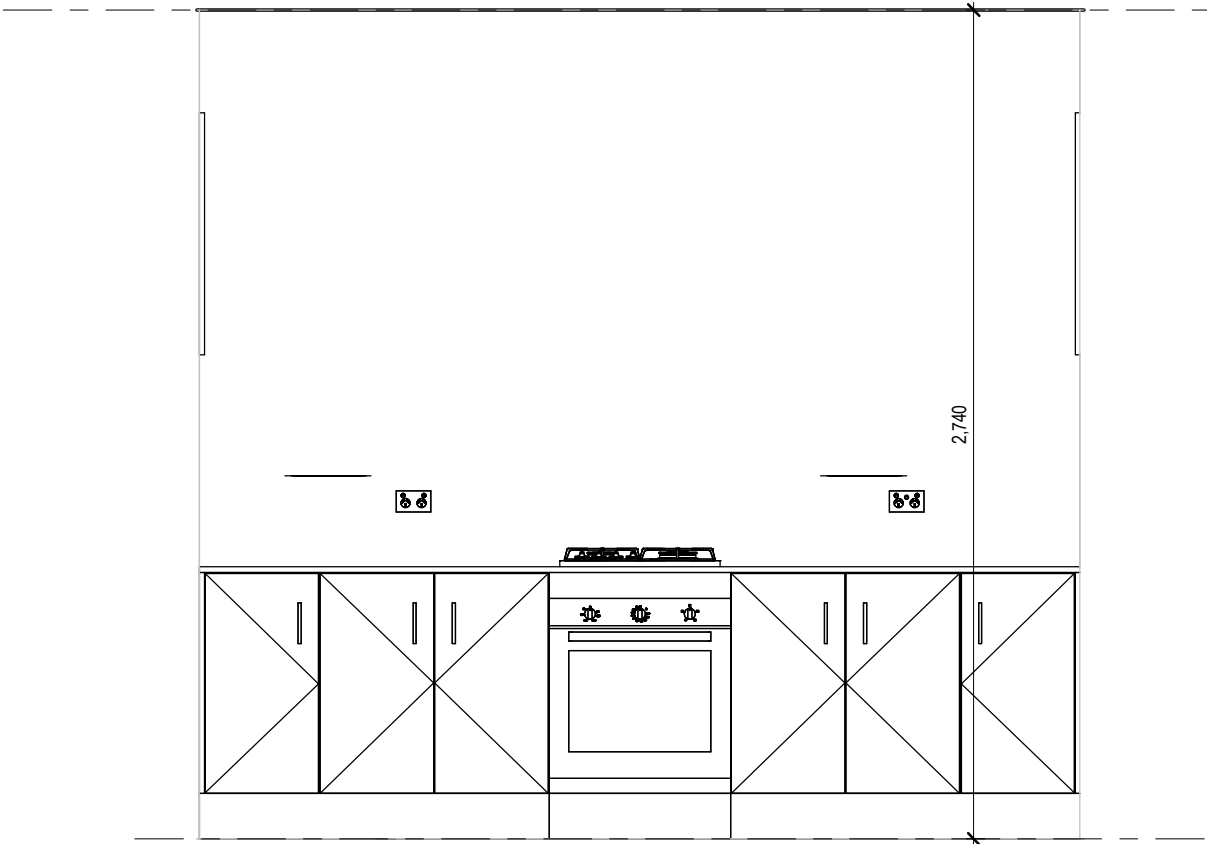

KIT C
1 : 25

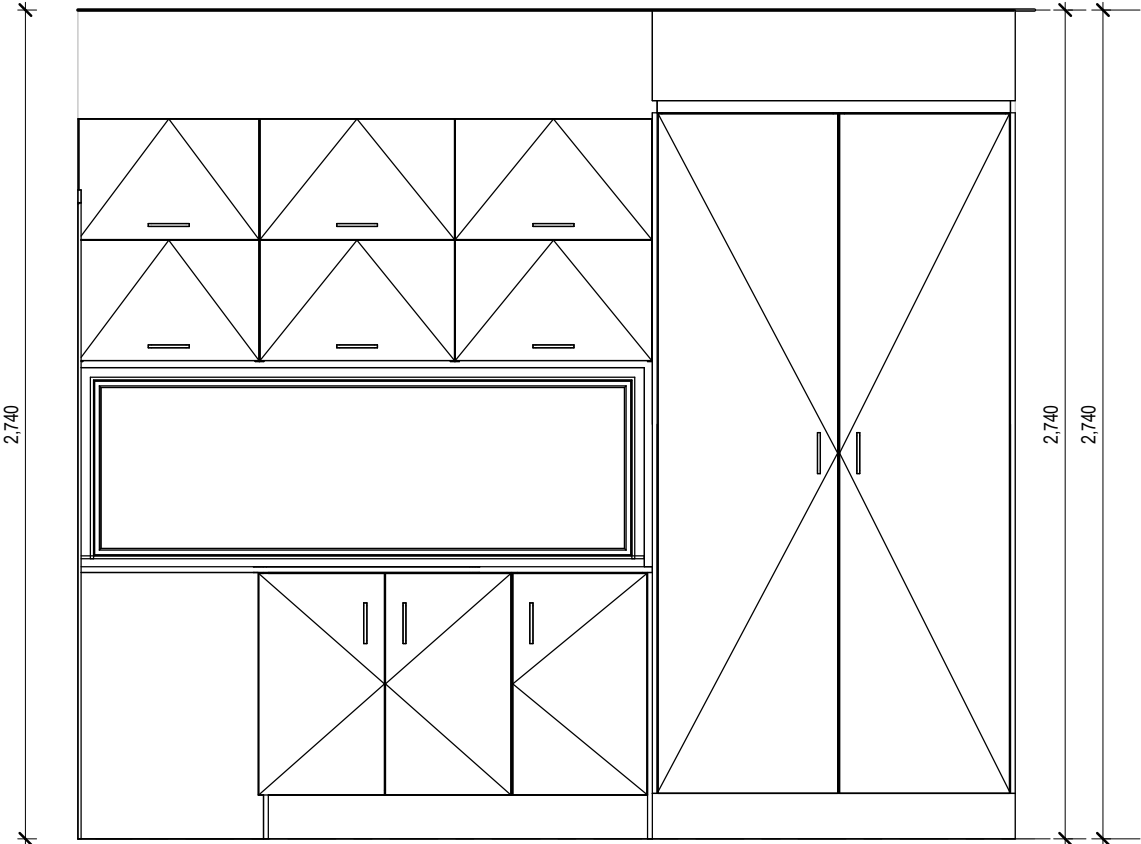

KIT D
1 : 25

EST KITCHEN TILES AREA

Type	Area m2
------	---------



CABINETRY DETAIL 1

SHEET NO: 101 - KIT

A3

CLIENT:
Jared Harder
Pam Harder


PROJECT:
LOT 5 WATEGOS STREET,
TINGALPA, QLD 4173
LOT: 31

SP/DP/PS:
DESIGN: CUSTOM
JOB NO:
SCALE: As indicated


REVISIONS:
1
2
3

4
5
DATE: 15/12/2025
ISSUE: CONTRACT DRAWINGS


CLIENT SIGN

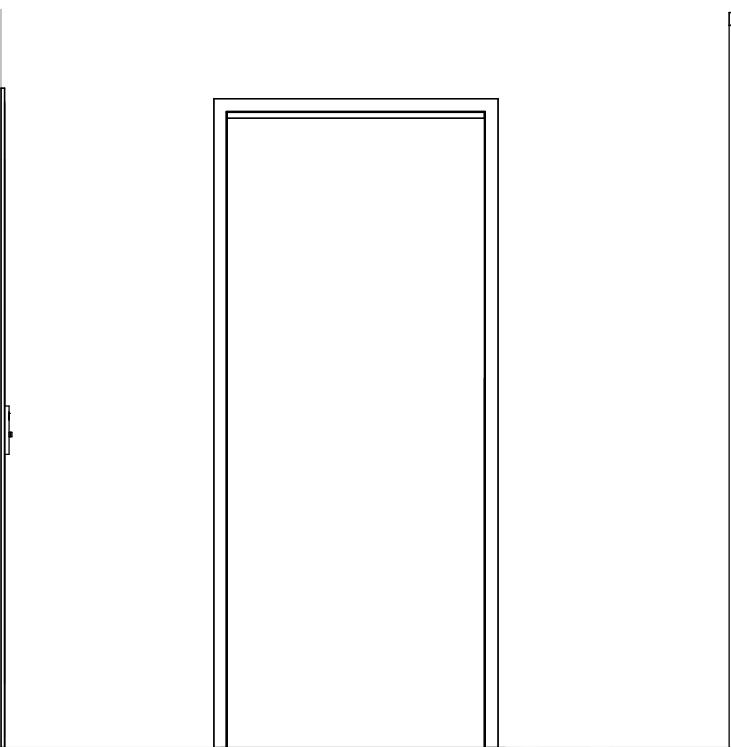


LDY A
1 : 25

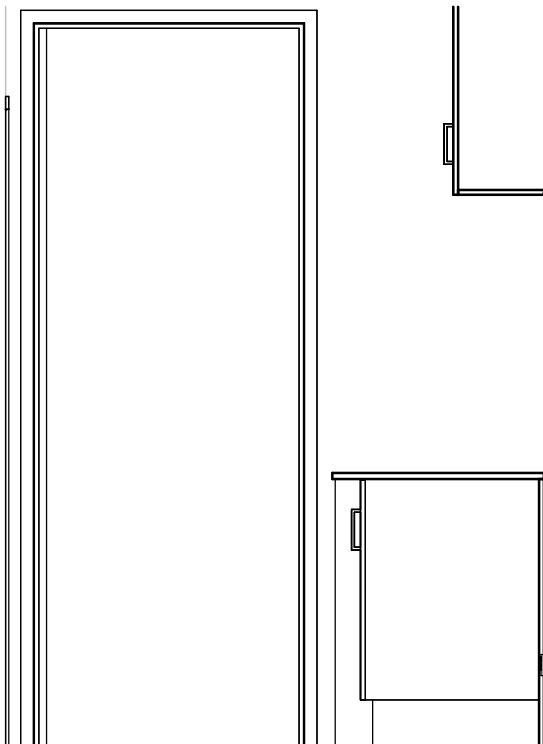

LDY B
1 : 25

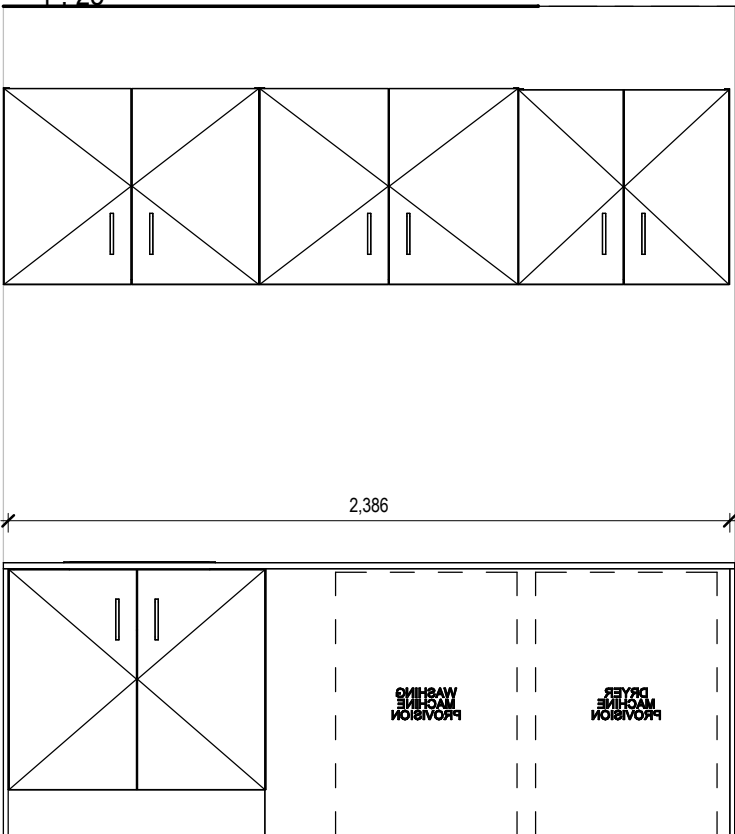

LDY D
1 : 25

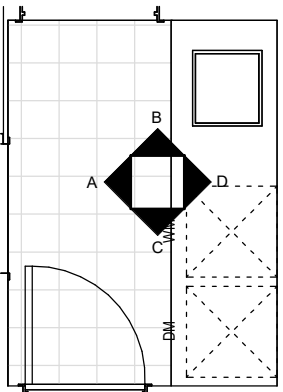

LAYOUT - LDY
1 : 50

EST LAUNDRY TILES AREA

Type	Area m2
------	---------



CABINETRY DETAIL 2

SHEET NO: 102 - LDY

A3

CLIENT:
Jared Harder
Pam Harder

PROJECT:
LOT 5 WATEGOS STREET,
TINGALPA, QLD 4173
LOT: 31

SP/DP/PS:
DESIGN: CUSTOM
JOB NO:
SCALE: As indicated


REVISIONS:
1
2
3

4
5
DATE: 15/12/2025
ISSUE: CONTRACT DRAWINGS


CLIENT SIGN

1,850

INDICATIVE ONLY SUBJECT TO CHANGE DUE TO PRODUCT SIZE AND FINAL MEASURE

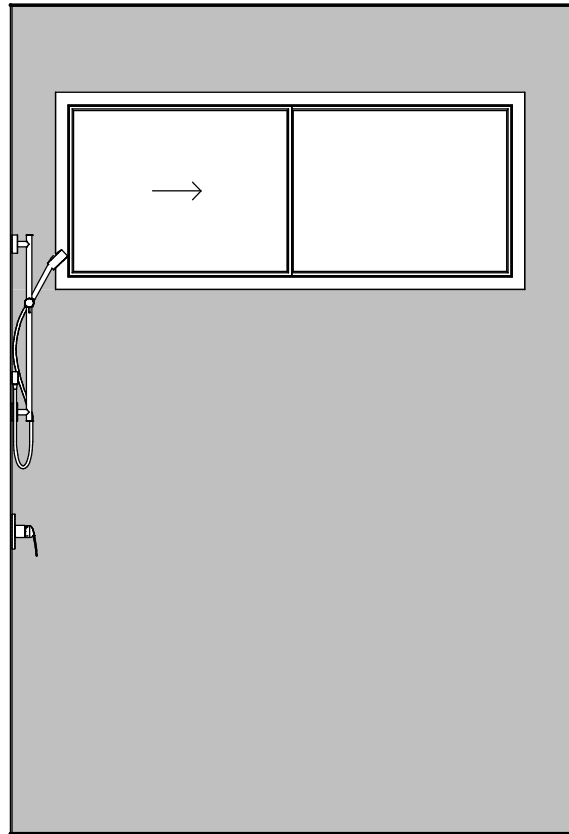


BATH A
1 : 25

 


BATH B
1 : 25

ELECT
HWS


500
500

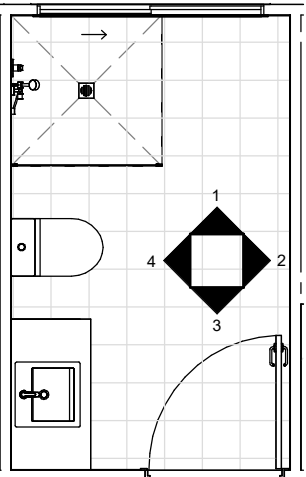

LAYOUT - BATH
1 : 50

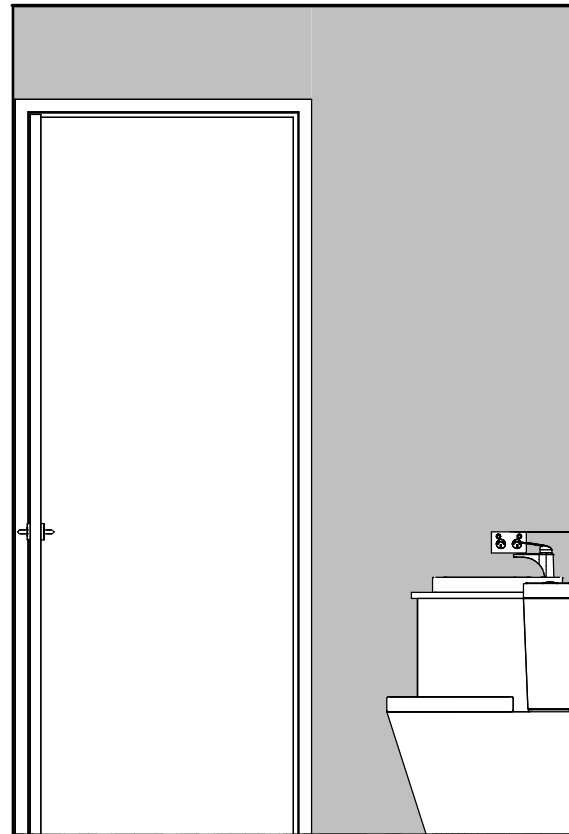

BATH C
1 : 25

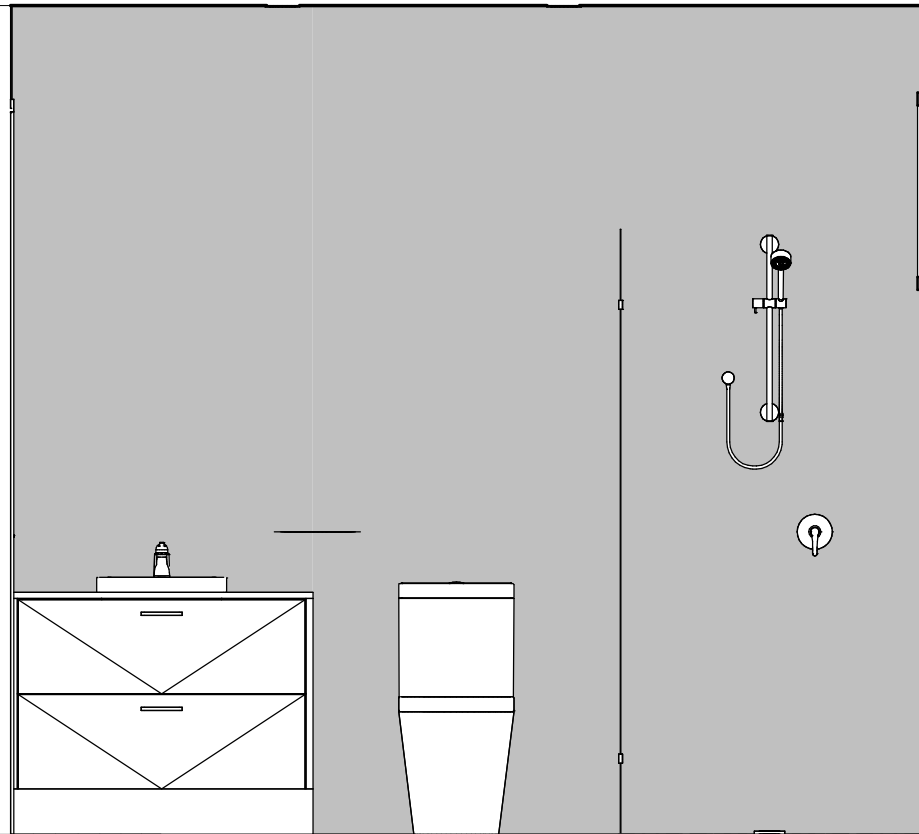

EST BATHS TILES AREA

Type	Area m2
Bath Shower	22.41
TOTAL	22.41



CABINETRY DETAIL 3

SHEET NO: 103 - BATH

BATH D
1 Jan 25
Pam Harder

A3

PROJECT:
LOT 5 WATEGOS STREET,
TINGALPA, QLD 4173


LOT: 31

SP/DP/PS:
DESIGN: CUSTOM
JOB NO:
SCALE: As indicated

REVISIONS:
1
2
3



4
5
DATE: 15/12/2025
ISSUE: CONTRACT DRAWINGS

CLIENT SIGN

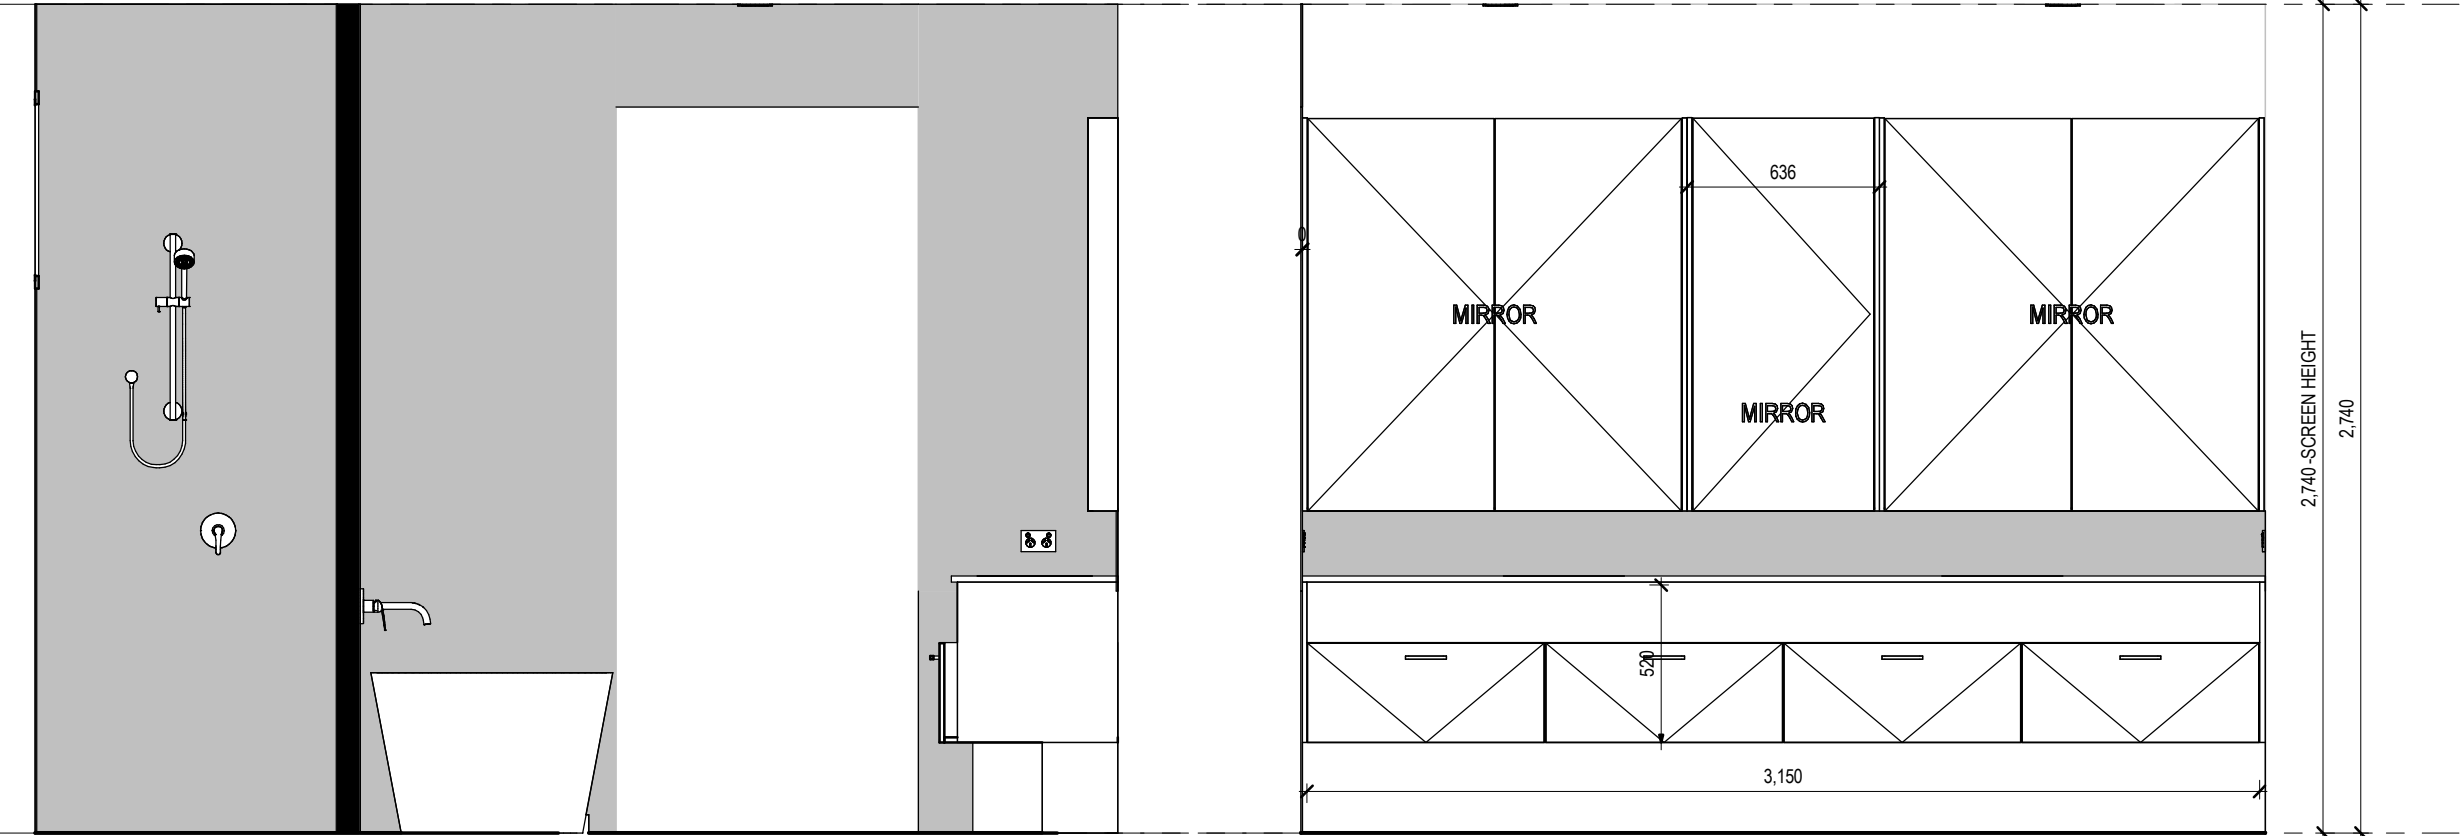

FF ENS A
1 : 25

LAYOUT - FF ENS
1 : 50

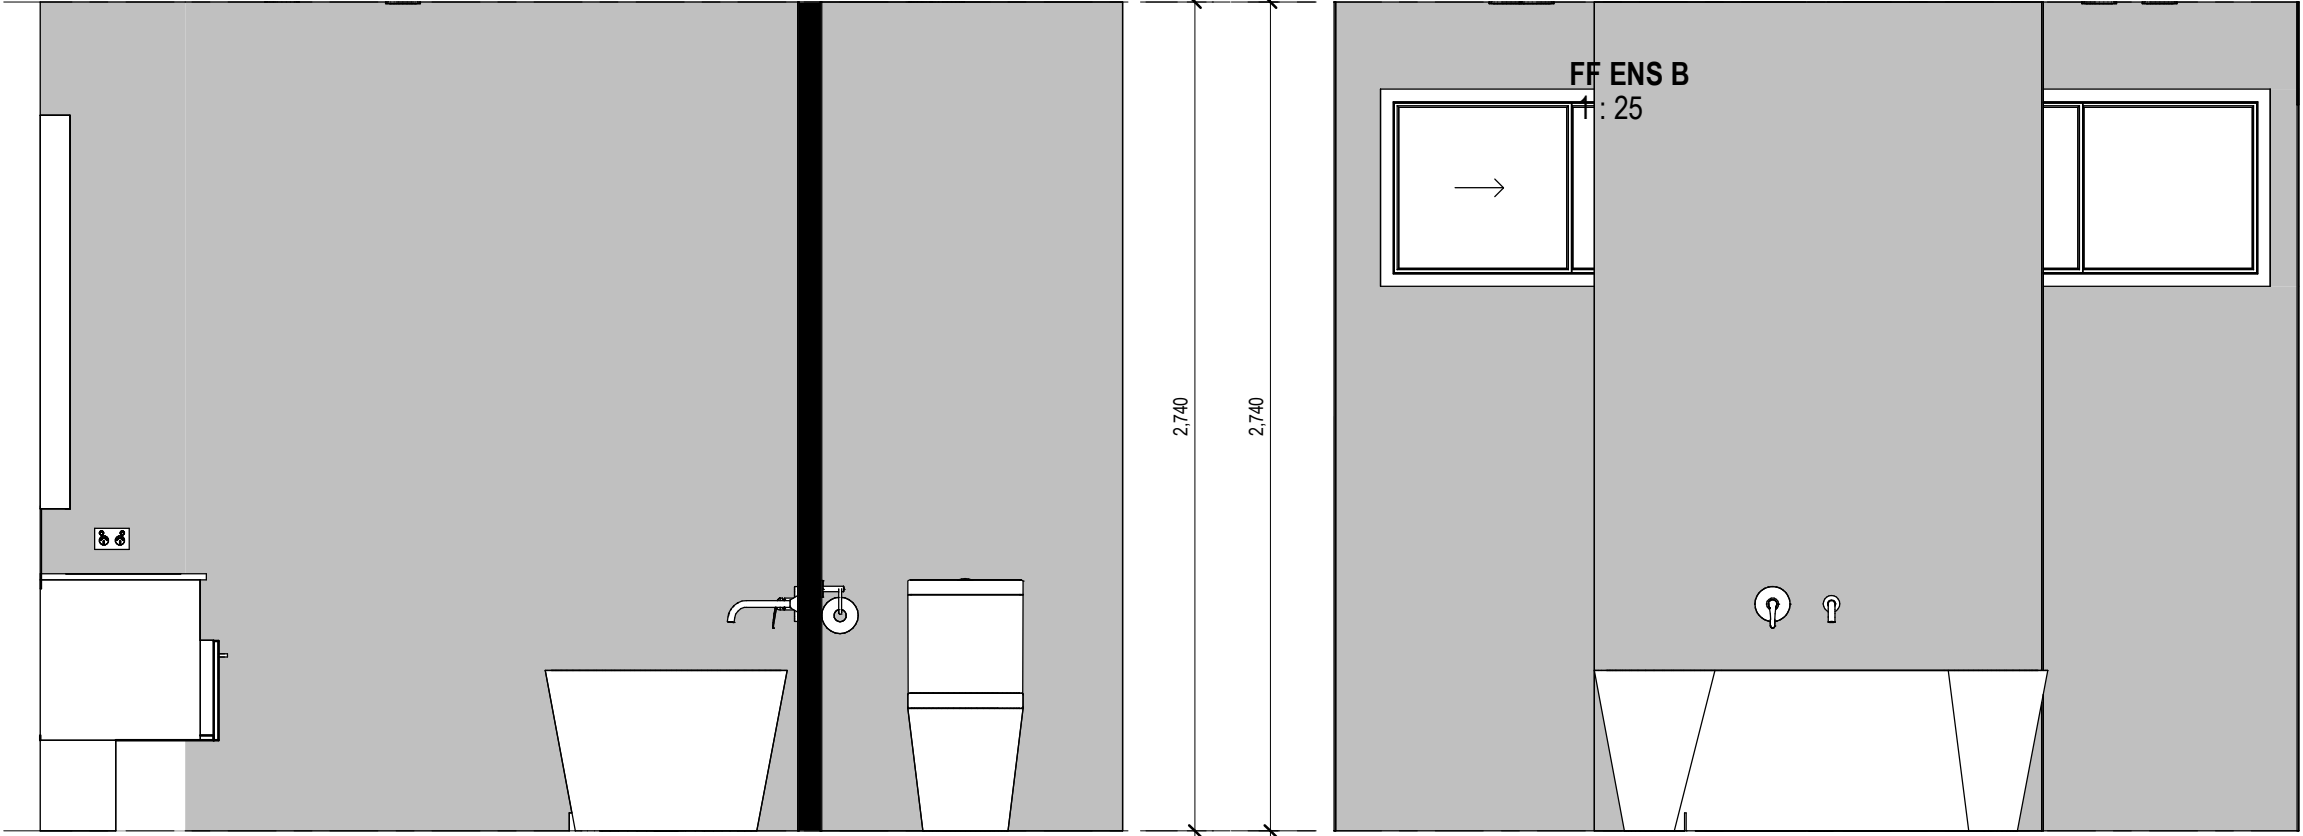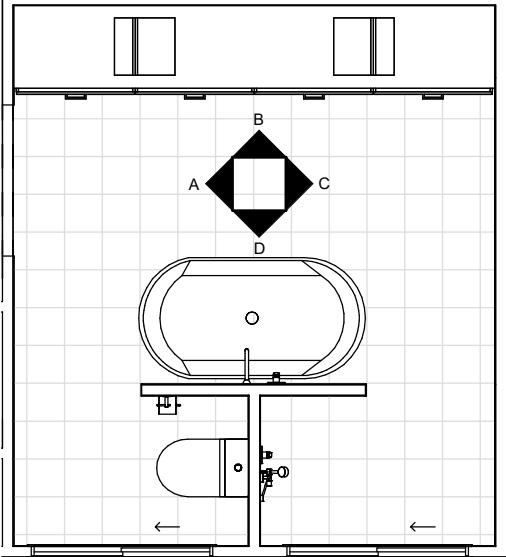


FF ENS C
1 : 25


FF ENS D
1 : 25

EST ENSUITE TILES AREA	
Type	Area m2
Ens Shower	11.17
Ens Skirting	23.44
Ens Vanity Splashback	3.19
TOTAL	37.80




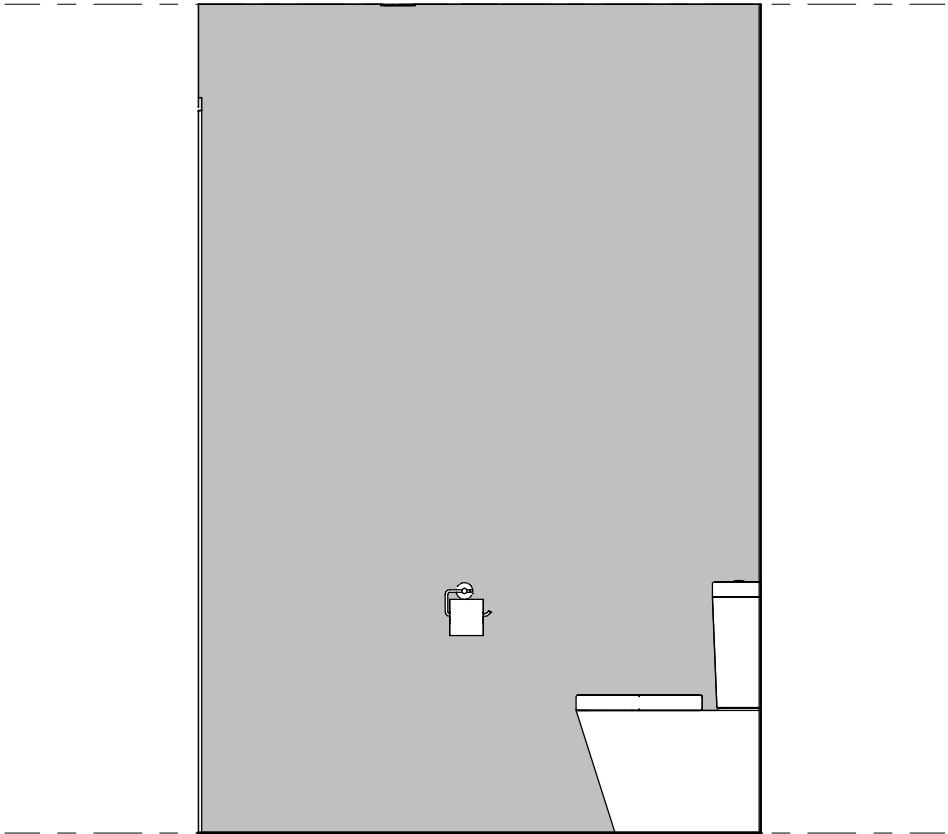


FF WC A
1 : 25

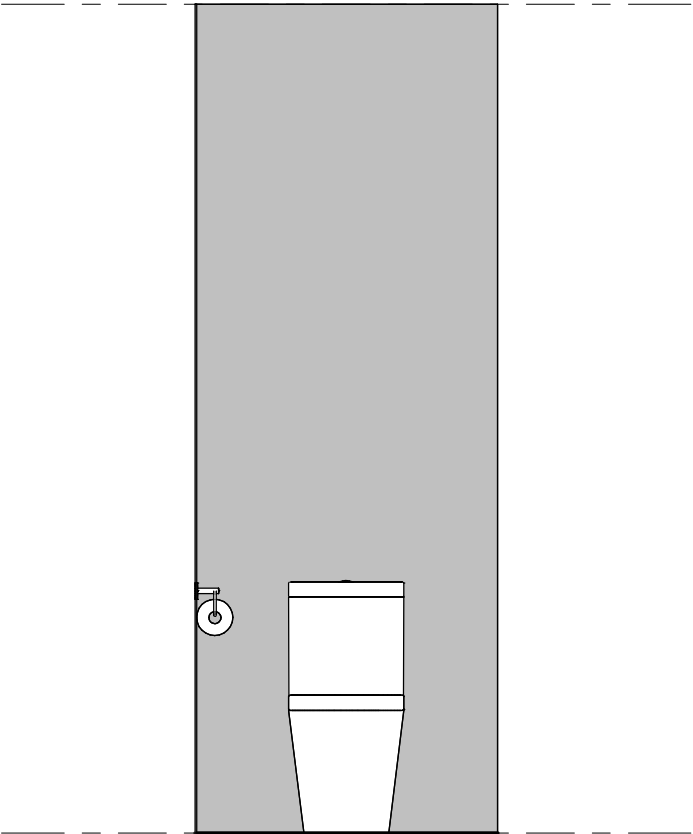


FF WC B
1 : 25

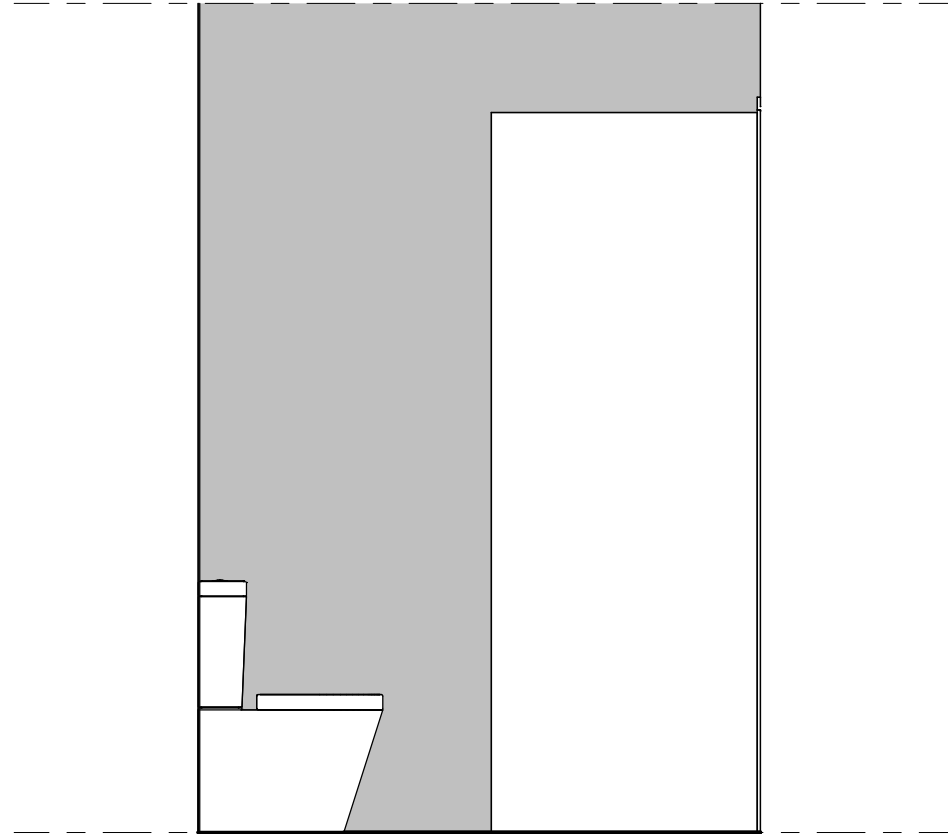

FF WC C
1 : 25

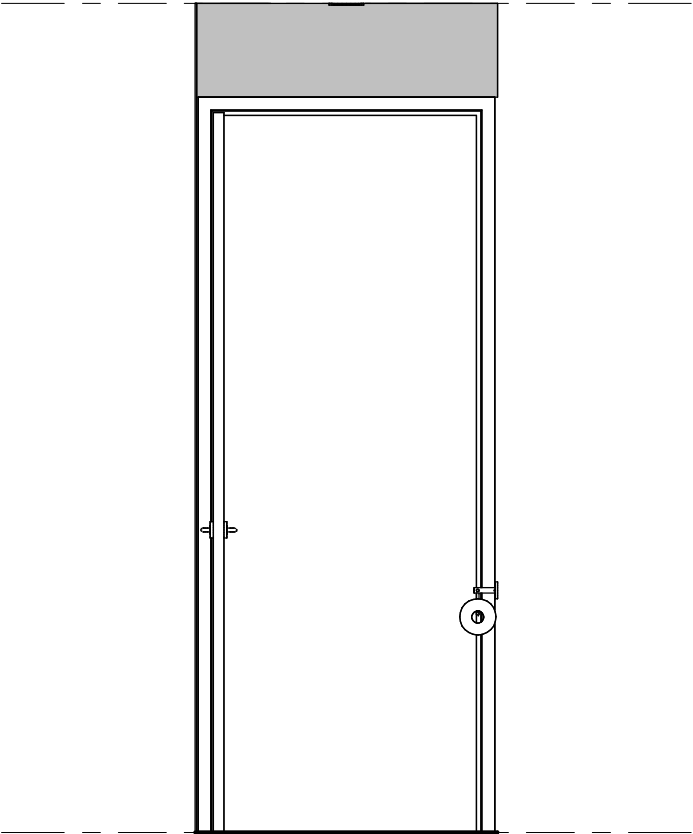


FF WC D
1 : 25

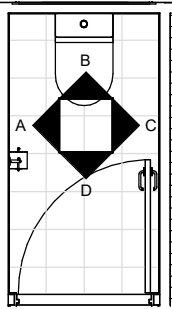


LAYOUT - FF WC
1 : 50


EST WC TILES AREA		
Type	Area m2	Description
WC Tiles	13.24	WC
TOTAL	13.24	

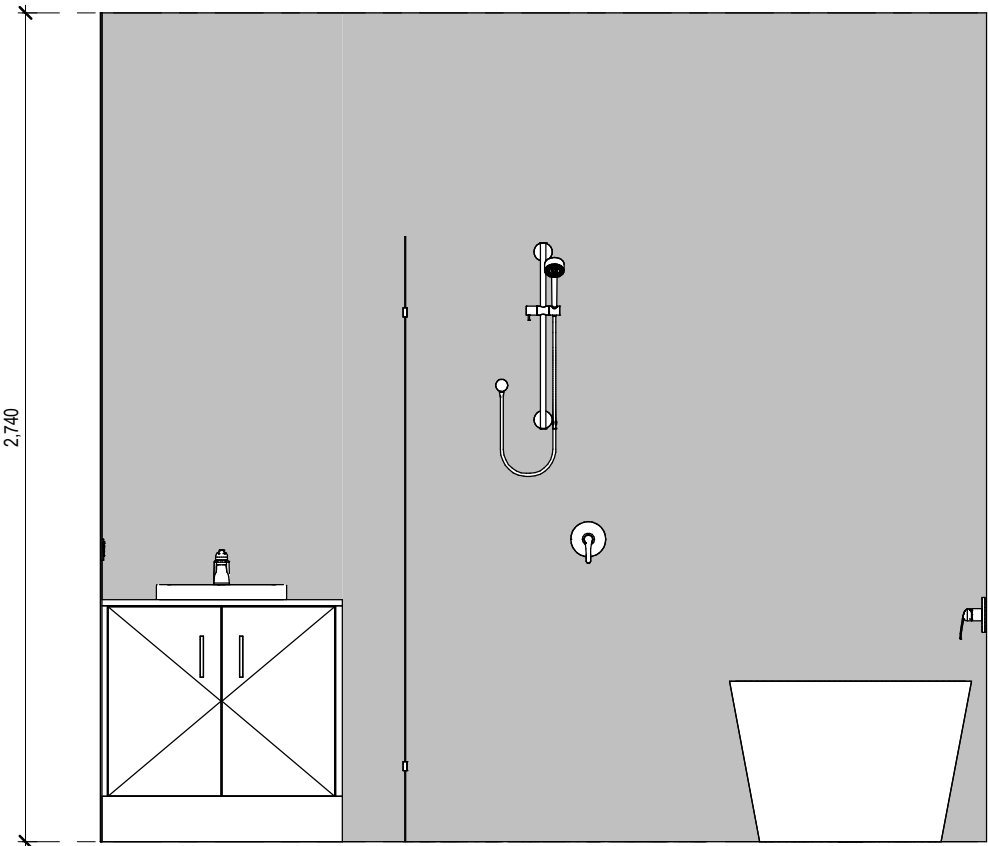

FF BATH A
1 : 25

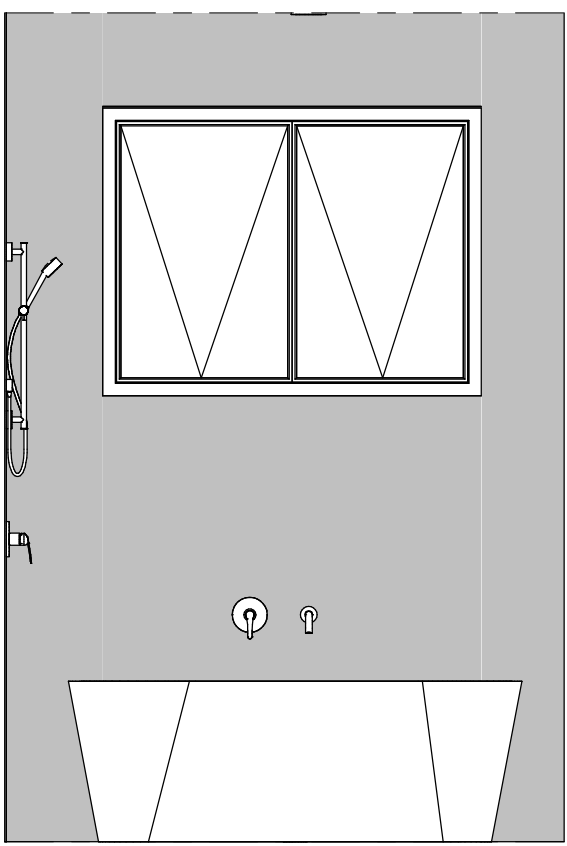


FF BATH B
1 : 25

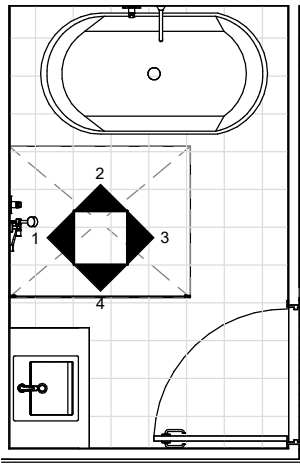


LAYOUT - FF BATH
1 : 50

EST FF BATH TILES AREA	
Type	Area m2
FF BATH Vanity	2.47
Splashback	
FF BATH Skirting	19.16
TOTAL	21.62

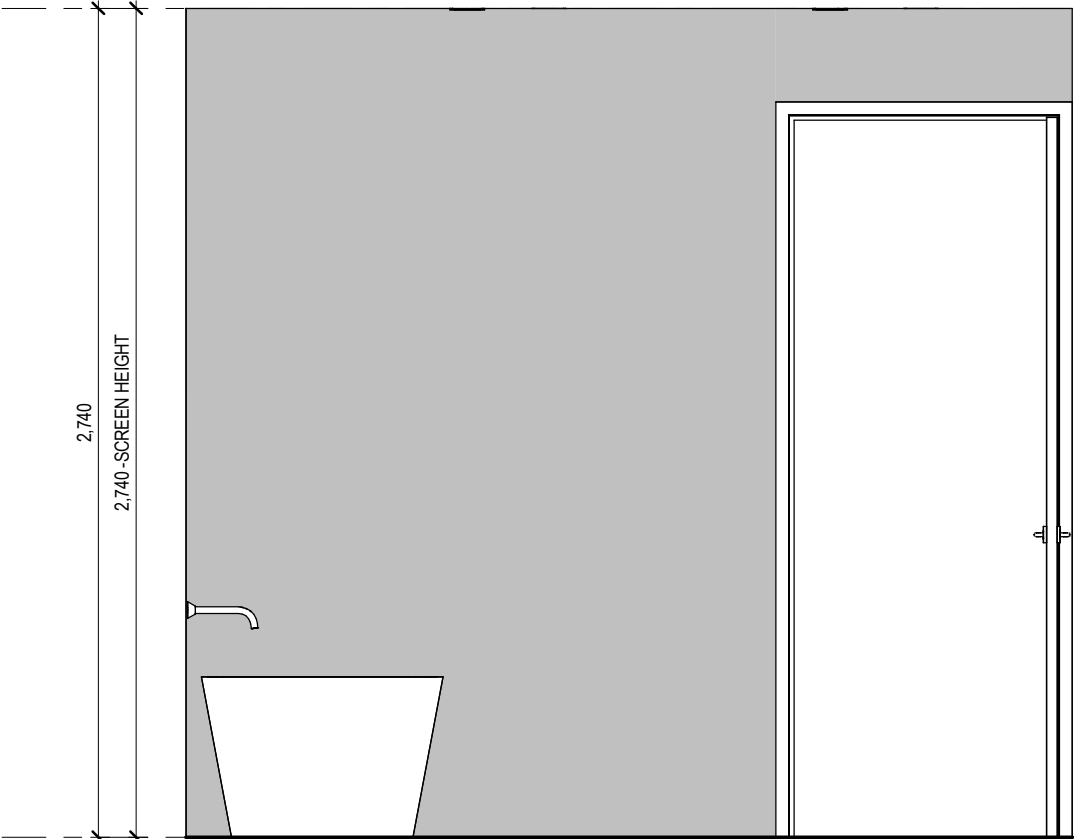

FF BATH C
1 : 25

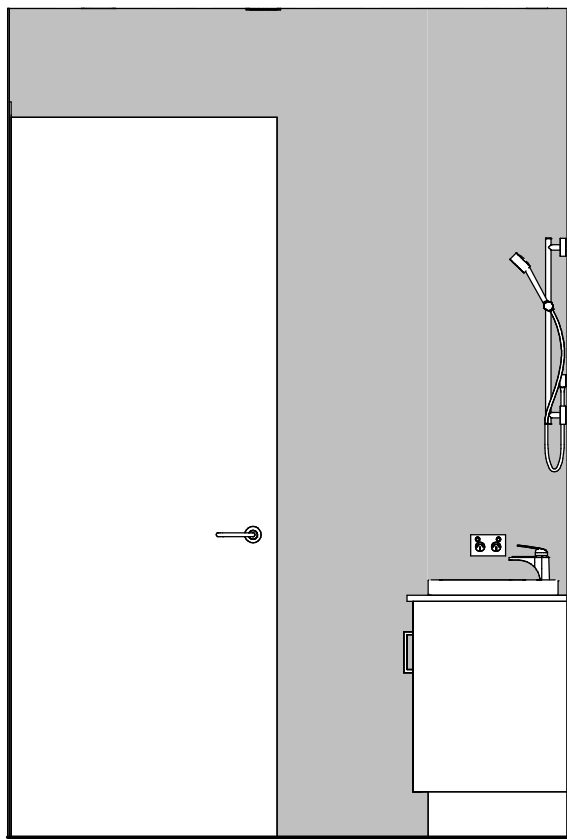

FF BATH D
1 : 25